


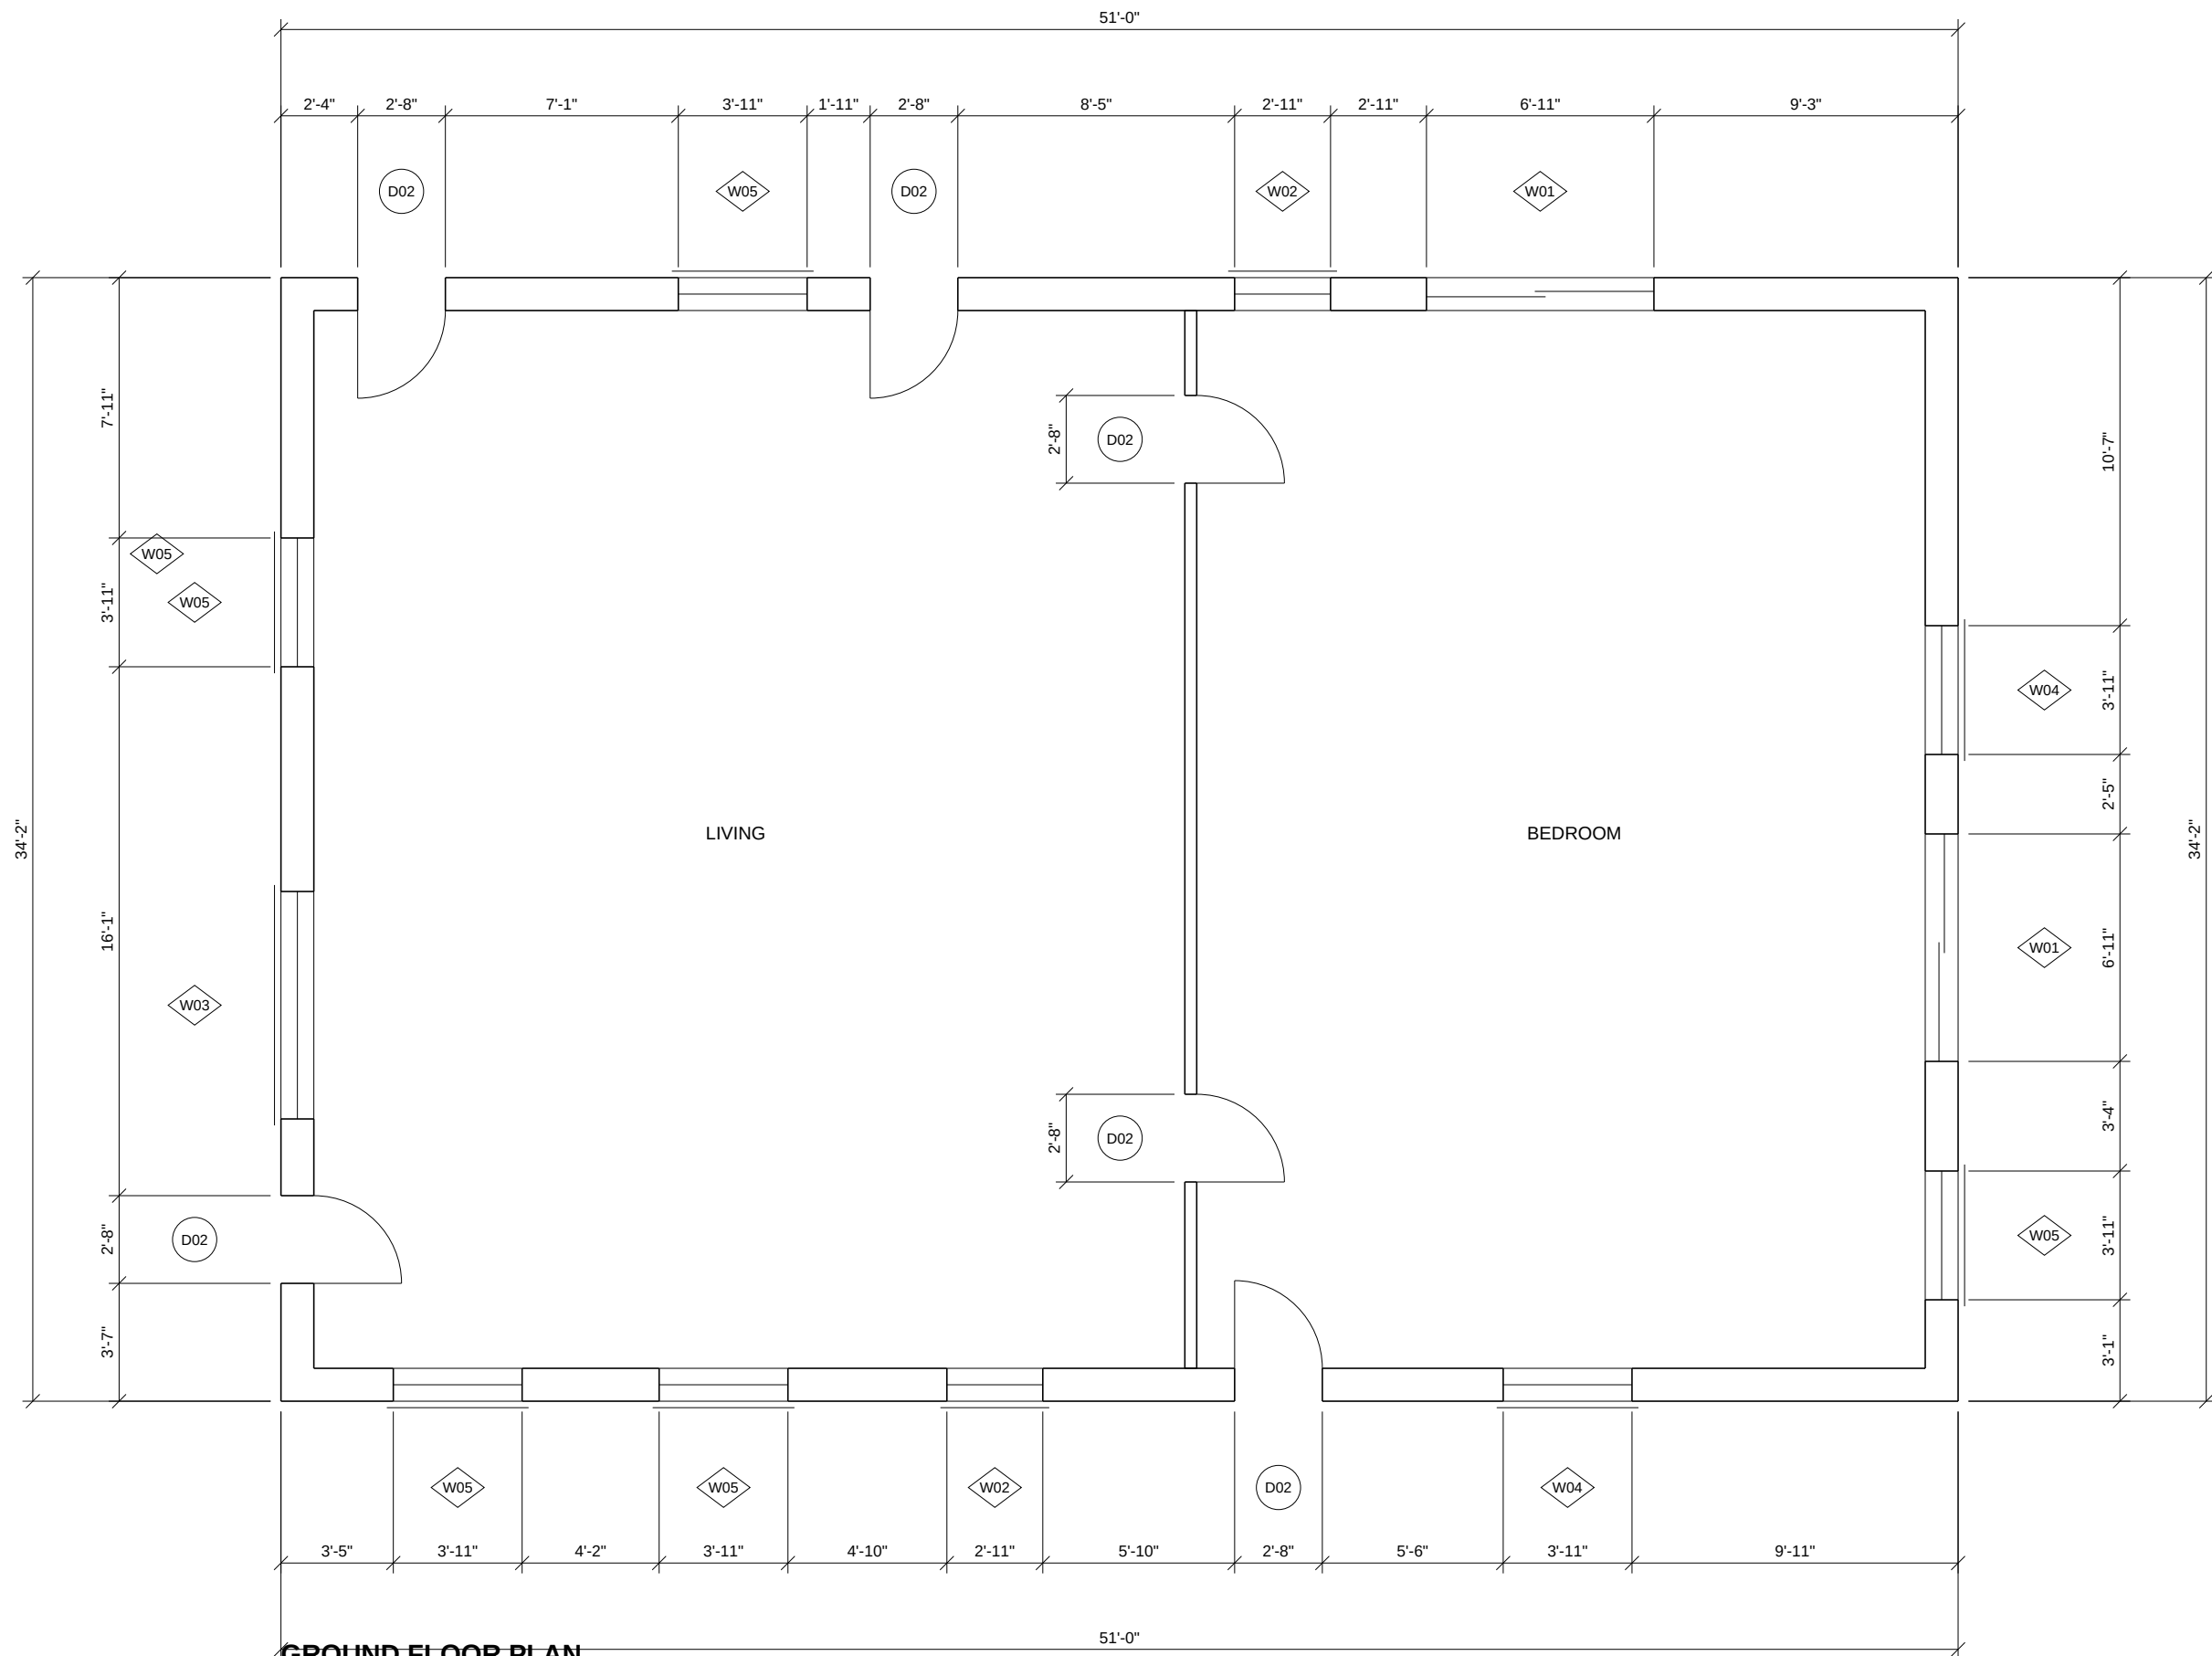


GROUND FLOOR PLAN

SCALE 3/16" = 1'-0"


REFER TO DOOR AND WINDOW SCHEDULES ON A-601.
WINDOW TAGS SHOWN IN HEXAGONS, DOOR TAGS IN CIRCLES.

STUDIO NORTH ARCHITECTS RESIDENTIAL BUILDING LOT 13, BENCHMARK AVENUE ALL DIMENSIONS IN FEET AND INCHES UNLESS NOTED OTHERWISE. DO NOT SCALE.	DRAWING TITLE	
	GROUND FLOOR PLAN	
	SCALE	DATE
	3/16" = 1'-0"	2026-09-01
	SHEET	REV
	A-101	B

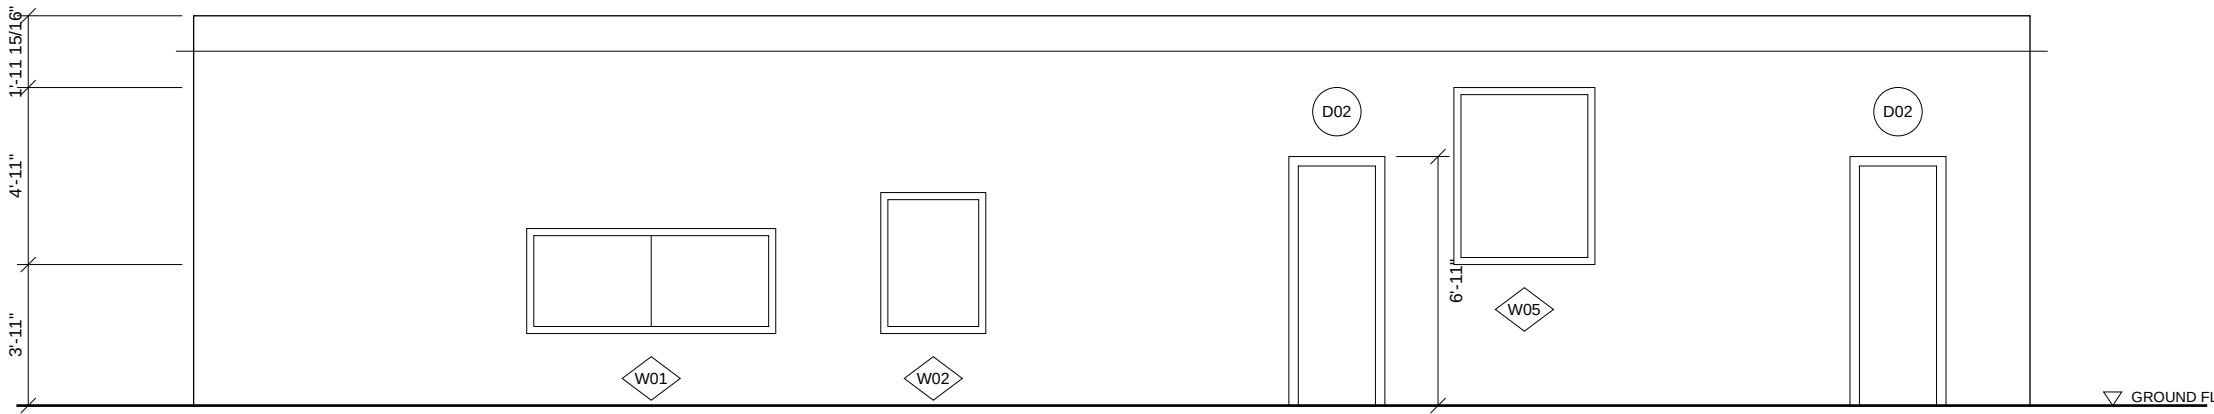

NORTH ELEVATION


SCALE 3/16" = 1'-0"

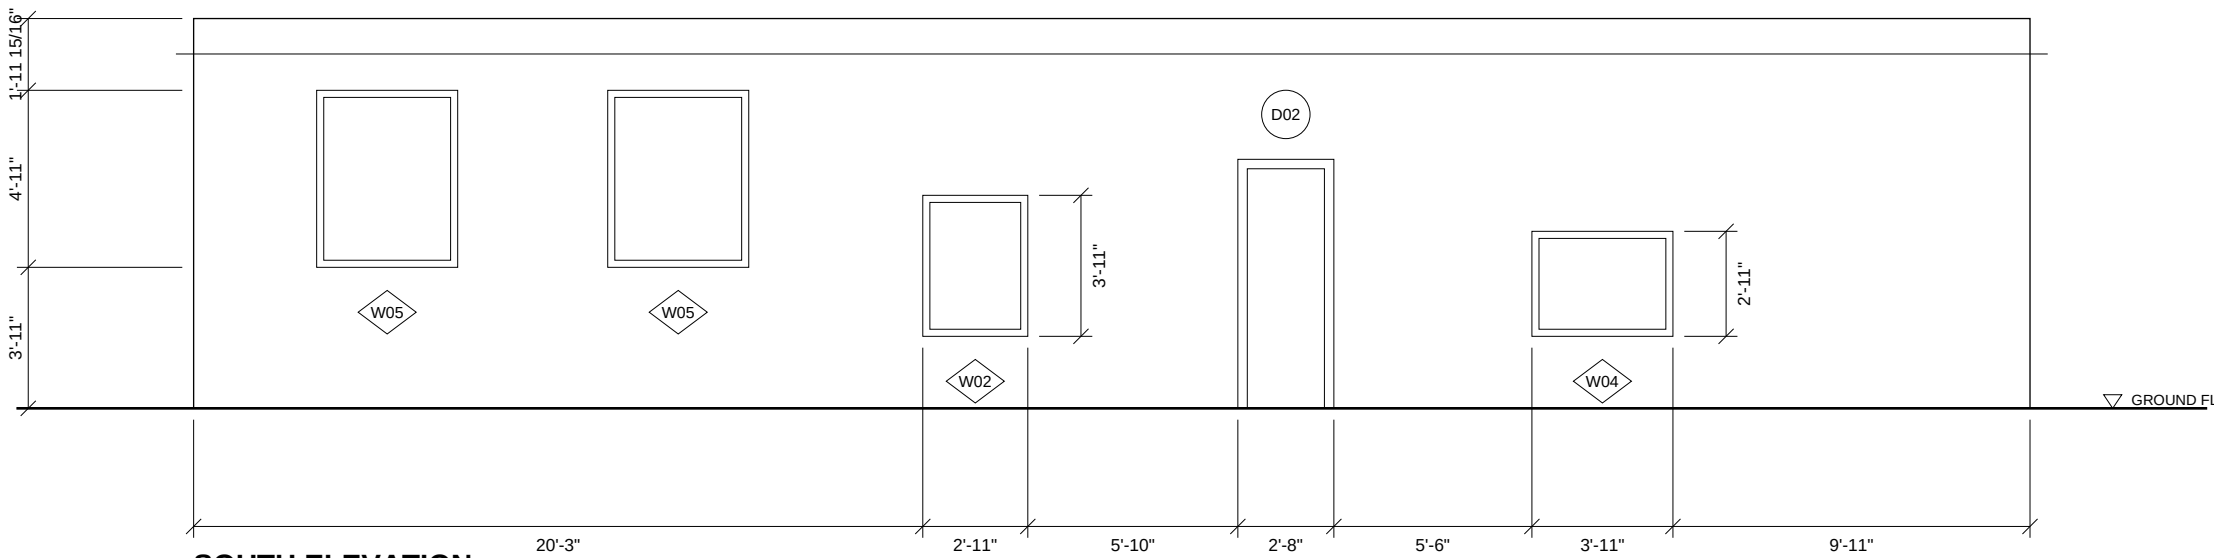

SOUTH ELEVATION


SCALE 3/16" = 1'-0"

STUDIO NORTH ARCHITECTS RESIDENTIAL BUILDING LOT 13, BENCHMARK AVENUE ALL DIMENSIONS IN FEET AND INCHES UNLESS NOTED OTHERWISE. DO NOT SCALE.	DRAWING TITLE NORTH & SOUTH ELEVATIONS	
	SCALE 3/16" = 1'-0"	DATE 2026-09-01
	SHEET A-201	REV B

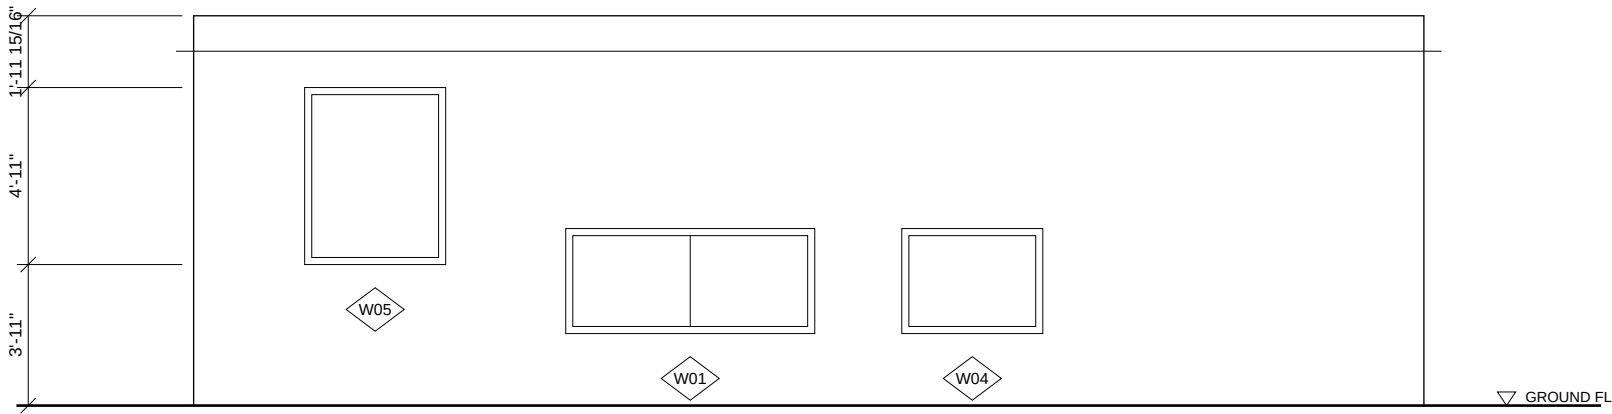

EAST ELEVATION

SCALE 3/16" = 1'-0"

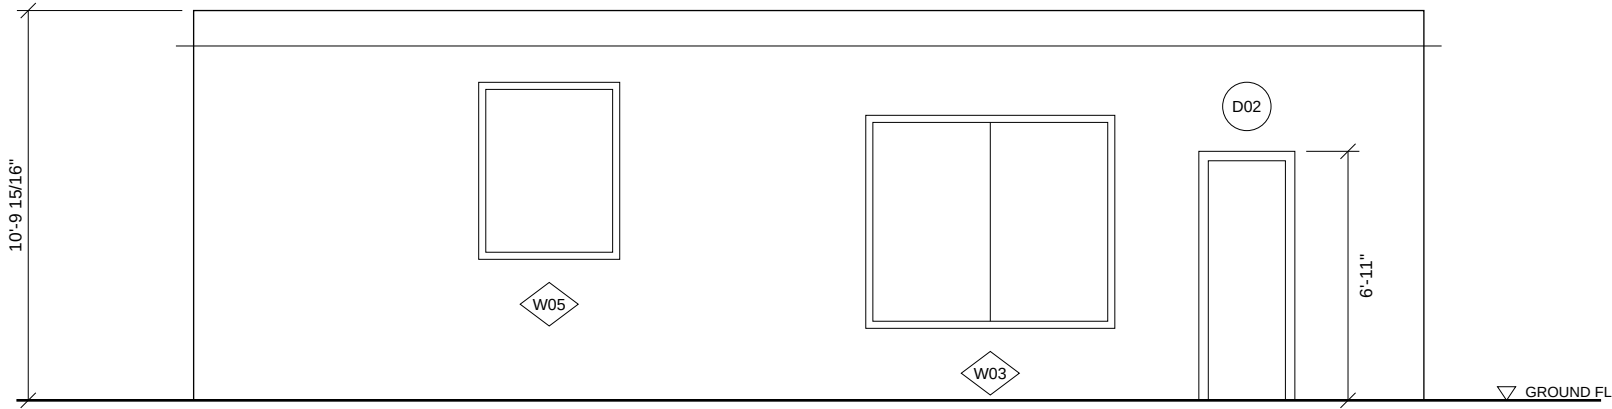

WEST ELEVATION

SCALE 3/16" = 1'-0"

STUDIO NORTH ARCHITECTS RESIDENTIAL BUILDING LOT 13, BENCHMARK AVENUE ALL DIMENSIONS IN FEET AND INCHES UNLESS NOTED OTHERWISE. DO NOT SCALE.	DRAWING TITLE EAST & WEST ELEVATIONS	
	SCALE 3/16" = 1'-0"	DATE 2026-09-01
	SHEET A-202	REV B

DOOR SCHEDULE

MARK	TYPE	WIDTH	HEIGHT	QTY	REMARKS
D01	HINGED	2'-10"	6'-11"	0	
D02	HINGED	2'-8"	6'-11"	6	

WINDOW SCHEDULE

MARK	TYPE	WIDTH	HEIGHT	SILL	QTY	REMARKS
W01	SLIDING	6'-11"	2'-11"	2'-0"	2	
W02	AWNING	2'-11"	3'-11"	2'-0"	2	
W03	AWNING	6'-11"	5'-11"	2'-0"	1	
W04	AWNING	3'-11"	2'-11"	2'-0"	5	
W05	AWNING	3'-11"	4'-11"	3'-11"	5	

NOTE: ALL SIZES ARE NOMINAL STRUCTURAL OPENING SIZES.

STUDIO NORTH ARCHITECTS RESIDENTIAL BUILDING LOT 13, BENCHMARK AVENUE ALL DIMENSIONS IN FEET AND INCHES UNLESS NOTED OTHERWISE. DO NOT SCALE.	DRAWING TITLE DOOR & WINDOW SCHEDULES	
	SCALE NTS	DATE 2026-09-01
	SHEET A-601	REV B