



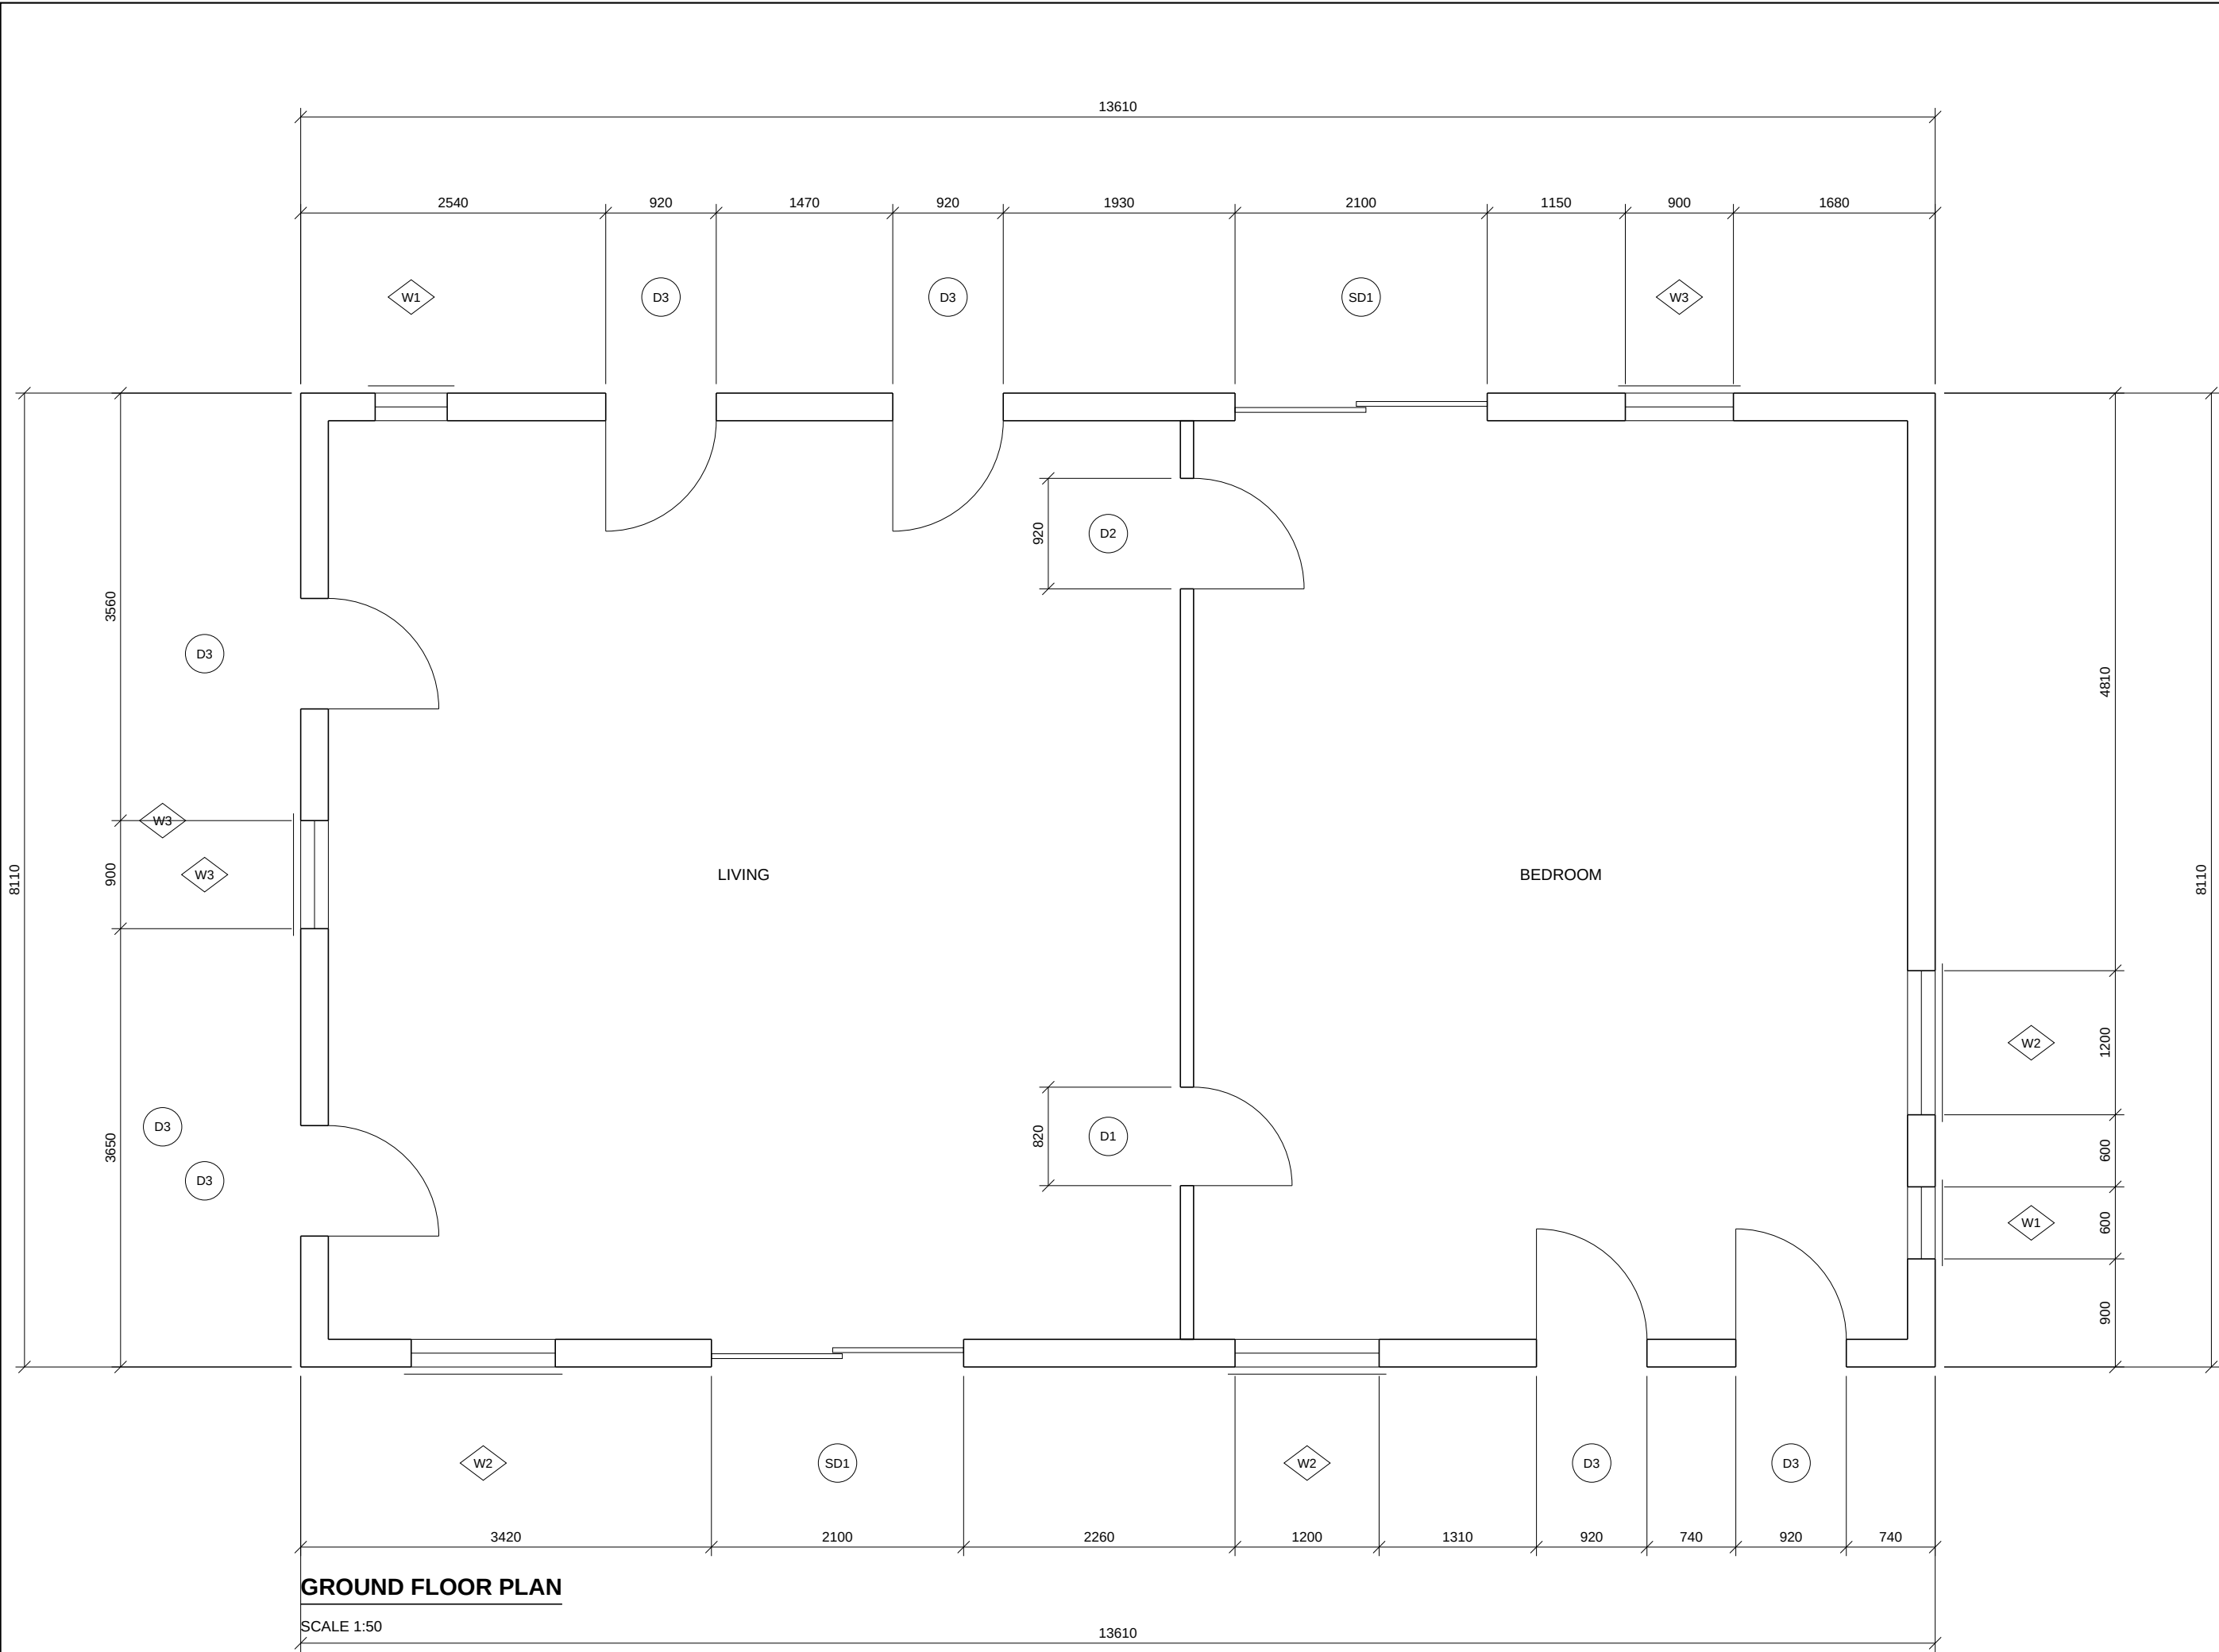


REFER TO DOOR AND WINDOW SCHEDULES ON A-601.
WINDOW TAGS SHOWN IN HEXAGONS, DOOR TAGS IN CIRCLES.

STUDIO NORTH ARCHITECTS RESIDENTIAL BUILDING LOT 15, BENCHMARK AVENUE ALL DIMENSIONS IN MILLIMETRES UNLESS NOTED OTHERWISE, DO NOT SCALE.	DRAWING TITLE	
	GROUND FLOOR PLAN	
	SCALE	DATE
	1:50	2026-09-01
	SHEET	REV
	A-101	B

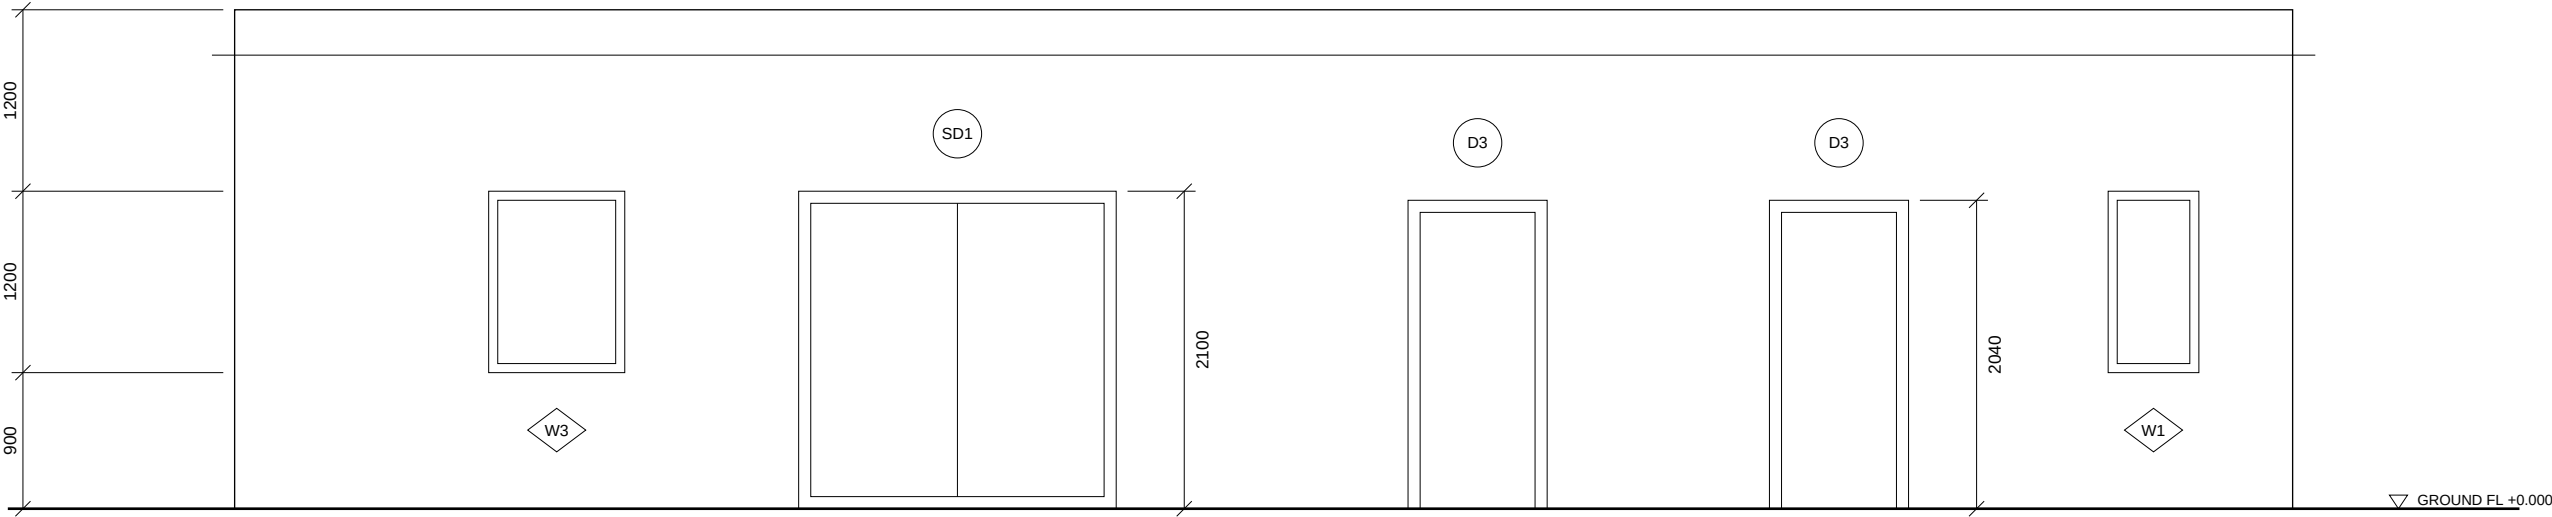

NORTH ELEVATION

SCALE 1:50

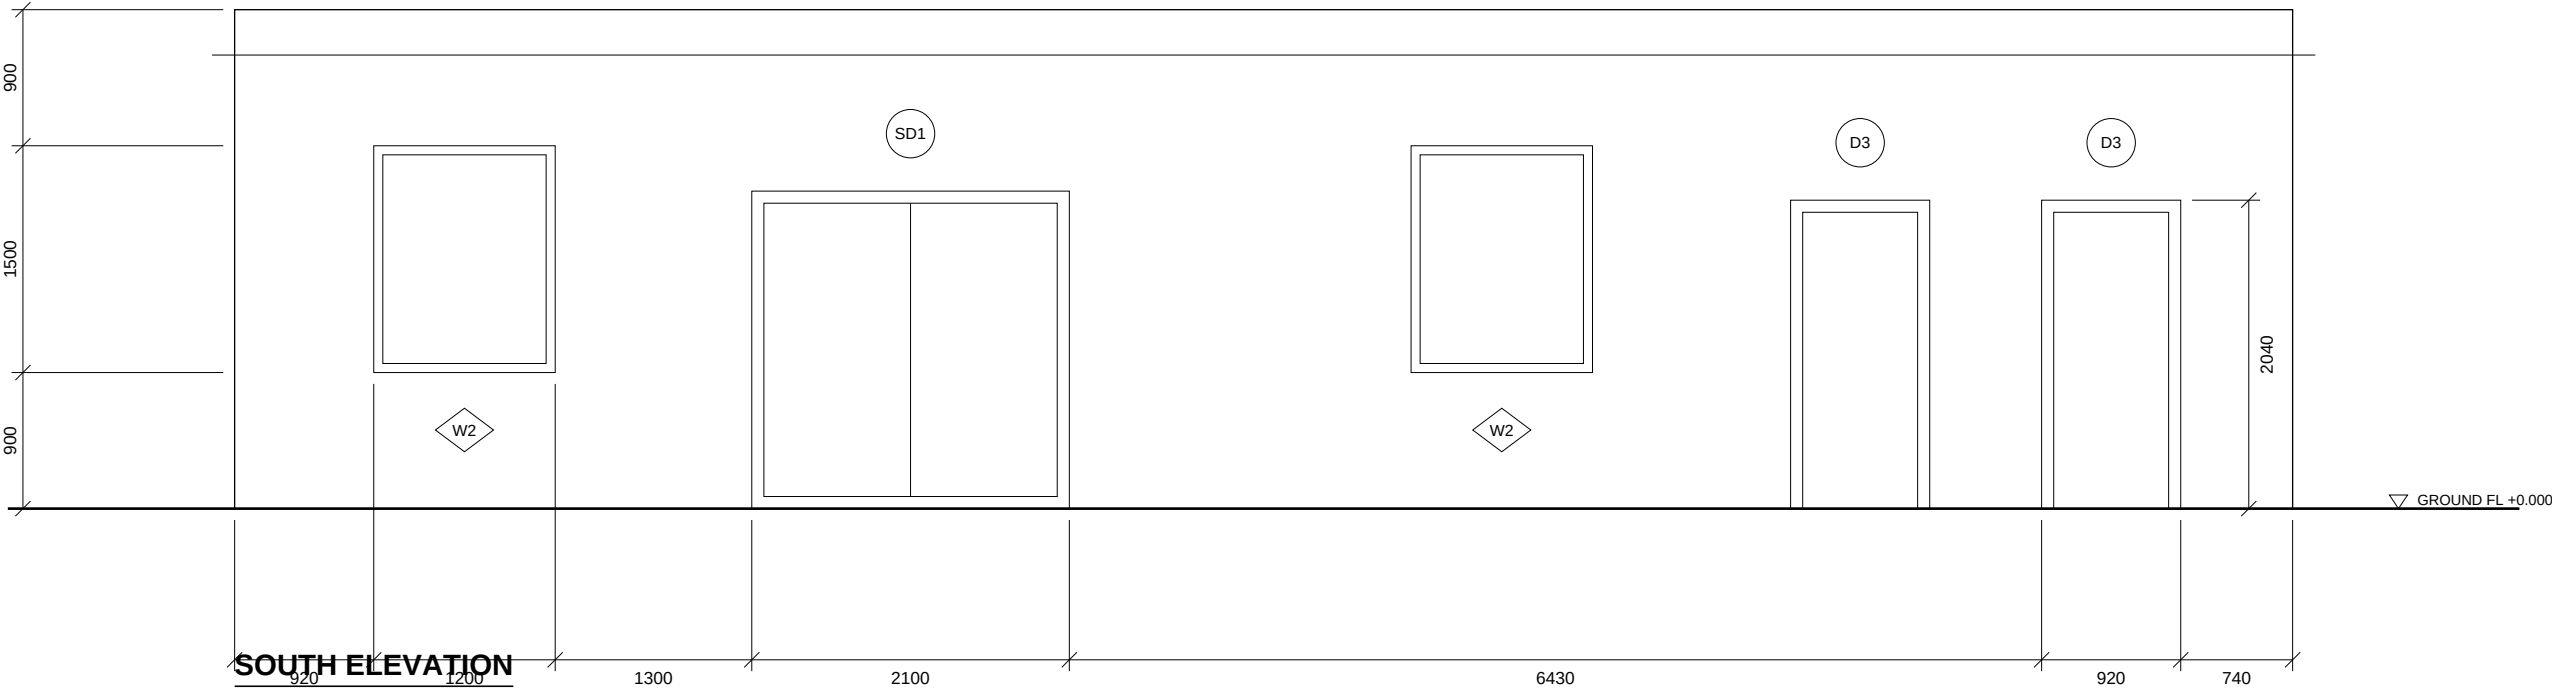

SOUTH ELEVATION

SCALE 1:50

STUDIO NORTH ARCHITECTS

RESIDENTIAL BUILDING
LOT 15, BENCHMARK AVENUE

ALL DIMENSIONS IN MILLIMETRES UNLESS NOTED
OTHERWISE, DO NOT SCALE.

DRAWING TITLE
NORTH & SOUTH ELEVATIONS

SCALE

1:50

SHEET


A-201

DATE

2026-09-01


REV

B

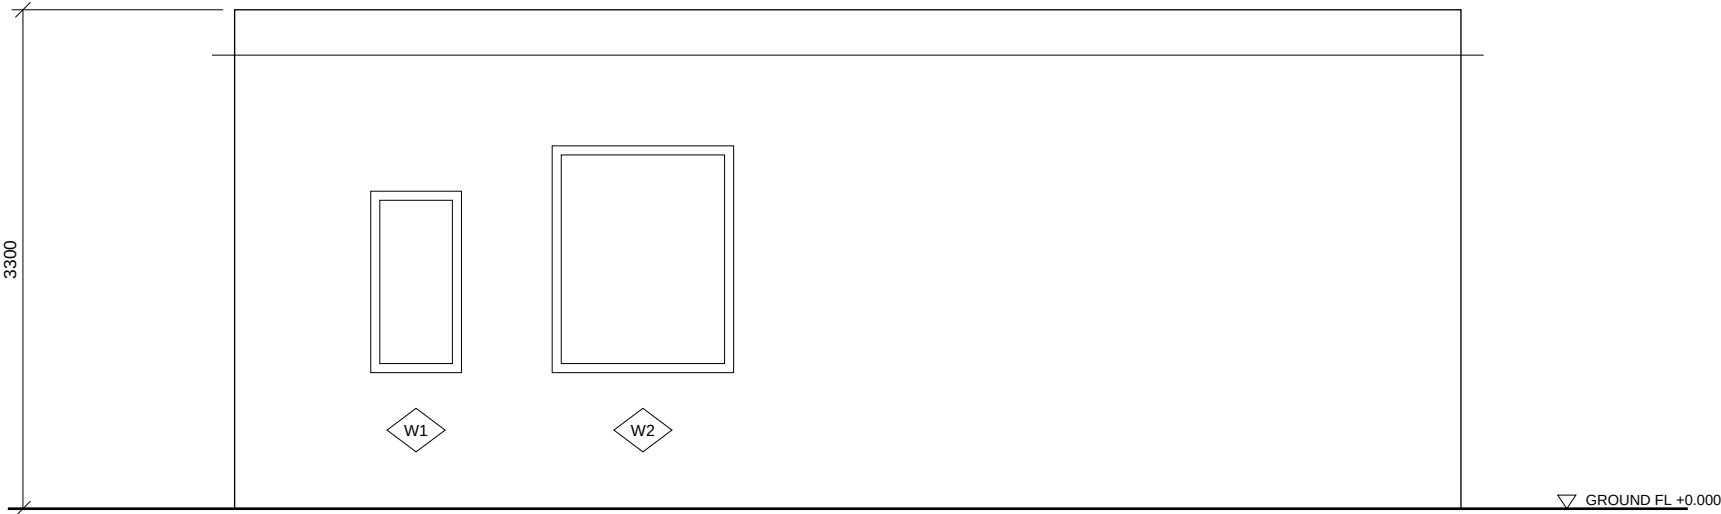

EAST ELEVATION

SCALE 1:50

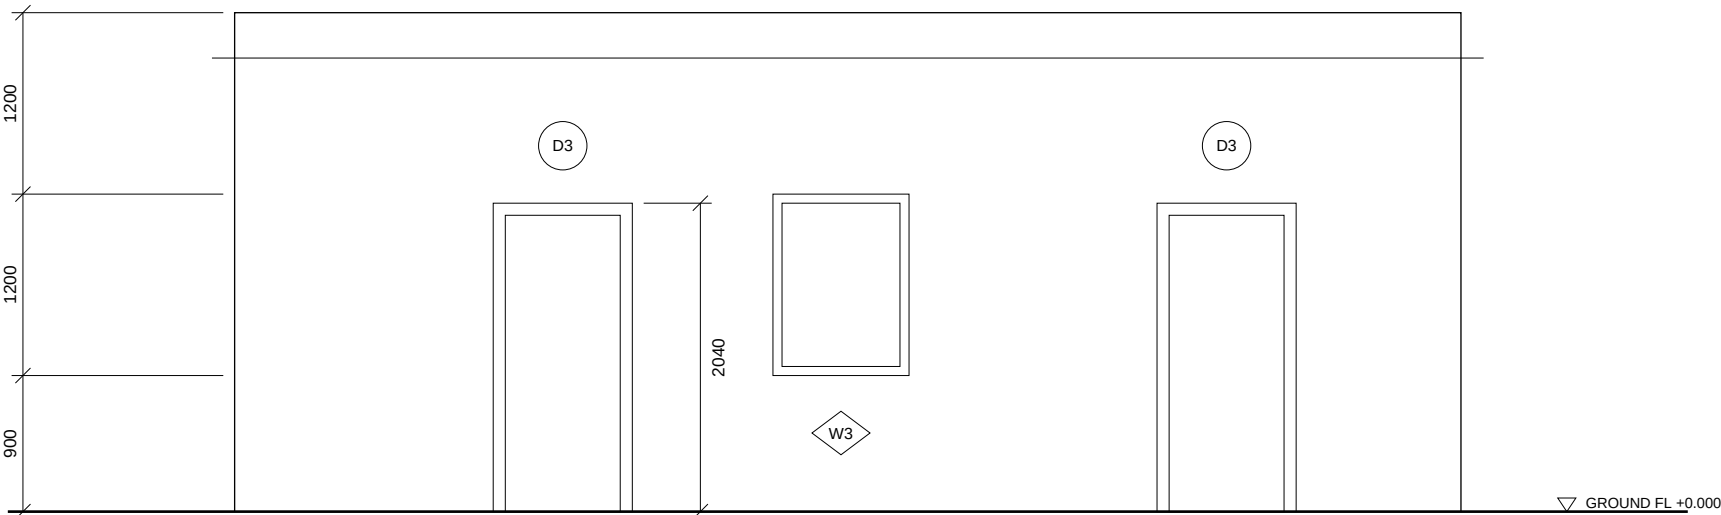

WEST ELEVATION

SCALE 1:50

STUDIO NORTH ARCHITECTS RESIDENTIAL BUILDING LOT 15, BENCHMARK AVENUE ALL DIMENSIONS IN MILLIMETRES UNLESS NOTED OTHERWISE, DO NOT SCALE.	DRAWING TITLE	
	EAST & WEST ELEVATIONS	
	SCALE	DATE
	1:50	2026-09-01
	SHEET	REV
	A-202	B

DOOR SCHEDULE

MARK	TYPE	WIDTH	HEIGHT	QTY	REMARKS
D1	HINGED	820	2340	1	
D2	HINGED	920	2100	2	
SD1	SLIDING DOOR	2100	2100	2	

WINDOW SCHEDULE

MARK	TYPE	WIDTH	HEIGHT	SILL	QTY	REMARKS
W1	AWNING	600	1200	900	2	
W2	AWNING	1200	1500	900	3	
W3	AWNING	900	1200	900	2	

NOTE: ALL SIZES ARE NOMINAL STRUCTURAL OPENING SIZES.

STUDIO NORTH ARCHITECTS RESIDENTIAL BUILDING LOT 15, BENCHMARK AVENUE ALL DIMENSIONS IN MILLIMETRES UNLESS NOTED OTHERWISE, DO NOT SCALE.	DRAWING TITLE DOOR & WINDOW SCHEDULES	
	SCALE NTS	DATE 2026-09-01
	SHEET A-601	REV B