



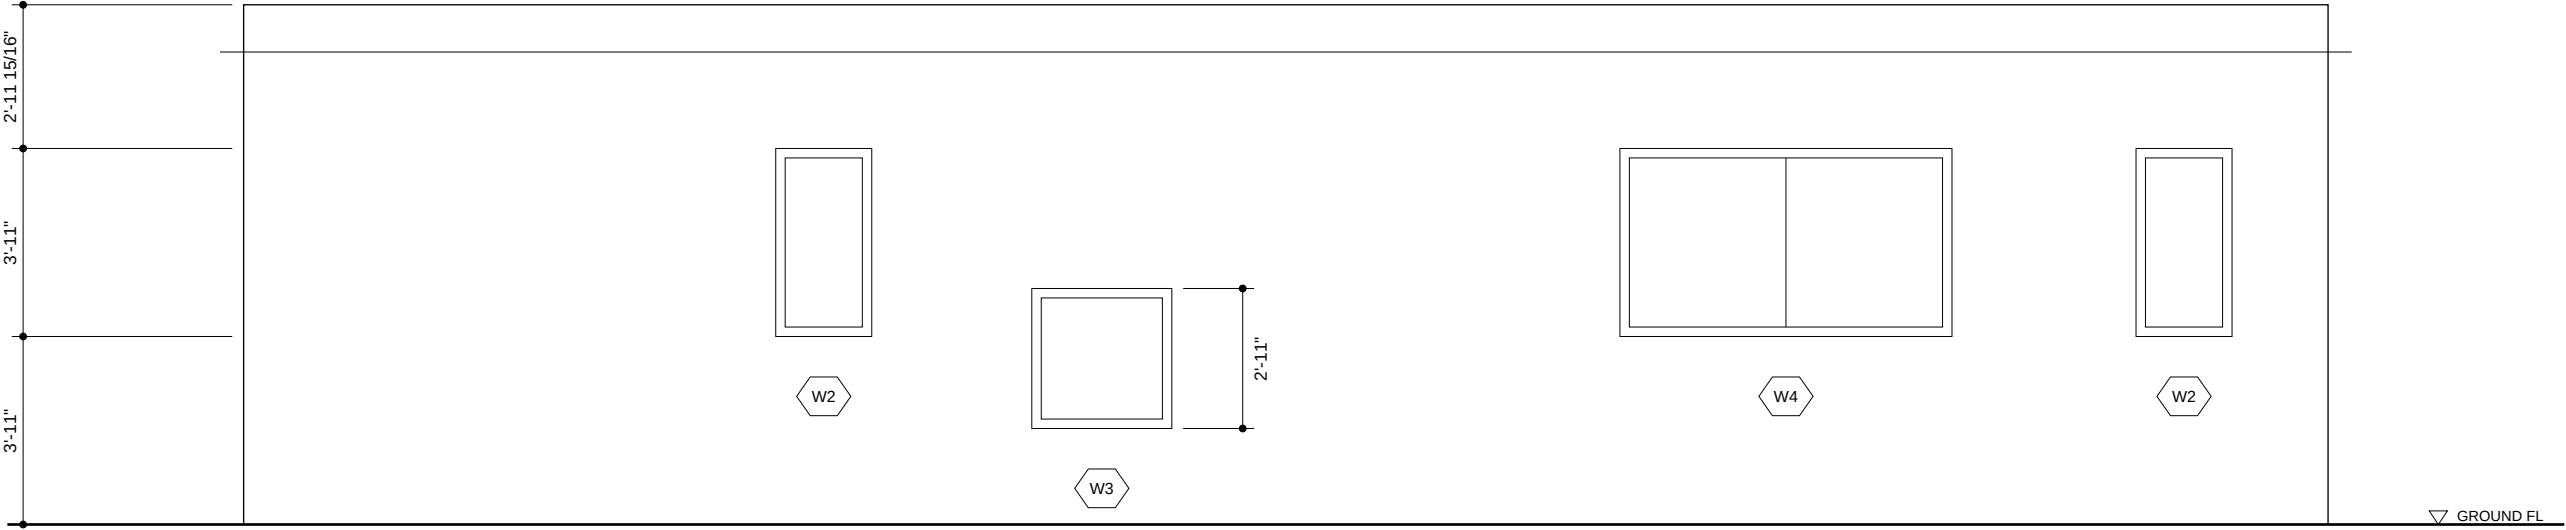

NORTH ELEVATION

SCALE 1/4" = 1'-0"

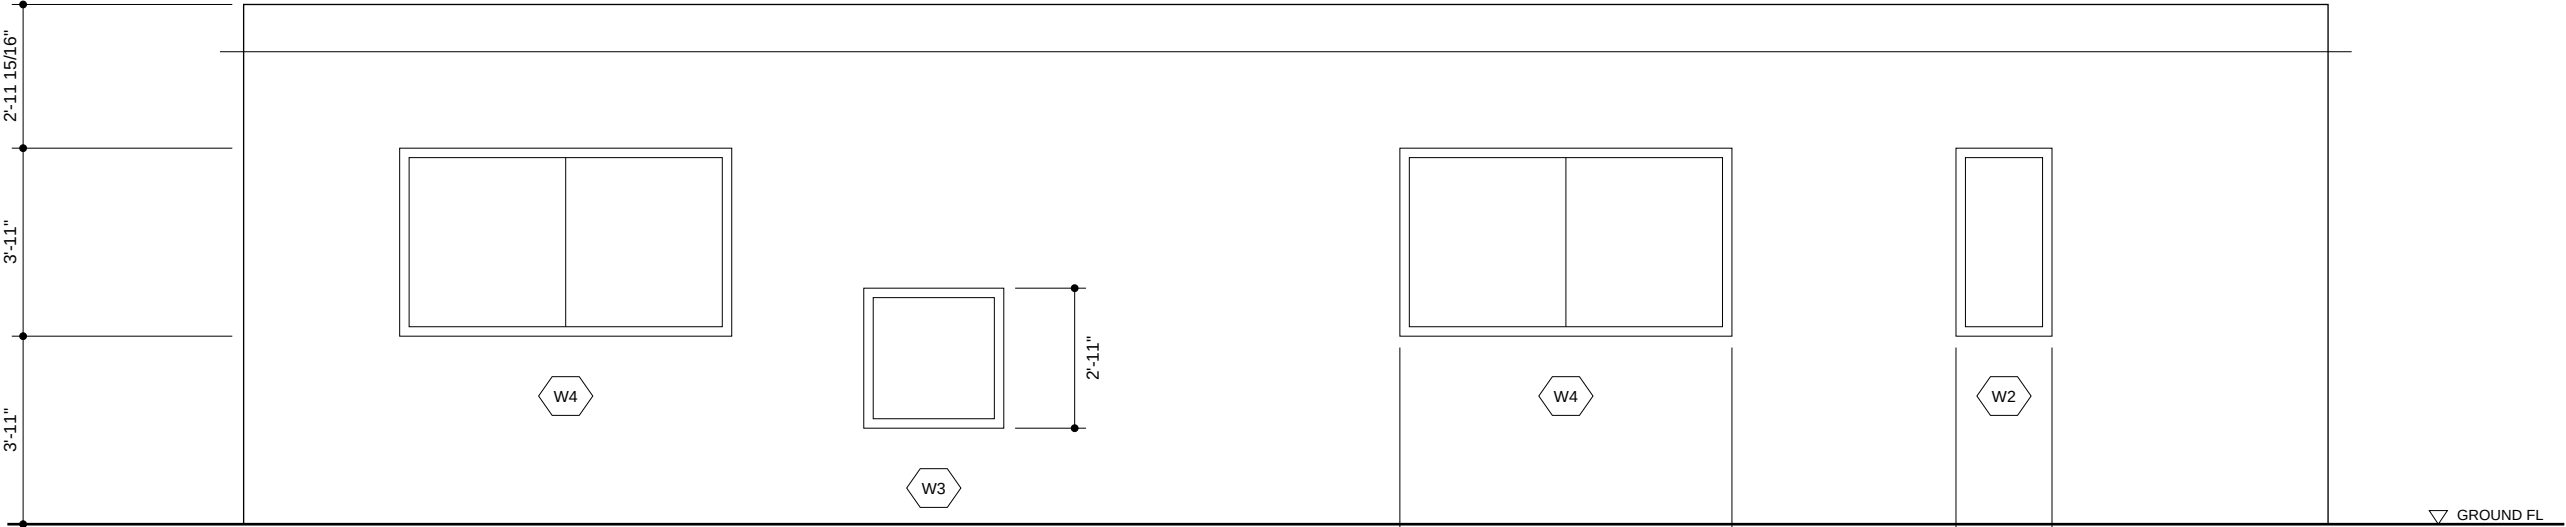

SOUTH ELEVATION

SCALE 1/4" = 1'-0"

STUDIO NORTH ARCHITECTS
RESIDENTIAL BUILDING
LOT 18, BENCHMARK AVENUE

ALL DIMENSIONS IN FEET AND INCHES UNLESS
NOTED OTHERWISE. DO NOT SCALE.


DRAWING TITLE
NORTH & SOUTH ELEVATIONS

SCALE
1/4" = 1'-0"

SHEET
A-201


DATE
2026-09-01

REV
B

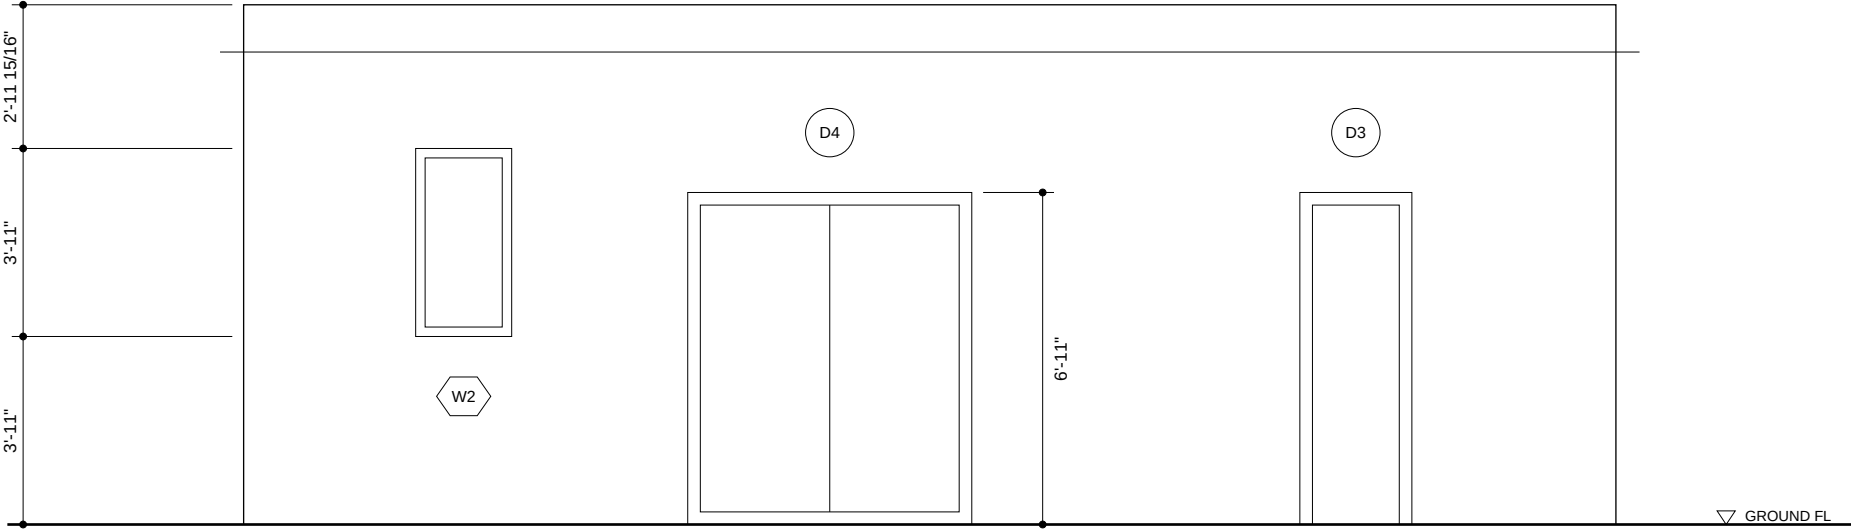

EAST ELEVATION

SCALE 1/4" = 1'-0"

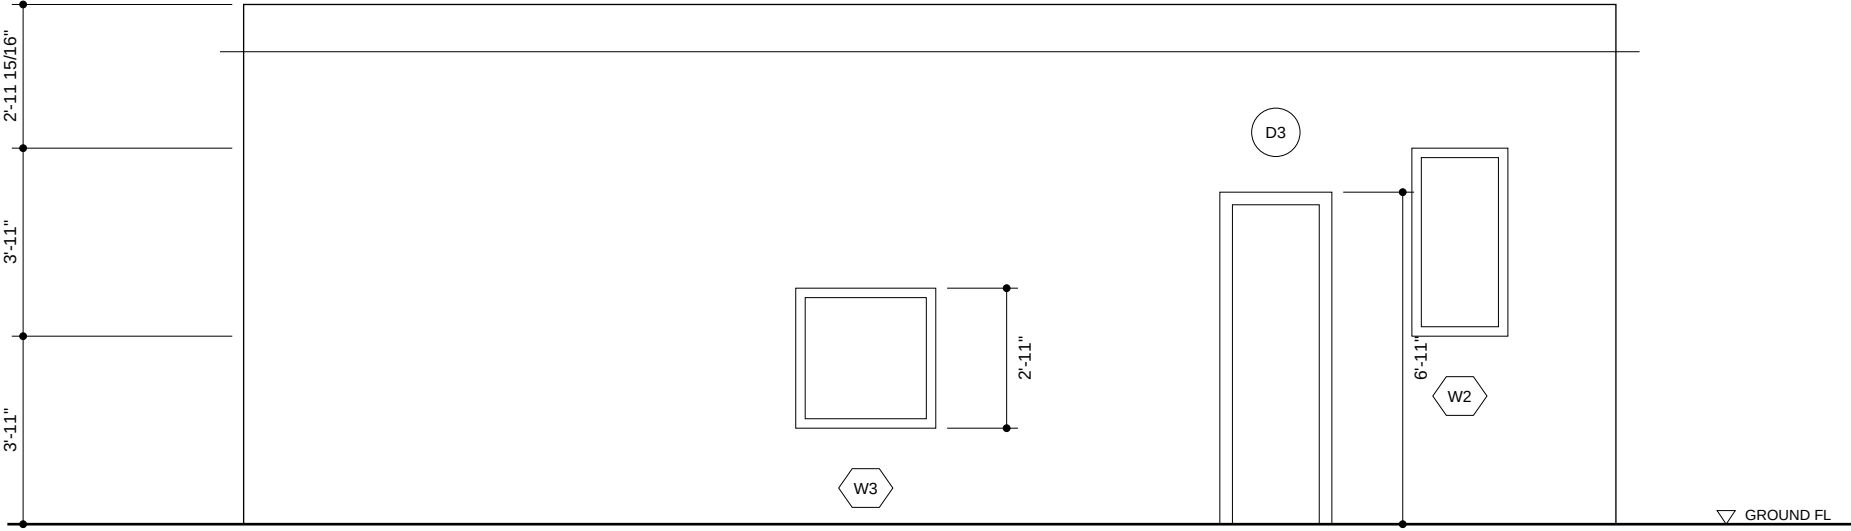

WEST ELEVATION

SCALE 1/4" = 1'-0"

STUDIO NORTH ARCHITECTS RESIDENTIAL BUILDING LOT 18, BENCHMARK AVENUE ALL DIMENSIONS IN FEET AND INCHES UNLESS NOTED OTHERWISE. DO NOT SCALE.	DRAWING TITLE	
	EAST & WEST ELEVATIONS	
	SCALE	DATE
	1/4" = 1'-0"	2026-09-01
	SHEET	REV
	A-202	B

DOOR SCHEDULE

MARK	TYPE	WIDTH	HEIGHT	QTY	REMARKS
D1	HINGED	2'-8"	7'-8"	1	
D2	HINGED	2'-10"	6'-11"	0	
D3	HINGED	2'-4"	6'-11"	3	
D4	FRENCH DOORS	5'-11"	6'-11"	1	

WINDOW SCHEDULE

MARK	TYPE	WIDTH	HEIGHT	SILL	QTY	REMARKS
W1	AWNING	3'-11"	2'-11"	2'-11"	0	
W2	AWNING	2'-0"	3'-11"	3'-11"	5	
W3	AWNING	2'-11"	2'-11"	2'-0"	3	
W4	AWNING	6'-11"	3'-11"	3'-11"	3	

NOTE: ALL SIZES ARE NOMINAL STRUCTURAL OPENING SIZES.

STUDIO NORTH ARCHITECTS RESIDENTIAL BUILDING LOT 18, BENCHMARK AVENUE ALL DIMENSIONS IN FEET AND INCHES UNLESS NOTED OTHERWISE. DO NOT SCALE.	DRAWING TITLE DOOR & WINDOW SCHEDULES	
	SCALE NTS	DATE 2026-09-01
	SHEET A-601	REV B