



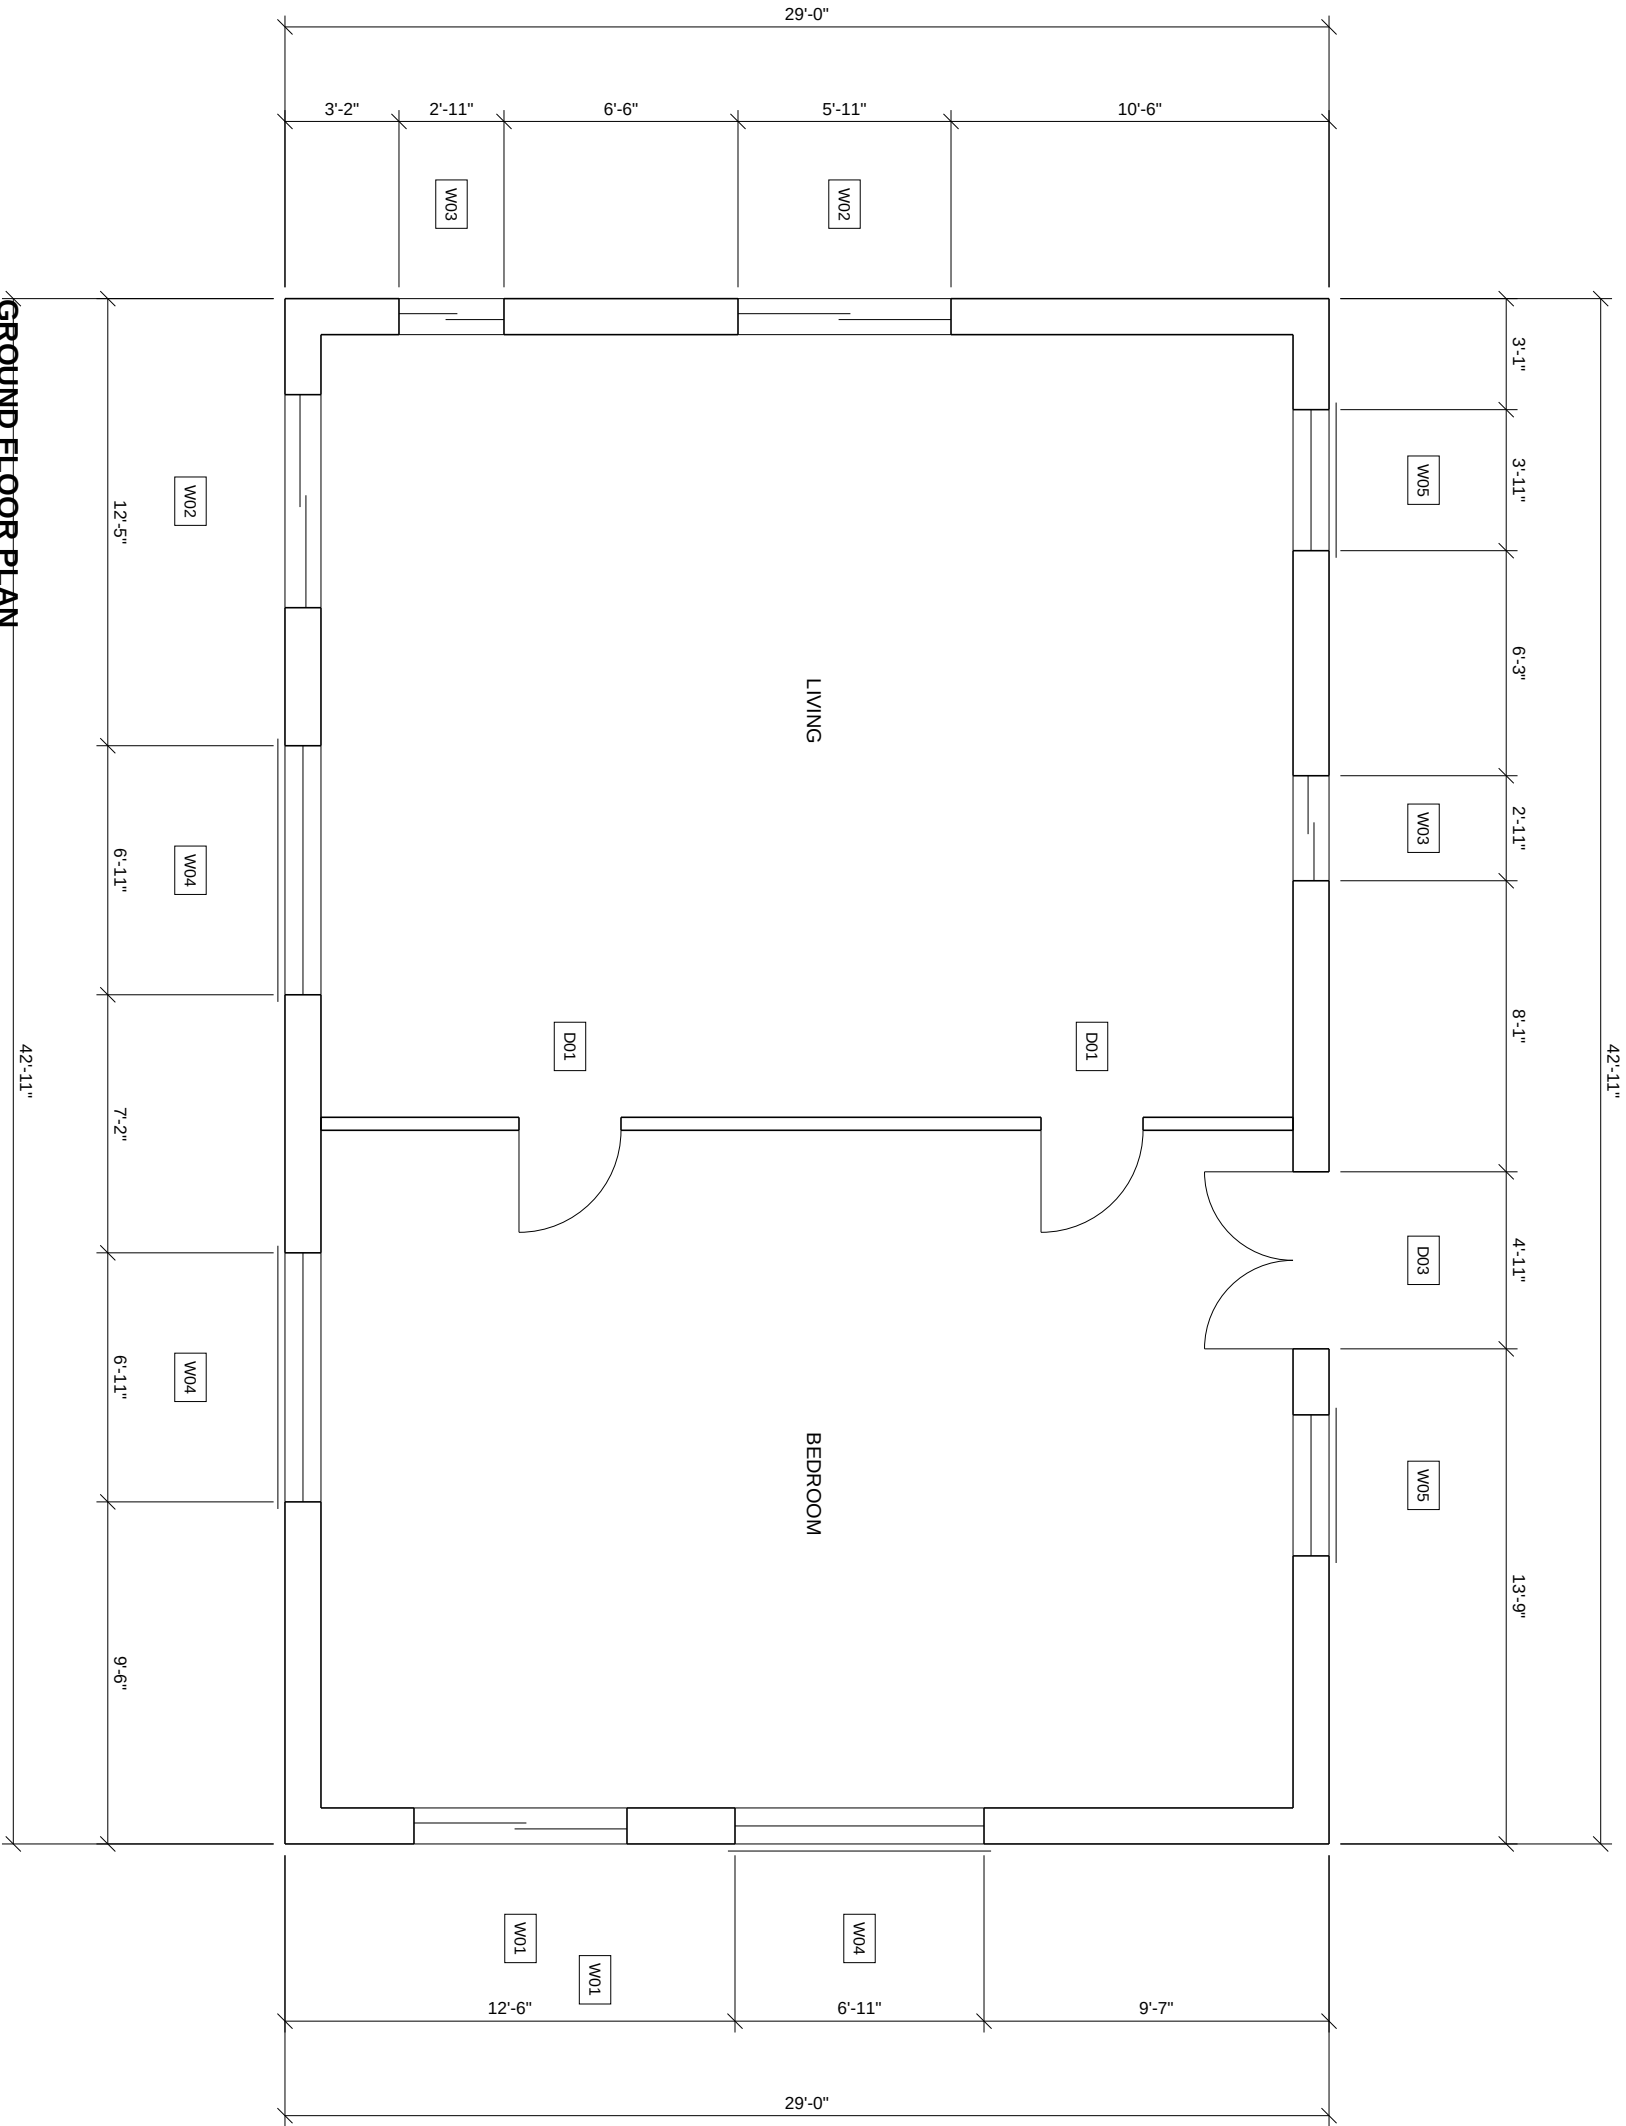


REFER TO DOOR AND WINDOW SCHEDULES ON A-601.
WINDOW TAGS SHOWN IN HEXAGONS, DOOR TAGS IN CIRCLES.

STUDIO NORTH ARCHITECTS		DRAWING TITLE	
RESIDENTIAL BUILDING		GROUND FLOOR PLAN	
LOT 21, BENCHMARK AVENUE		SCALE	DATE
ALL DIMENSIONS IN FEET AND INCHES UNLESS NOTED OTHERWISE. DO NOT SCALE.		3/16" = 1'-0"	2026-09-01
		SHEET	REV
A-101			B

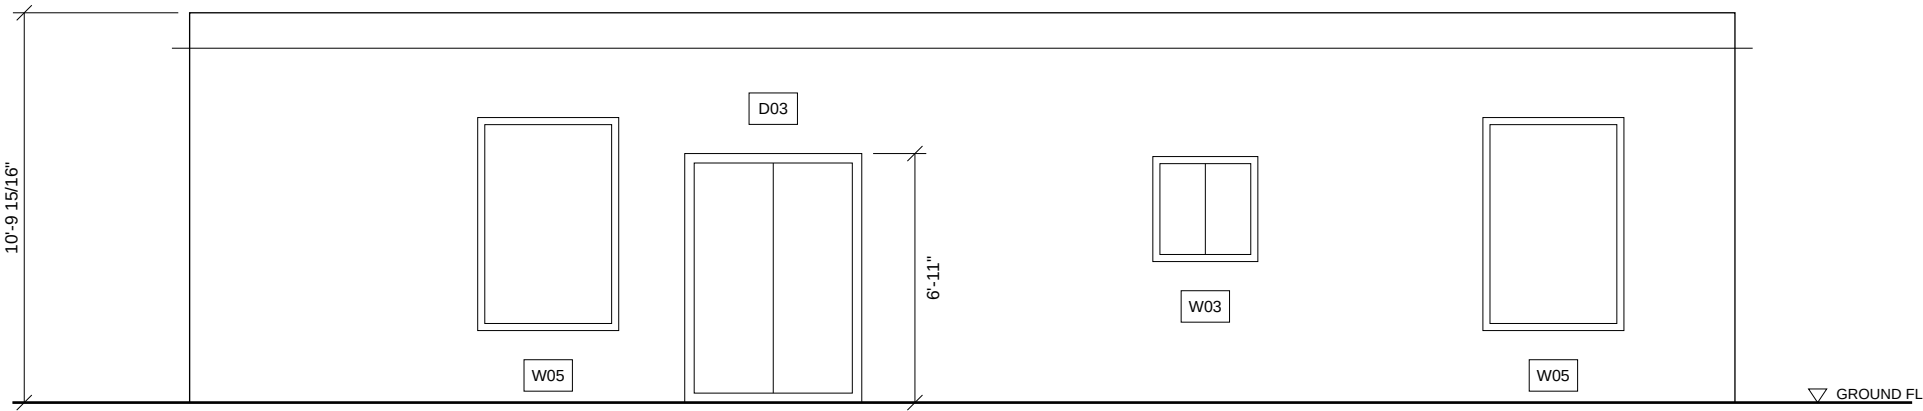

NORTH ELEVATION


SCALE 3/16" = 1'-0"

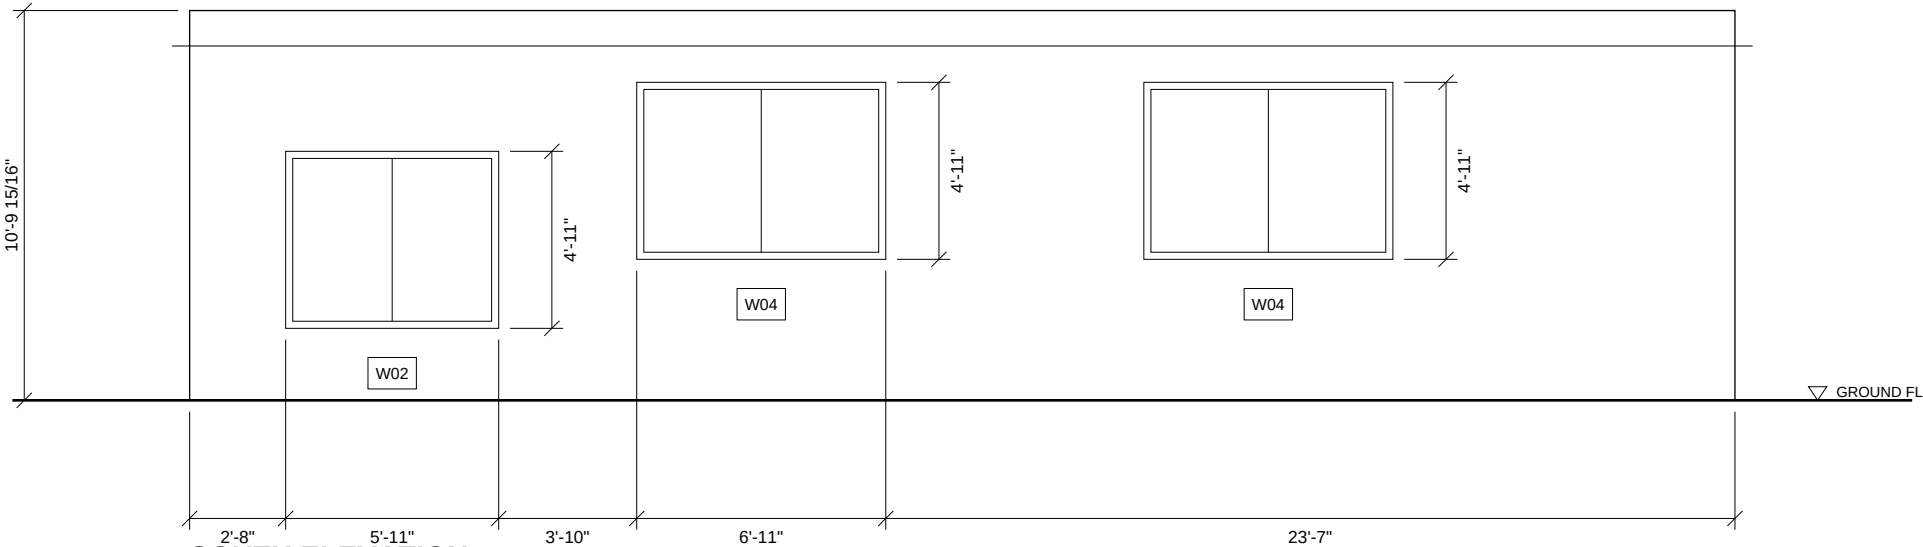

SOUTH ELEVATION


SCALE 3/16" = 1'-0"

STUDIO NORTH ARCHITECTS RESIDENTIAL BUILDING LOT 21, BENCHMARK AVENUE ALL DIMENSIONS IN FEET AND INCHES UNLESS NOTED OTHERWISE. DO NOT SCALE.	DRAWING TITLE NORTH & SOUTH ELEVATIONS	
	SCALE 3/16" = 1'-0"	DATE 2026-09-01
	SHEET A-201	REV B

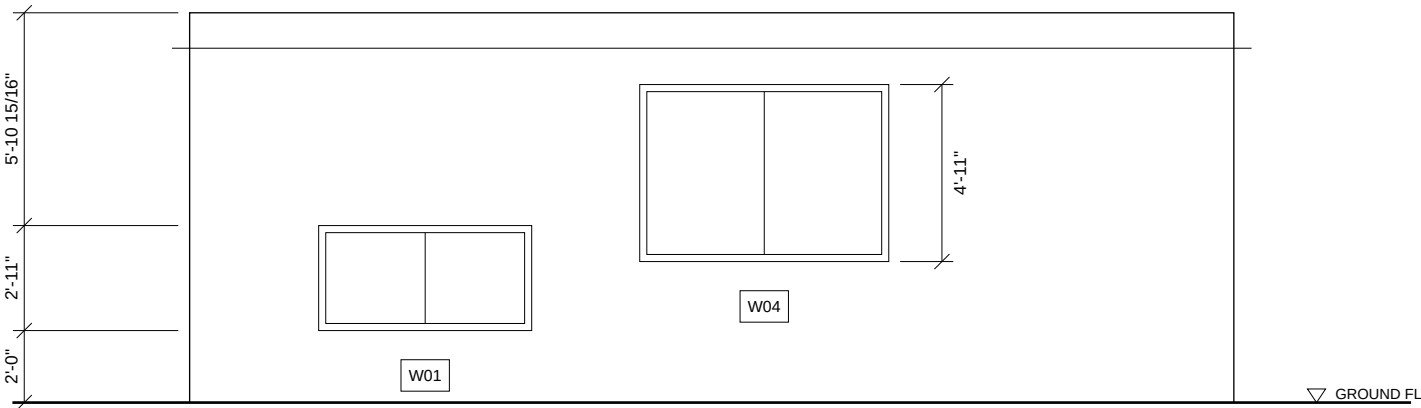

EAST ELEVATION

SCALE 3/16" = 1'-0"

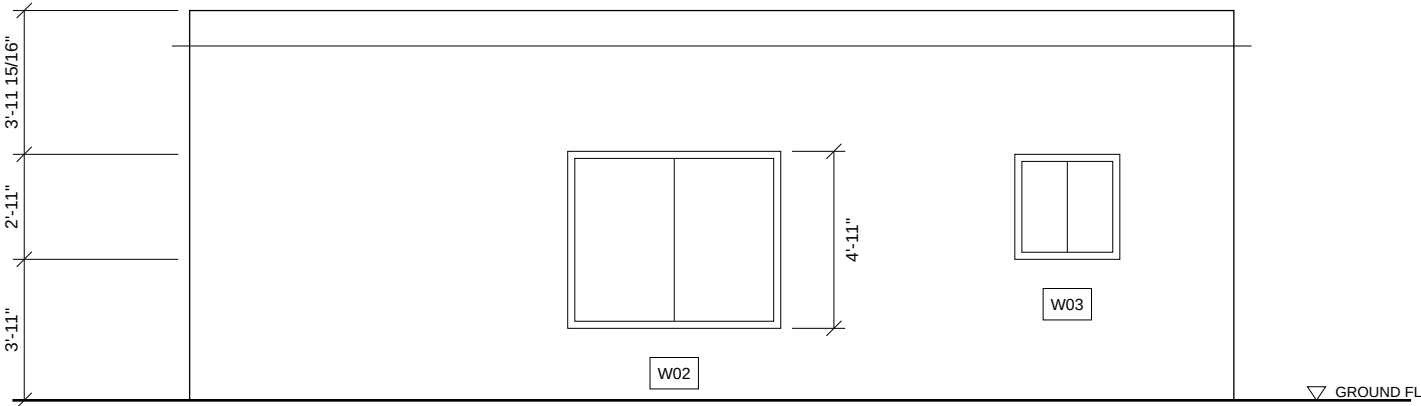

WEST ELEVATION

SCALE 3/16" = 1'-0"

STUDIO NORTH ARCHITECTS RESIDENTIAL BUILDING LOT 21, BENCHMARK AVENUE ALL DIMENSIONS IN FEET AND INCHES UNLESS NOTED OTHERWISE. DO NOT SCALE.	DRAWING TITLE EAST & WEST ELEVATIONS	
	SCALE 3/16" = 1'-0"	DATE 2026-09-01
	SHEET A-202	REV B

DOOR SCHEDULE

MARK	TYPE	WIDTH	HEIGHT	QTY	REMARKS
D02	HINGED	2'-8"	7'-8"	0	
D03	FRENCH DOORS	4'-11"	6'-11"	1	

WINDOW SCHEDULE

MARK	TYPE	WIDTH	HEIGHT	SILL	QTY	REMARKS
W01	SLIDING	5'-11"	2'-11"	2'-0"	1	
W02	SLIDING	5'-11"	4'-11"	2'-0"	1	
W03	SLIDING	2'-11"	2'-11"	3'-11"	2	
W04	AWNING	6'-11"	4'-11"	3'-11"	3	
W05	AWNING	3'-11"	5'-11"	2'-0"	2	

NOTE: ALL SIZES ARE NOMINAL STRUCTURAL OPENING SIZES.

STUDIO NORTH ARCHITECTS RESIDENTIAL BUILDING LOT 21, BENCHMARK AVENUE ALL DIMENSIONS IN FEET AND INCHES UNLESS NOTED OTHERWISE. DO NOT SCALE.	DRAWING TITLE DOOR & WINDOW SCHEDULES	
	SCALE NTS	DATE 2026-09-01
	SHEET A-601	REV B