



REFER TO DOOR AND WINDOW SCHEDULES ON A-601.
WINDOW TAGS SHOWN IN HEXAGONS, DOOR TAGS IN CIRCLES.

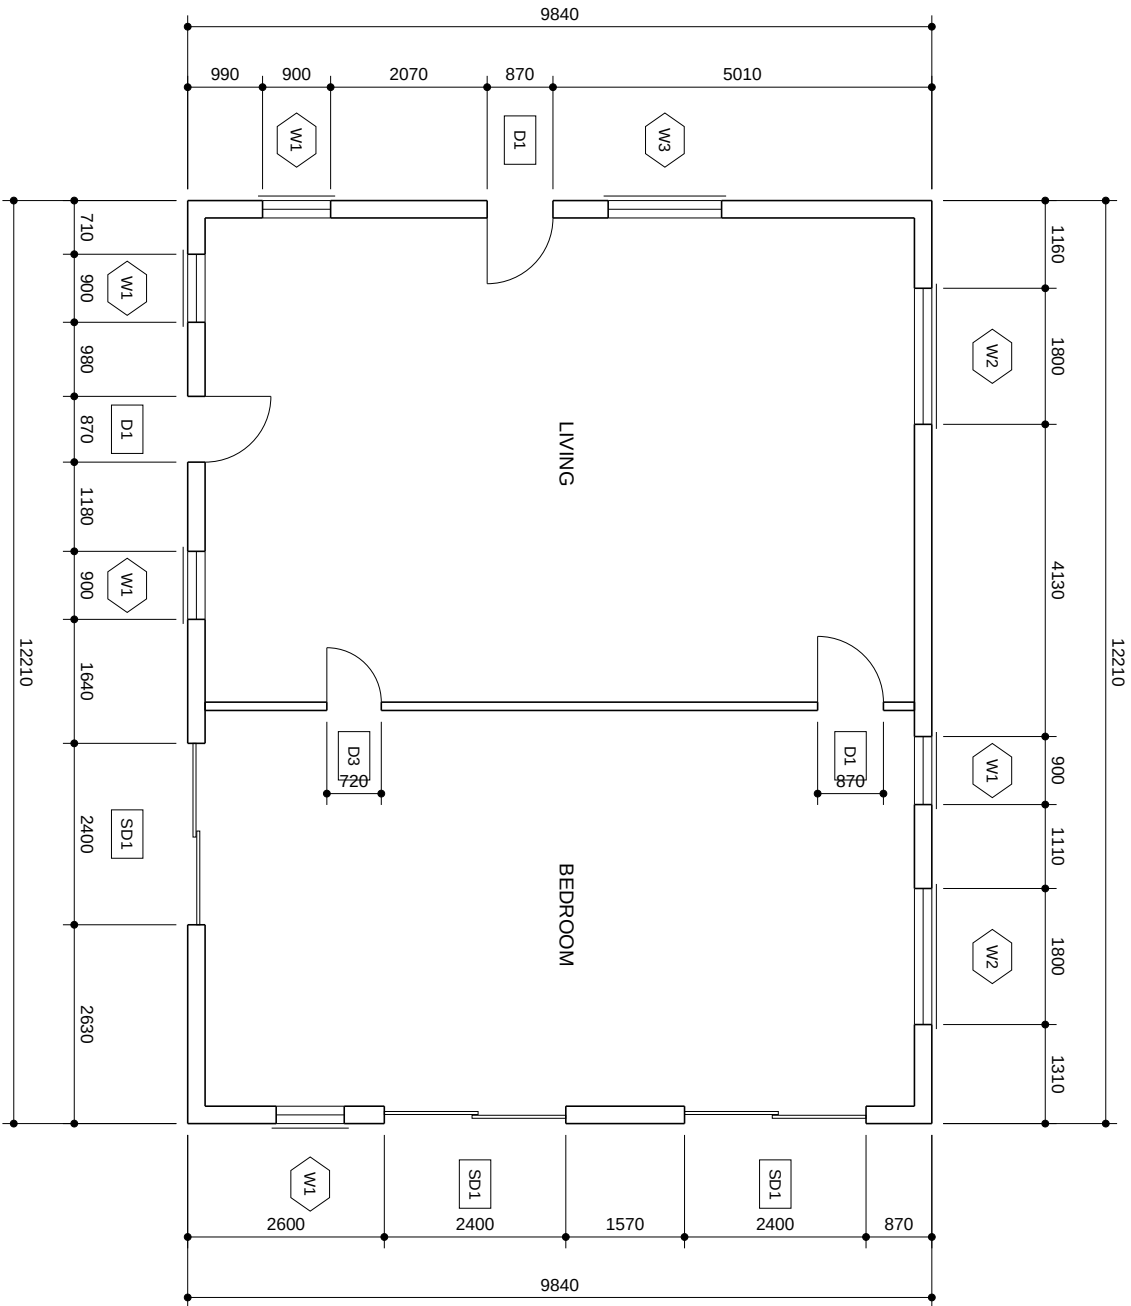


GROUND FLOOR PLAN
SCALE 1:100

STUDIO NORTH ARCHITECTS RESIDENTIAL BUILDING LOT 22, BENCHMARK AVENUE		GROUND FLOOR PLAN	
ALL DIMENSIONS IN MILLIMETRES UNLESS NOTED OTHERWISE. DO NOT SCALE		SCALE 1:100	DATE 2026-09-01
SHEET A-101		REV B	

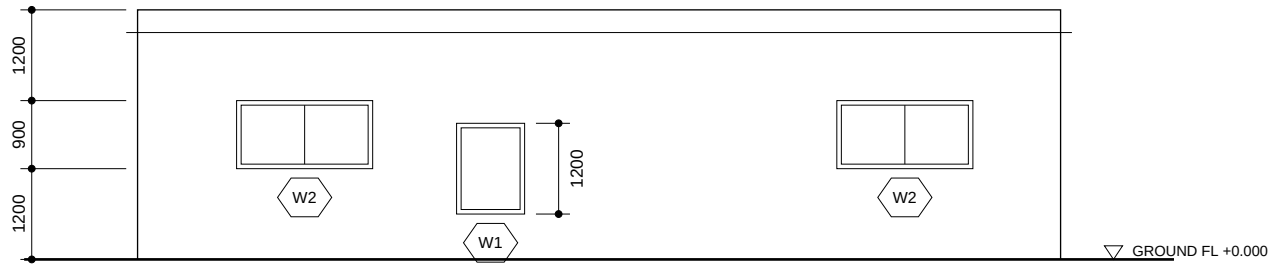

NORTH ELEVATION


SCALE 1:100

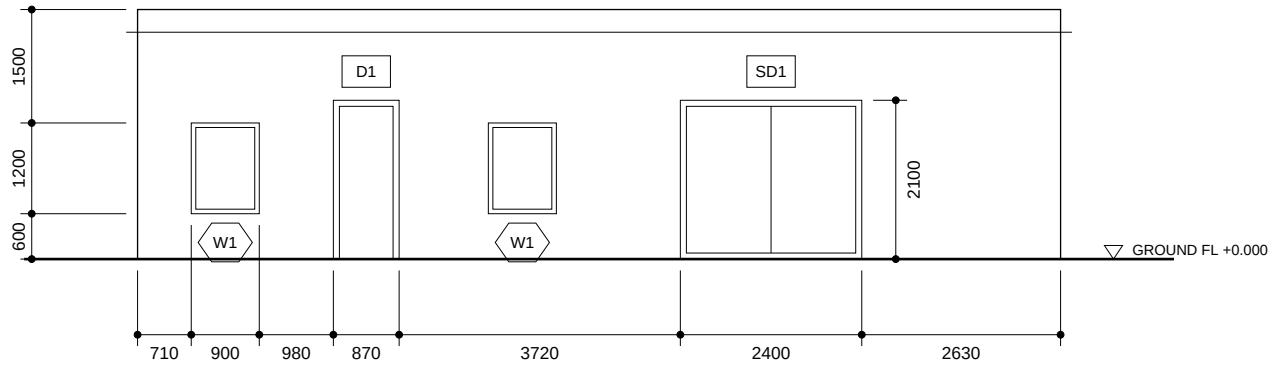

SOUTH ELEVATION


SCALE 1:100

STUDIO NORTH ARCHITECTS RESIDENTIAL BUILDING LOT 22, BENCHMARK AVENUE ALL DIMENSIONS IN MILLIMETRES UNLESS NOTED OTHERWISE. DO NOT SCALE.	DRAWING TITLE NORTH & SOUTH ELEVATIONS	
	SCALE 1:100	DATE 2026-09-01
	SHEET A-201	REV B

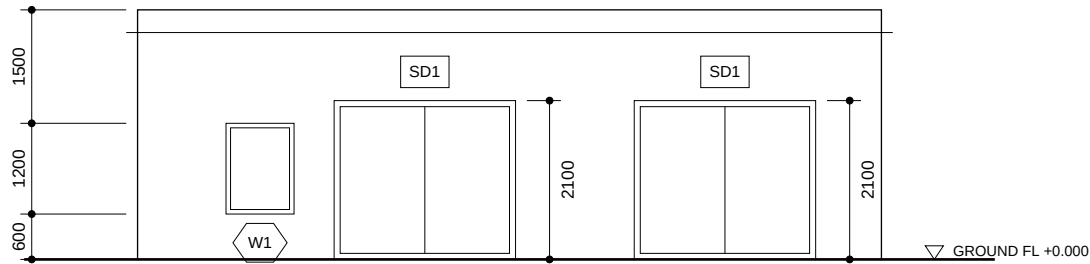

EAST ELEVATION

SCALE 1:100

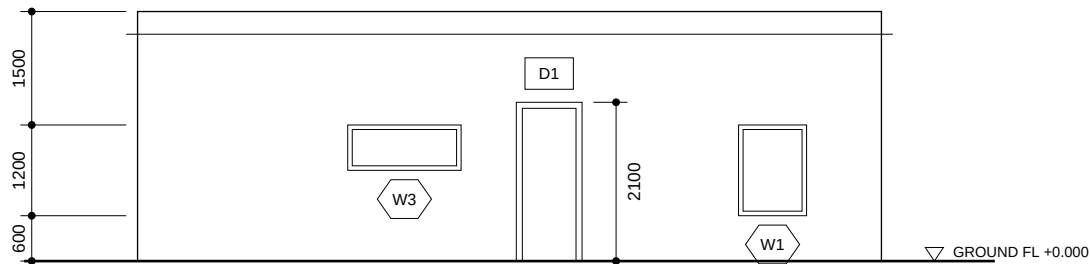

WEST ELEVATION

SCALE 1:100

STUDIO NORTH ARCHITECTS RESIDENTIAL BUILDING LOT 22, BENCHMARK AVENUE ALL DIMENSIONS IN MILLIMETRES UNLESS NOTED OTHERWISE, DO NOT SCALE.	DRAWING TITLE	
	EAST & WEST ELEVATIONS	
	SCALE	DATE
	1:100	2026-09-01
	SHEET	REV
	A-202	B

DOOR SCHEDULE

MARK	TYPE	WIDTH	HEIGHT	QTY	REMARKS
D1	HINGED	870	2100	3	
D2	HINGED	820	2040	0	
D3	HINGED	720	2340	1	
SD1	SLIDING DOOR	2400	2100	3	

WINDOW SCHEDULE

MARK	TYPE	WIDTH	HEIGHT	SILL	QTY	REMARKS
W1	AWNING	900	1200	600	5	
W2	AWNING	1800	900	1200	2	
W3	AWNING	1500	600	1200	1	

NOTE: ALL SIZES ARE NOMINAL STRUCTURAL OPENING SIZES.

STUDIO NORTH ARCHITECTS RESIDENTIAL BUILDING LOT 22, BENCHMARK AVENUE ALL DIMENSIONS IN MILLIMETRES UNLESS NOTED OTHERWISE. DO NOT SCALE.	DRAWING TITLE DOOR & WINDOW SCHEDULES	
	SCALE NTS	DATE 2026-09-01
	SHEET A-601	REV B