

RESIDENTIAL BUILDING

LOT 23, BENCHMARK AVENUE


CONSTRUCTION ISSUE

DRAWING LIST

SHEET	TITLE
A-101	GROUND FLOOR PLAN
A-201	NORTH & SOUTH ELEVATIONS
A-202	EAST & WEST ELEVATIONS
A-601	DOOR & WINDOW SCHEDULES

STUDIO NORTH ARCHITECTS RESIDENTIAL BUILDING LOT 23, BENCHMARK AVENUE ALL DIMENSIONS IN MILLIMETRES UNLESS NOTED OTHERWISE, DO NOT SCALE.	DRAWING TITLE COVER SHEET	
	SCALE NTS	DATE 2026-09-01
	SHEET A-000	REV B


REFER TO DOOR AND WINDOW SCHEDULES ON A-601.
WINDOW TAGS SHOWN IN HEXAGONS, DOOR TAGS IN CIRCLES.

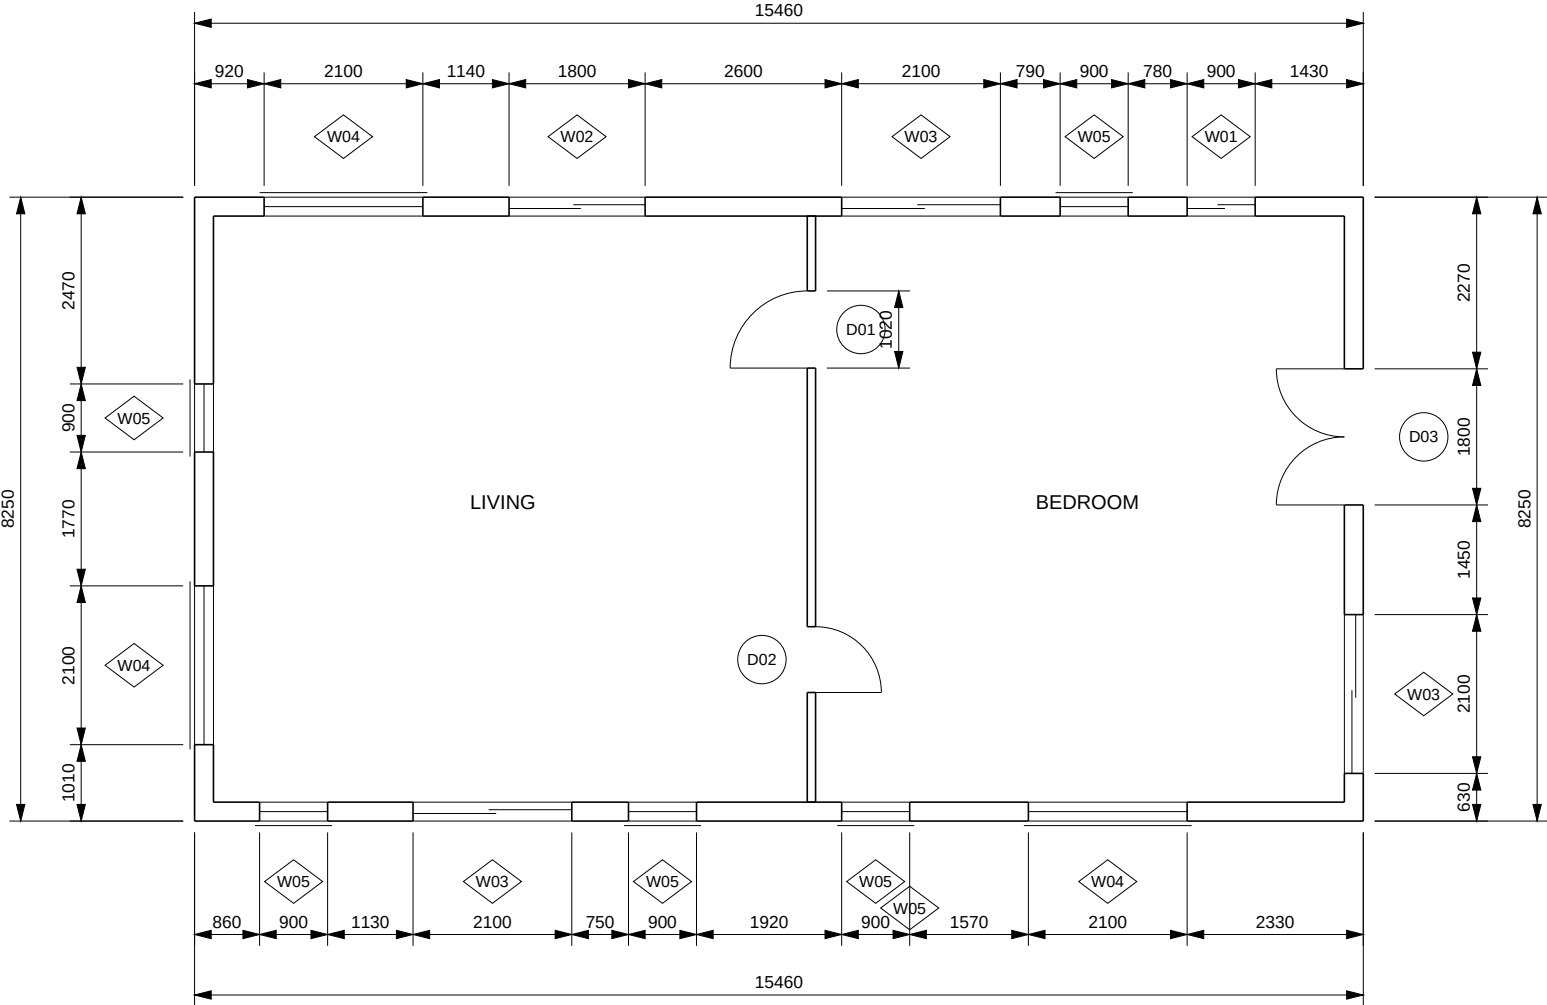

GROUND FLOOR PLAN


SCALE 1:100

STUDIO NORTH ARCHITECTS RESIDENTIAL BUILDING LOT 23, BENCHMARK AVENUE ALL DIMENSIONS IN MILLIMETRES UNLESS NOTED OTHERWISE, DO NOT SCALE.	DRAWING TITLE GROUND FLOOR PLAN	
	SCALE 1:100	DATE 2026-09-01
	SHEET A-101	REV B

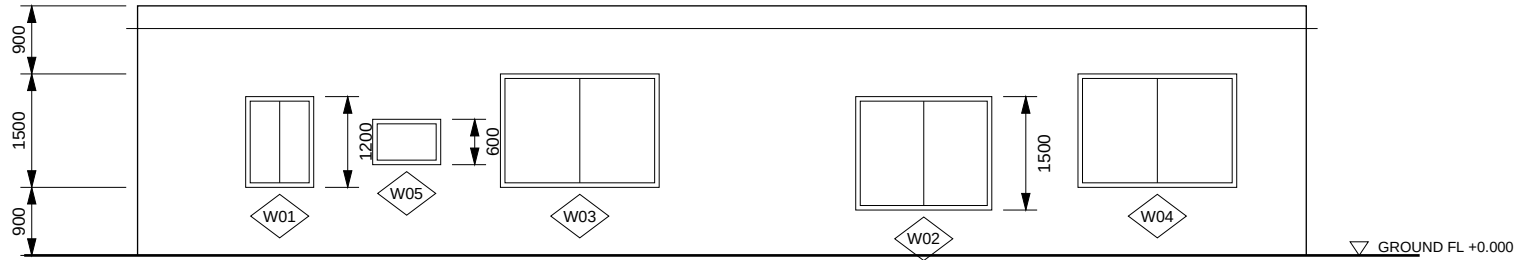

NORTH ELEVATION


SCALE 1:100

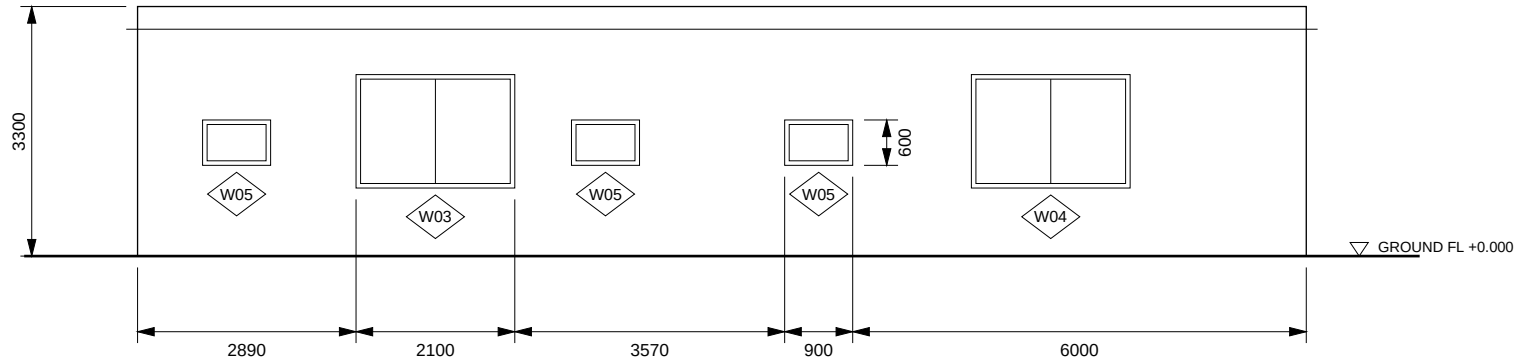

SOUTH ELEVATION


SCALE 1:100

STUDIO NORTH ARCHITECTS RESIDENTIAL BUILDING LOT 23, BENCHMARK AVENUE ALL DIMENSIONS IN MILLIMETRES UNLESS NOTED OTHERWISE. DO NOT SCALE.	DRAWING TITLE	
	NORTH & SOUTH ELEVATIONS	
	SCALE	DATE
	1:100	2026-09-01
	SHEET	REV
	A-201	B

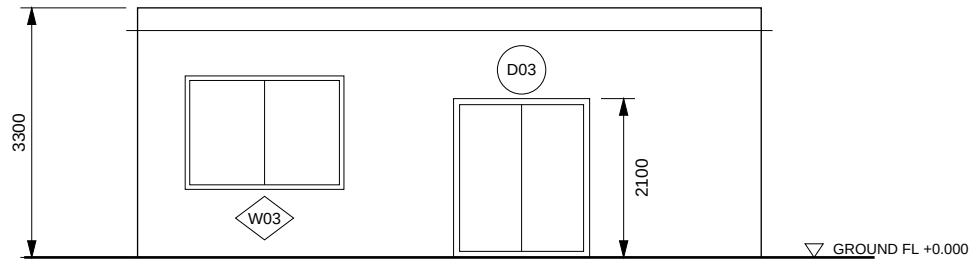

EAST ELEVATION

SCALE 1:100

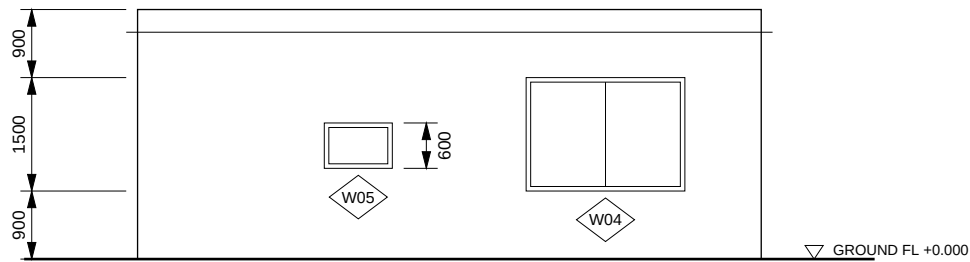

WEST ELEVATION

SCALE 1:100

STUDIO NORTH ARCHITECTS

RESIDENTIAL BUILDING

LOT 23, BENCHMARK AVENUE

ALL DIMENSIONS IN MILLIMETRES UNLESS NOTED
OTHERWISE, DO NOT SCALE.

DRAWING TITLE

EAST & WEST ELEVATIONS

SCALE

1:100

SHEET

A-202

DATE

2026-09-01

REV

B

DOOR SCHEDULE

MARK	TYPE	WIDTH	HEIGHT	QTY	REMARKS
D01	HINGED	1020	2040	1	
D02	HINGED	870	2340	1	
D03	FRENCH DOORS	1800	2100	1	

WINDOW SCHEDULE

MARK	TYPE	WIDTH	HEIGHT	SILL	QTY	REMARKS
W01	SLIDING	900	1200	900	1	
W02	SLIDING	1800	1800	600	1	
W03	SLIDING	2100	1500	900	3	
W04	AWNING	2100	1500	900	3	
W05	AWNING	900	600	1200	5	

NOTE: ALL SIZES ARE NOMINAL STRUCTURAL OPENING SIZES.

STUDIO NORTH ARCHITECTS RESIDENTIAL BUILDING LOT 23, BENCHMARK AVENUE ALL DIMENSIONS IN MILLIMETRES UNLESS NOTED OTHERWISE. DO NOT SCALE.	DRAWING TITLE DOOR & WINDOW SCHEDULES	
	SCALE NTS	DATE 2026-09-01
	SHEET A-601	REV B