



REFER TO DOOR AND WINDOW SCHEDULES ON A-601.
WINDOW TAGS SHOWN IN HEXAGONS, DOOR TAGS IN CIRCLES.

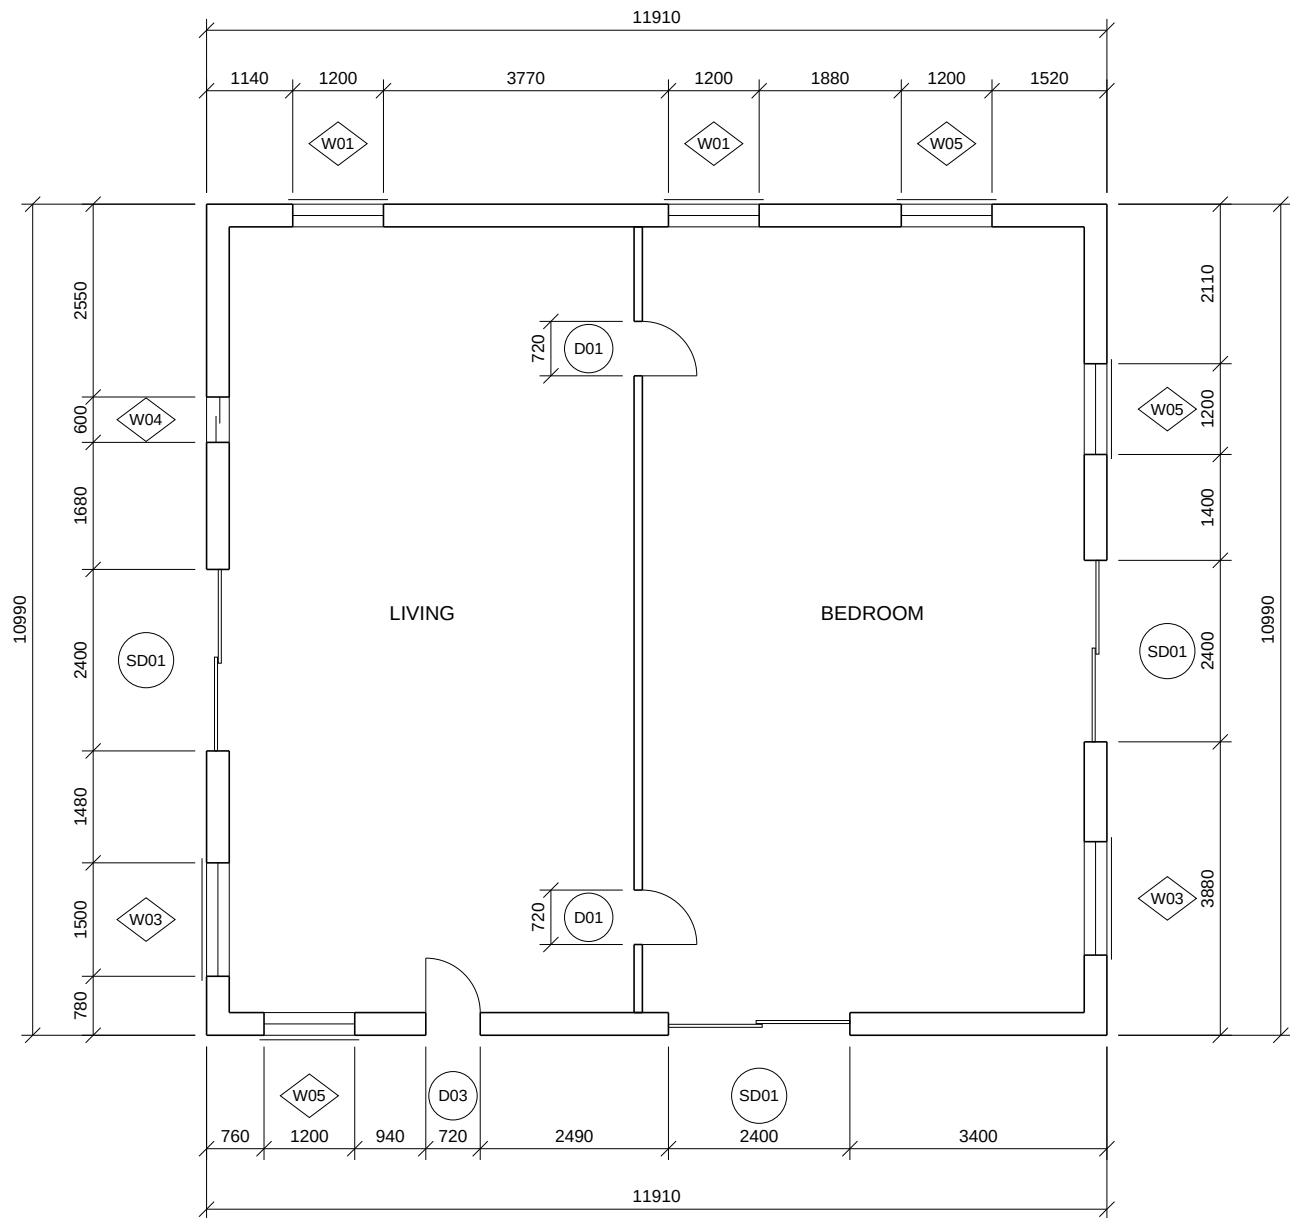

GROUND FLOOR PLAN


SCALE 1:100

STUDIO NORTH ARCHITECTS RESIDENTIAL BUILDING LOT 24, BENCHMARK AVENUE ALL DIMENSIONS IN MILLIMETRES UNLESS NOTED OTHERWISE, DO NOT SCALE.	DRAWING TITLE	
	GROUND FLOOR PLAN	
	SCALE	DATE
	1:100	2026-09-01
	SHEET	REV
	A-101	B

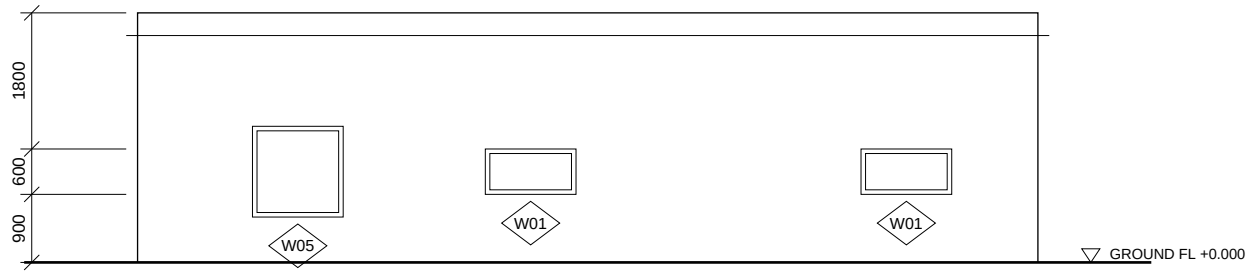

NORTH ELEVATION

SCALE 1:100

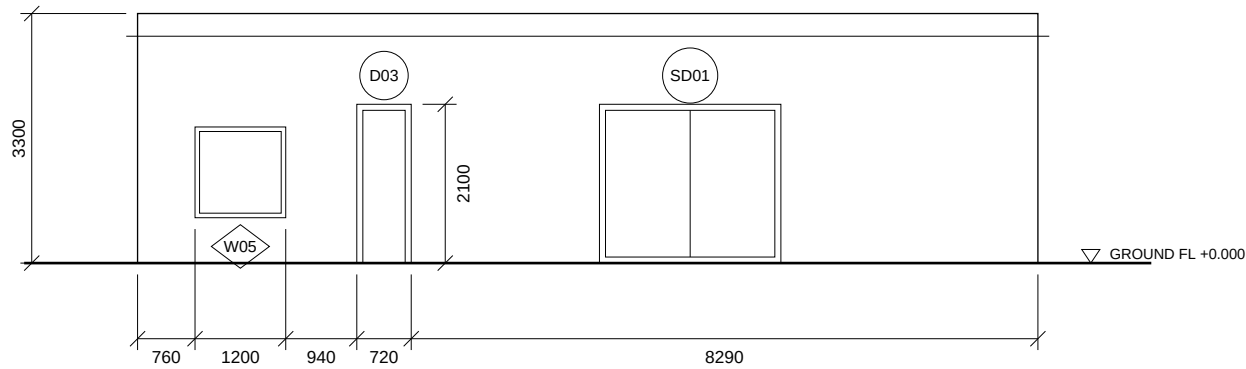

SOUTH ELEVATION

SCALE 1:100

STUDIO NORTH ARCHITECTS

RESIDENTIAL BUILDING

LOT 24, BENCHMARK AVENUE

ALL DIMENSIONS IN MILLIMETRES UNLESS NOTED
OTHERWISE. DO NOT SCALE.

DRAWING TITLE

NORTH & SOUTH ELEVATIONS

SCALE

1:100

SHEET


A-201

DATE

2026-09-01


REV

B

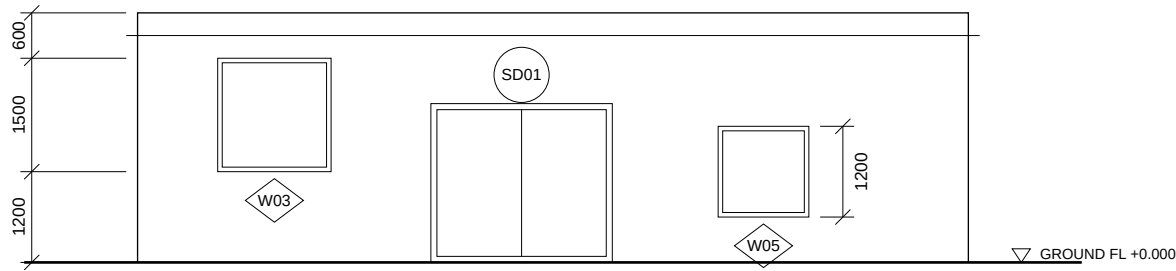

EAST ELEVATION

SCALE 1:100

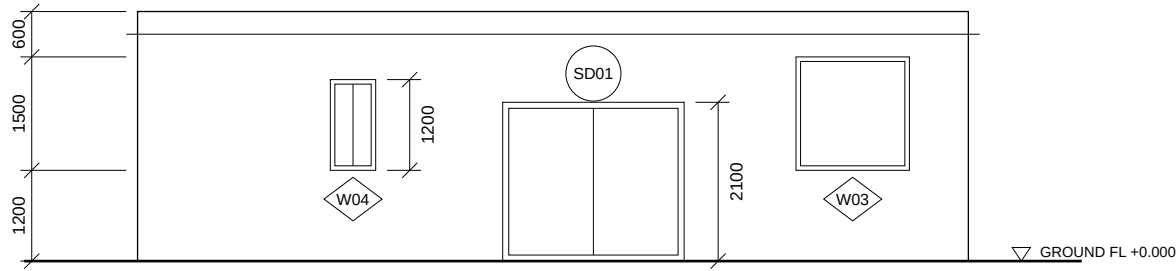

WEST ELEVATION

SCALE 1:100

STUDIO NORTH ARCHITECTS RESIDENTIAL BUILDING LOT 24, BENCHMARK AVENUE ALL DIMENSIONS IN MILLIMETRES UNLESS NOTED OTHERWISE, DO NOT SCALE.	DRAWING TITLE	
	EAST & WEST ELEVATIONS	
	SCALE	DATE
	1:100	2026-09-01
	SHEET	REV
	A-202	B

DOOR SCHEDULE

MARK	TYPE	WIDTH	HEIGHT	QTY	REMARKS
D01	HINGED	720	2040	2	
D02	HINGED	870	2100	0	
D03	HINGED	720	2100	1	
SD01	SLIDING DOOR	2400	2100	3	

WINDOW SCHEDULE

MARK	TYPE	WIDTH	HEIGHT	SILL	QTY	REMARKS
W01	AWNING	1200	600	900	2	
W02	AWNING	2100	600	600	0	
W03	AWNING	1500	1500	1200	2	
W04	SLIDING	600	1200	1200	1	
W05	AWNING	1200	1200	600	3	

NOTE: ALL SIZES ARE NOMINAL STRUCTURAL OPENING SIZES.

STUDIO NORTH ARCHITECTS RESIDENTIAL BUILDING LOT 24, BENCHMARK AVENUE ALL DIMENSIONS IN MILLIMETRES UNLESS NOTED OTHERWISE. DO NOT SCALE.	DRAWING TITLE DOOR & WINDOW SCHEDULES	
	SCALE NTS	DATE 2026-09-01
	SHEET A-601	REV B