


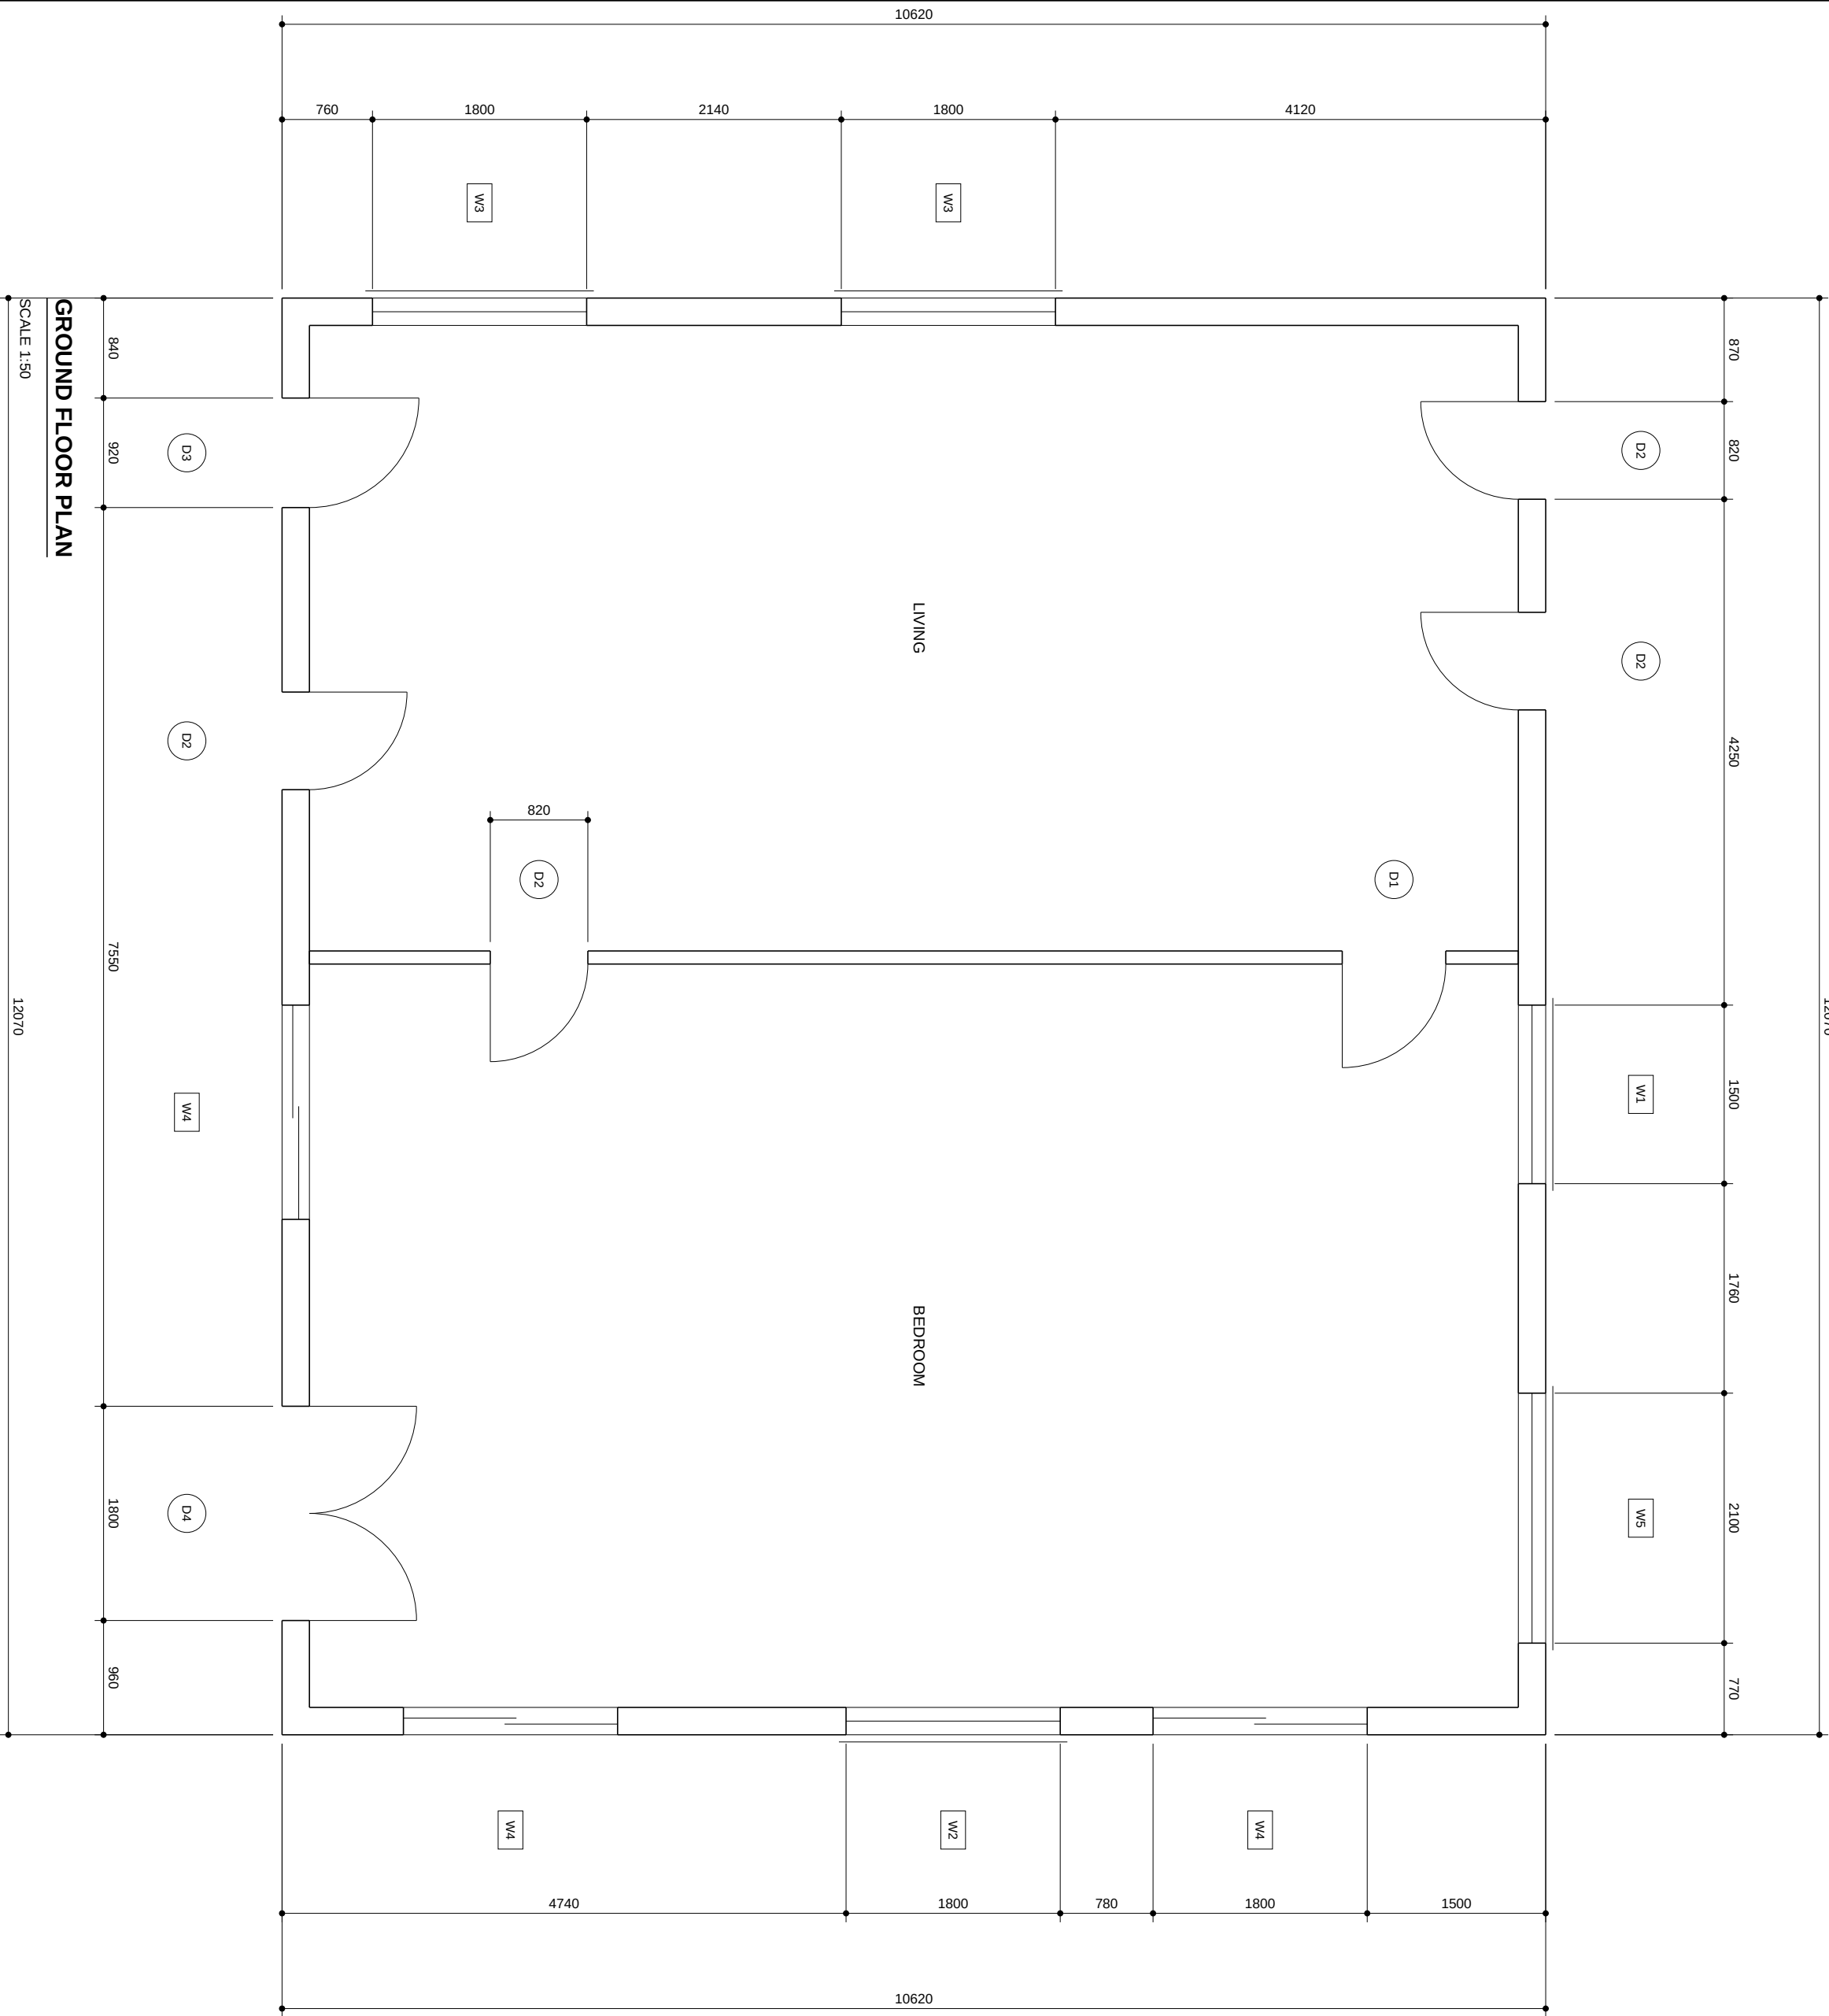

REFER TO DOOR AND WINDOW SCHEDULES ON A-601.
WINDOW TAGS SHOWN IN HEXAGONS, DOOR TAGS IN CIRCLES.

STUDIO NORTH ARCHITECTS		DRAWING TITLE	
RESIDENTIAL BUILDING		GROUND FLOOR PLAN	
LOT 25, BENCHMARK AVENUE		SCALE	DATE
ALL DIMENSIONS IN MILLIMETRES, UNLESS NOTED OTHERWISE, DO NOT SCALE.		1:50	2026-09-01
		SHEET	REV
A-101			B

DOOR SCHEDULE

MARK	TYPE	WIDTH	HEIGHT	QTY	REMARKS
D1	HINGED	870	2040	1	
D2	HINGED	820	2340	4	
D3	HINGED	920	2040	1	
SD1	SLIDING DOOR	2400	2100	0	
D4	FRENCH DOORS	1800	2100	1	

WINDOW SCHEDULE

MARK	TYPE	WIDTH	HEIGHT	SILL	QTY	REMARKS
W2	AWNING	1800	900	1200	1	
W4	SLIDING	1800	1500	1200	3	
W5	AWNING	2100	600	1200	1	

NOTE: ALL SIZES ARE NOMINAL STRUCTURAL OPENING SIZES.

STUDIO NORTH ARCHITECTS RESIDENTIAL BUILDING LOT 25, BENCHMARK AVENUE ALL DIMENSIONS IN MILLIMETRES UNLESS NOTED OTHERWISE. DO NOT SCALE.	DRAWING TITLE DOOR & WINDOW SCHEDULES	
	SCALE NTS	DATE 2026-09-01
	SHEET A-601	REV B