



REFER TO DOOR AND WINDOW SCHEDULES ON A-601.
WINDOW TAGS SHOWN IN HEXAGONS, DOOR TAGS IN CIRCLES.

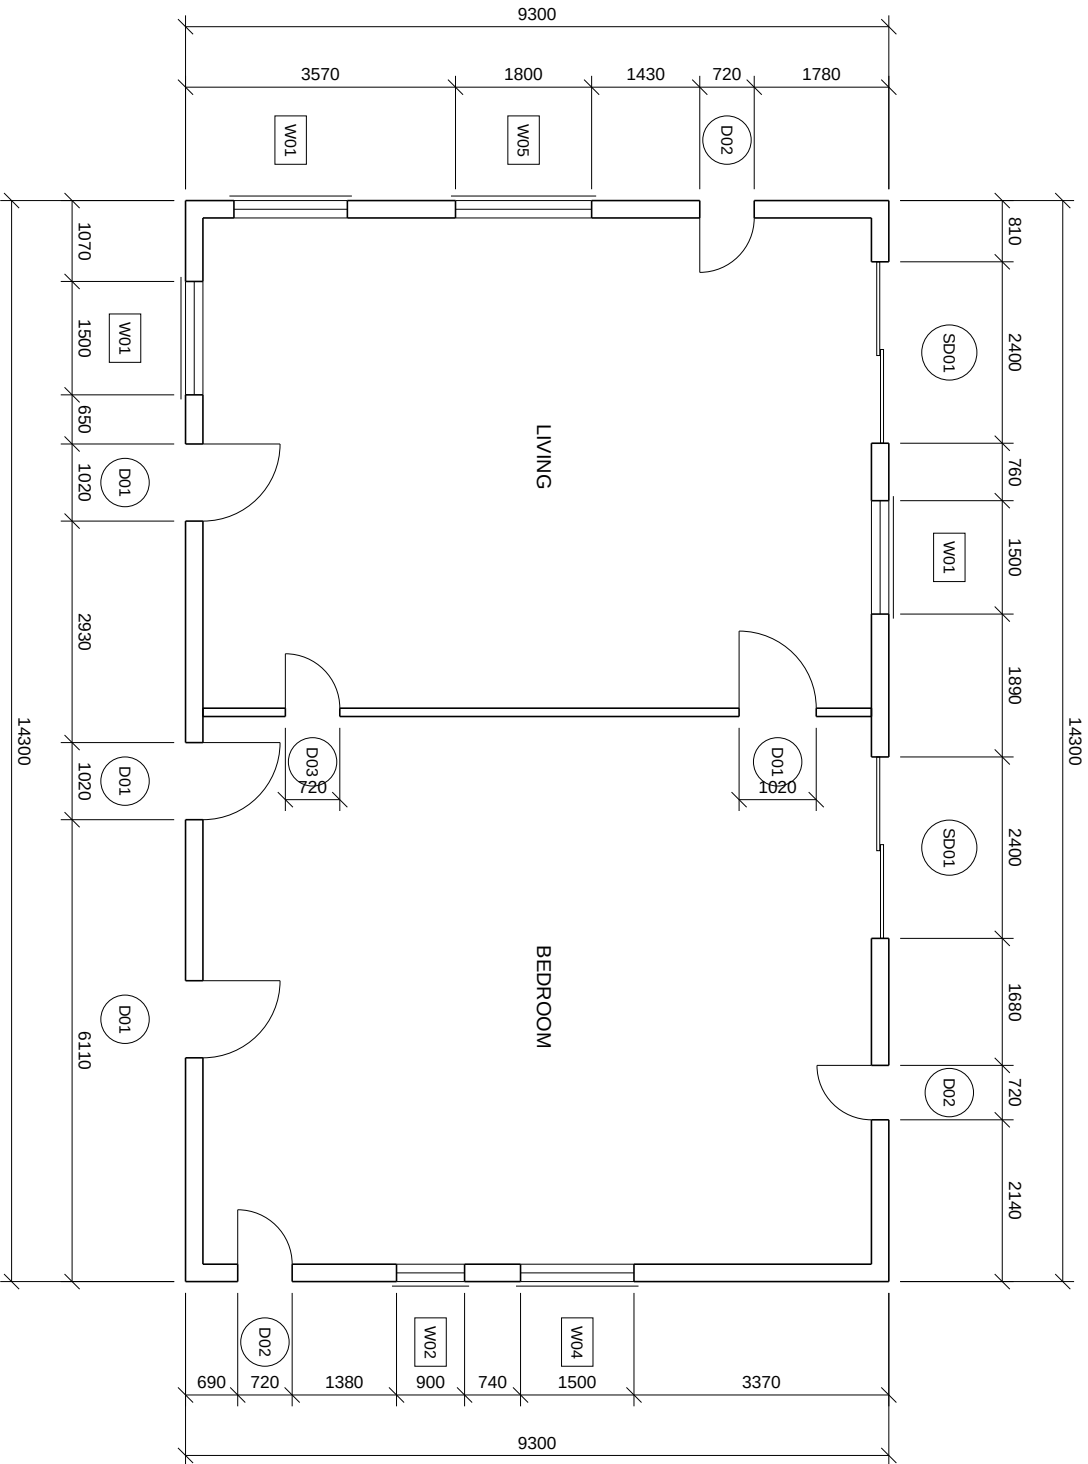

GROUND FLOOR PLAN


SCALE 1:100

STUDIO NORTH ARCHITECTS		DRAWING TITLE	
RESIDENTIAL BUILDING		GROUND FLOOR PLAN	
LOT 26, BENCHMARK AVENUE		SCALE	DATE
ALL DIMENSIONS IN MILLIMETRES UNLESS NOTED OTHERWISE. DO NOT SCALE		1:100	2026-09-01
		SHEET	REV
A-101			B

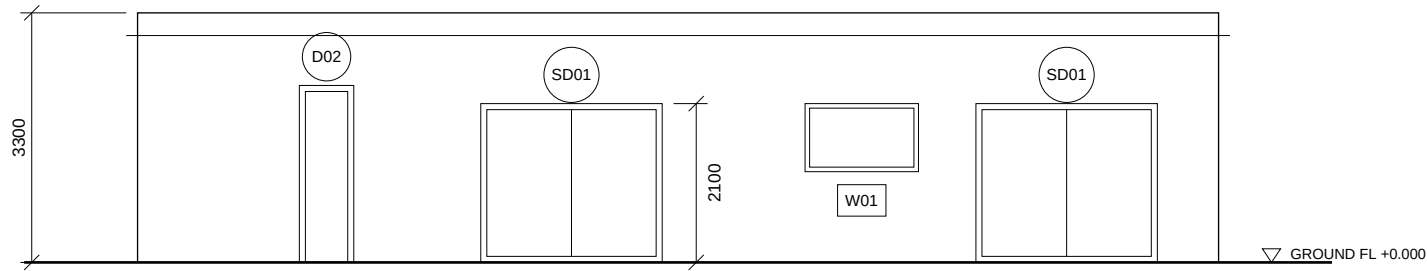

NORTH ELEVATION

SCALE 1:100

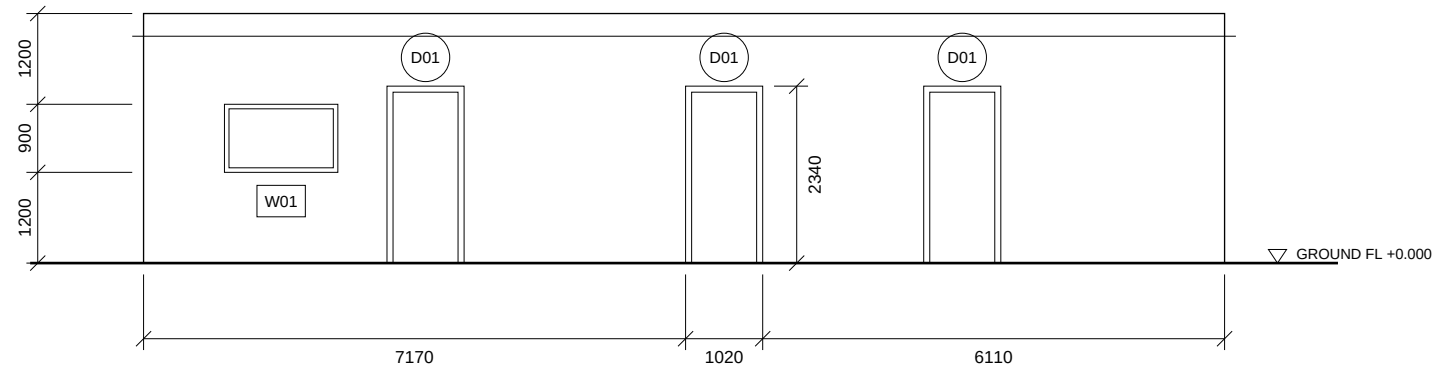

SOUTH ELEVATION

SCALE 1:100

STUDIO NORTH ARCHITECTS

RESIDENTIAL BUILDING

LOT 26, BENCHMARK AVENUE

ALL DIMENSIONS IN MILLIMETRES UNLESS NOTED
OTHERWISE. DO NOT SCALE.

DRAWING TITLE

NORTH & SOUTH ELEVATIONS

SCALE

1:100

SHEET


A-201

DATE

2026-09-01


REV

B

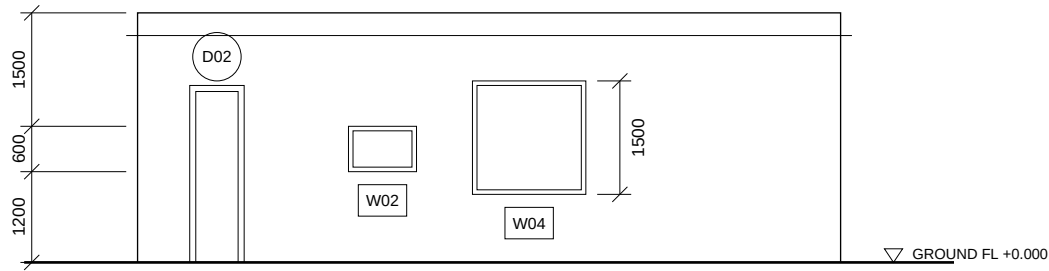

EAST ELEVATION

SCALE 1:100

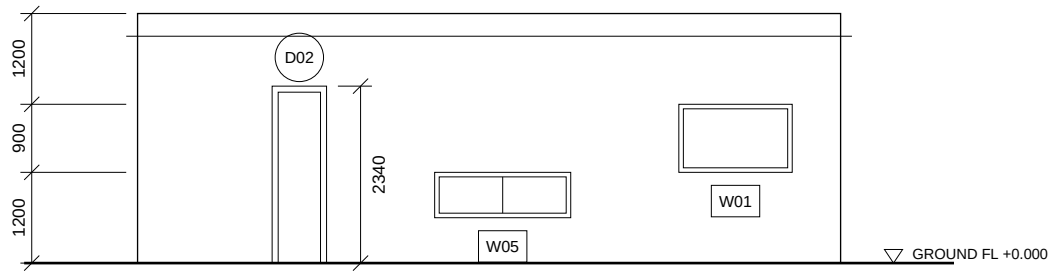

WEST ELEVATION

SCALE 1:100

STUDIO NORTH ARCHITECTS

RESIDENTIAL BUILDING

LOT 26, BENCHMARK AVENUE

ALL DIMENSIONS IN MILLIMETRES UNLESS NOTED
OTHERWISE, DO NOT SCALE.

DRAWING TITLE

EAST & WEST ELEVATIONS

SCALE

1:100

SHEET

A-202

DATE

2026-09-01

REV

B

DOOR SCHEDULE

MARK	TYPE	WIDTH	HEIGHT	QTY	REMARKS
D02	HINGED	720	2340	3	
D03	HINGED	720	2340	1	
SD01	SLIDING DOOR	2400	2100	2	

WINDOW SCHEDULE

MARK	TYPE	WIDTH	HEIGHT	SILL	QTY	REMARKS
W01	AWNING	1500	900	1200	3	
W02	AWNING	900	600	1200	1	
W03	AWNING	900	900	600	0	
W04	AWNING	1500	1500	900	1	
W05	AWNING	1800	600	600	1	

NOTE: ALL SIZES ARE NOMINAL STRUCTURAL OPENING SIZES.

STUDIO NORTH ARCHITECTS RESIDENTIAL BUILDING LOT 26, BENCHMARK AVENUE ALL DIMENSIONS IN MILLIMETRES UNLESS NOTED OTHERWISE. DO NOT SCALE.	DRAWING TITLE DOOR & WINDOW SCHEDULES	
	SCALE NTS	DATE 2026-09-01
	SHEET A-601	REV B