

RESIDENTIAL BUILDING


LOT 27, BENCHMARK AVENUE

CONSTRUCTION ISSUE

DRAWING LIST


SHEET	TITLE
A-101	GROUND FLOOR PLAN
A-201	NORTH & SOUTH ELEVATIONS
A-202	EAST & WEST ELEVATIONS
A-601	DOOR & WINDOW SCHEDULES

STUDIO NORTH ARCHITECTS RESIDENTIAL BUILDING LOT 27, BENCHMARK AVENUE ALL DIMENSIONS IN MILLIMETRES UNLESS NOTED OTHERWISE, DO NOT SCALE.	DRAWING TITLE COVER SHEET	
	SCALE NTS	DATE 2026-09-01
	SHEET A-000	REV B

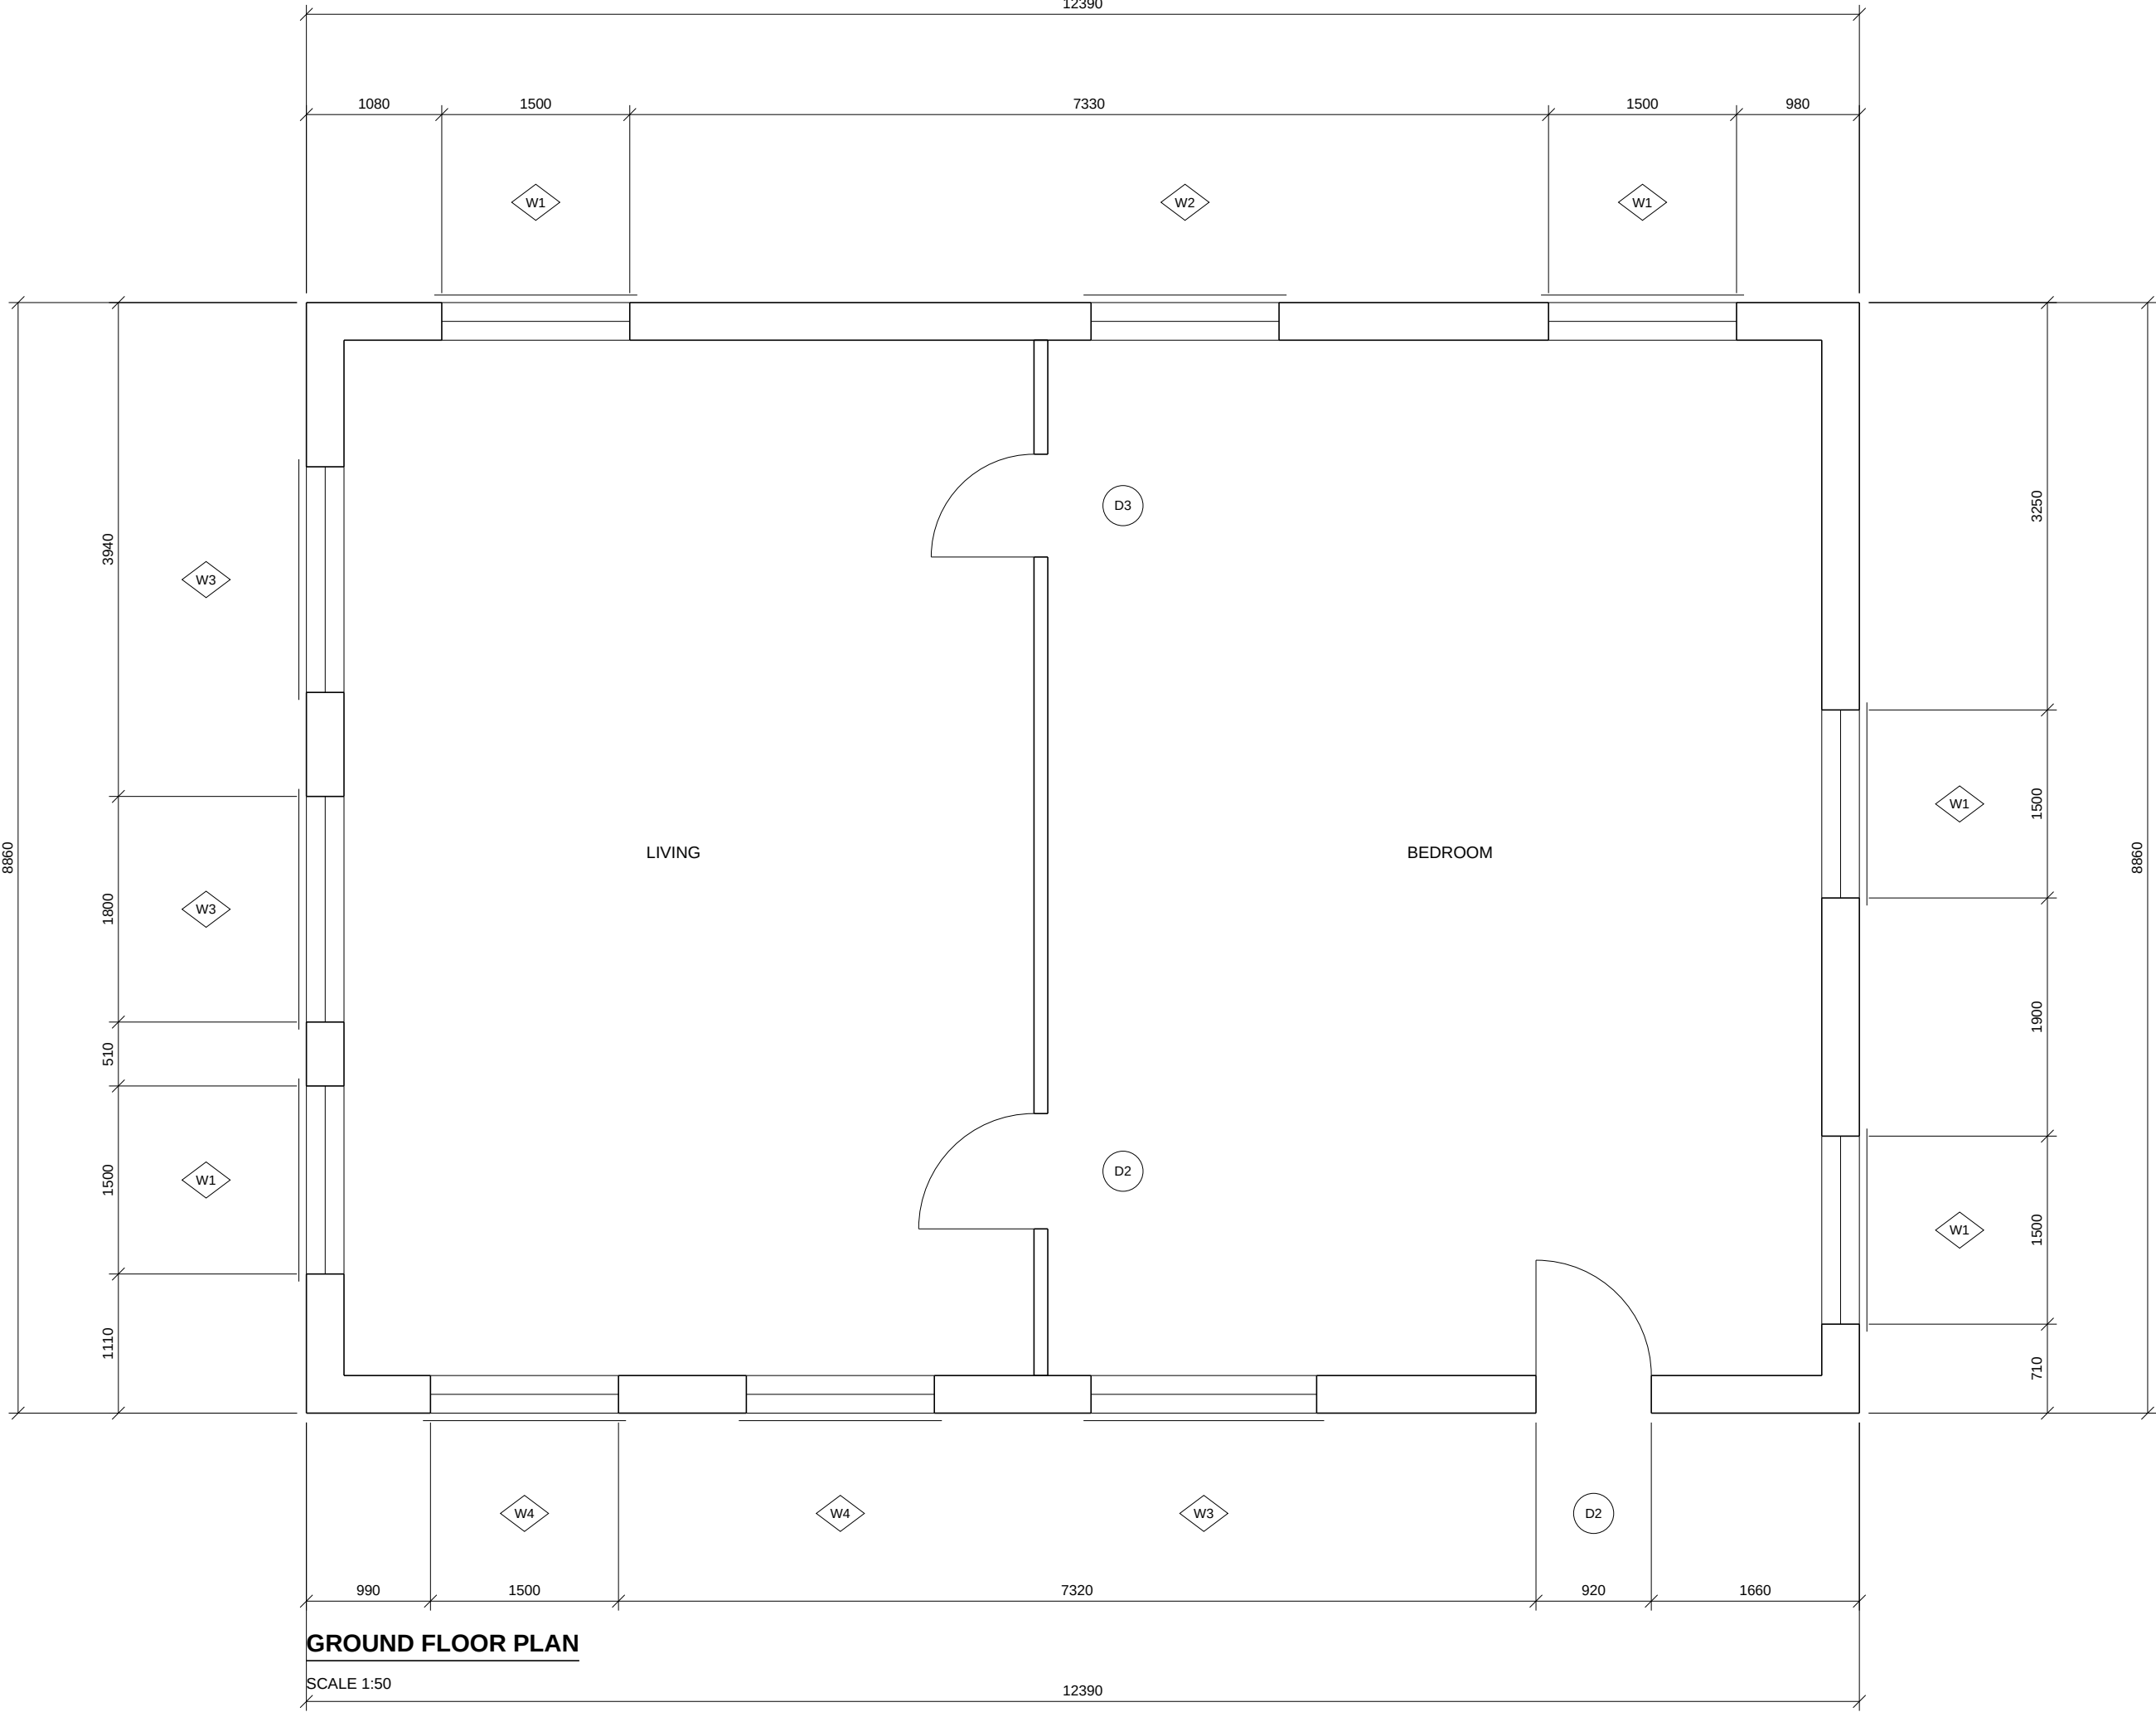


REFER TO DOOR AND WINDOW SCHEDULES ON A-601.
WINDOW TAGS SHOWN IN HEXAGONS, DOOR TAGS IN CIRCLES.

STUDIO NORTH ARCHITECTS RESIDENTIAL BUILDING LOT 27, BENCHMARK AVENUE ALL DIMENSIONS IN MILLIMETRES UNLESS NOTED OTHERWISE, DO NOT SCALE.	DRAWING TITLE	
	GROUND FLOOR PLAN	
	SCALE	DATE
	1:50	2026-09-01
	SHEET	REV
	A-101	B

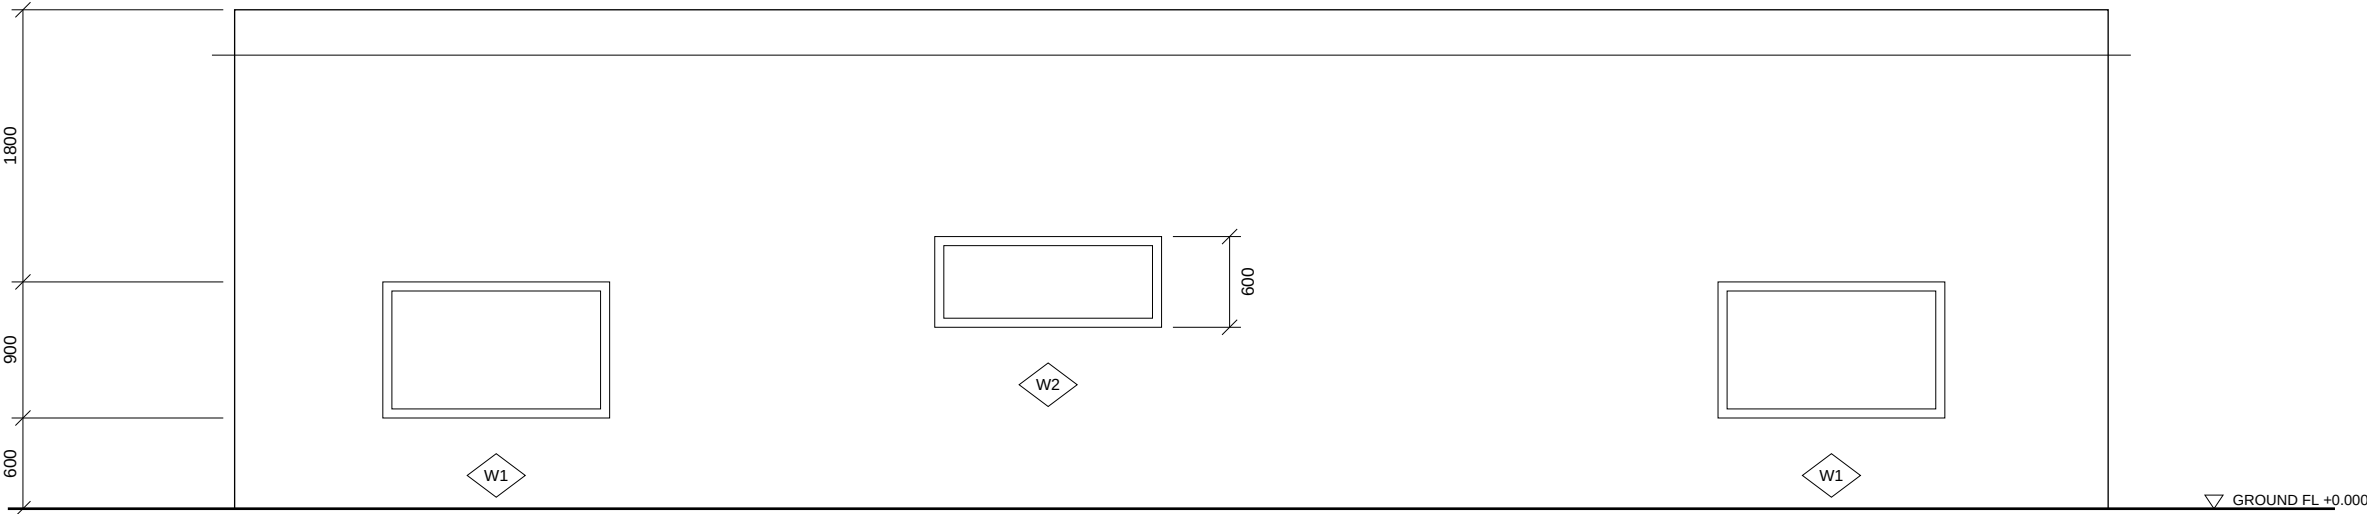

NORTH ELEVATION

SCALE 1:50

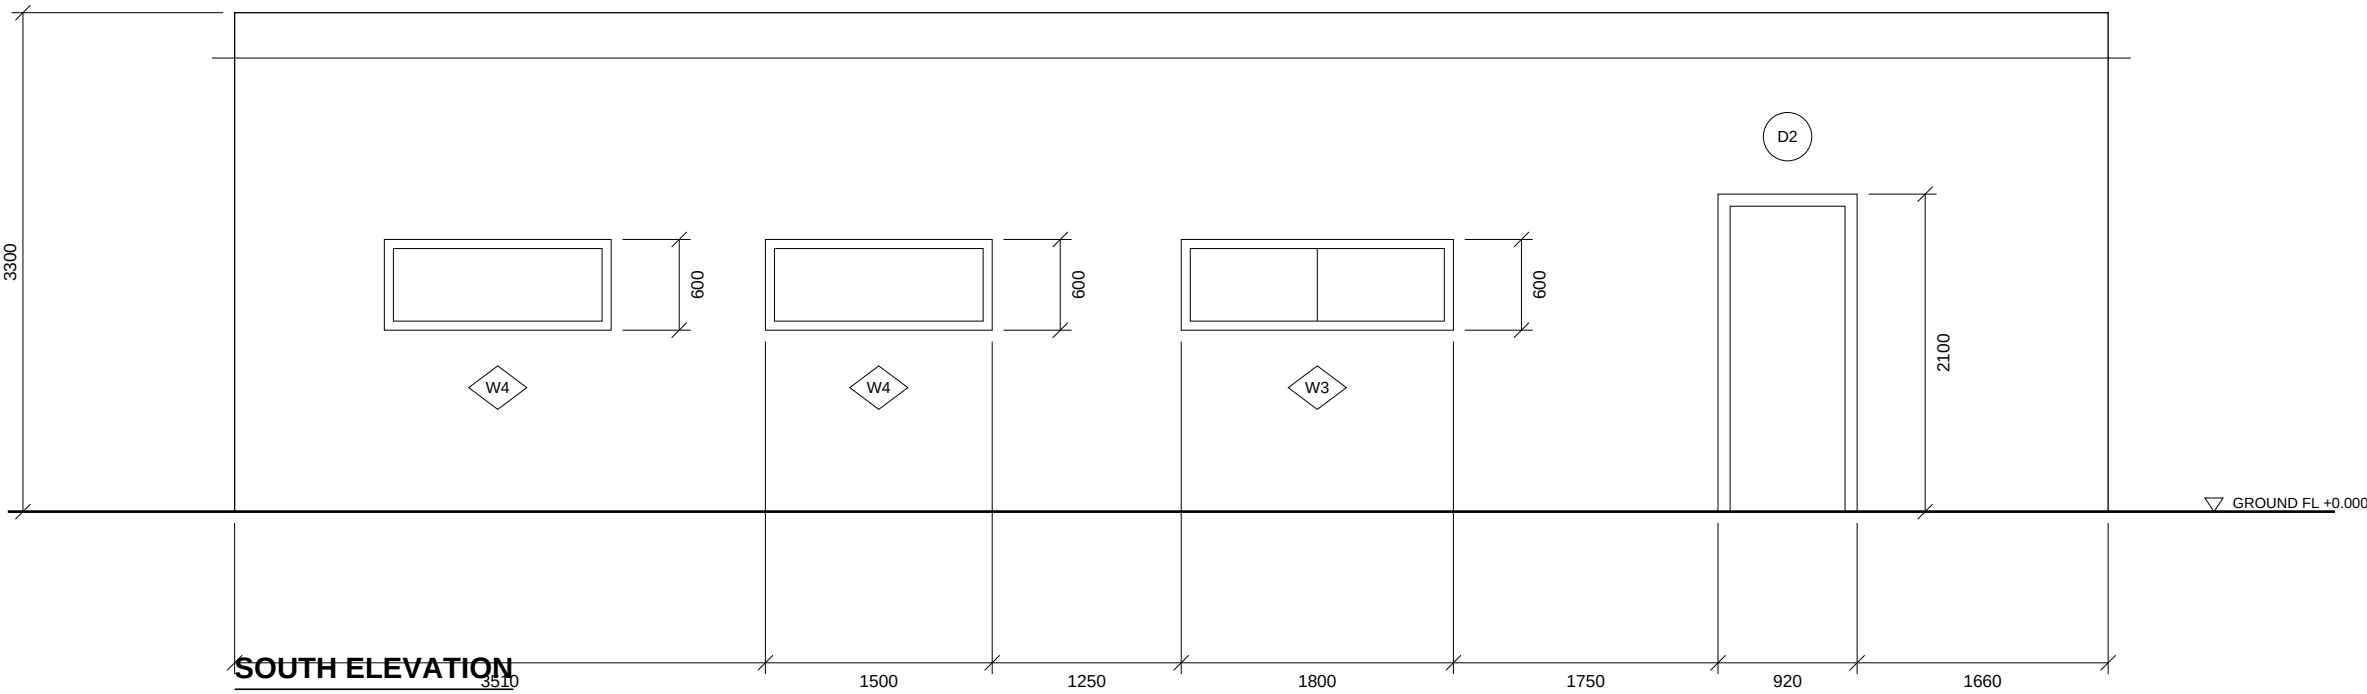

SOUTH ELEVATION

SCALE 1:50

STUDIO NORTH ARCHITECTS

RESIDENTIAL BUILDING

LOT 27, BENCHMARK AVENUE

ALL DIMENSIONS IN MILLIMETRES UNLESS NOTED
OTHERWISE, DO NOT SCALE.

DRAWING TITLE

NORTH & SOUTH ELEVATIONS

SCALE

1:50

SHEET


A-201

DATE

2026-09-01


REV

B

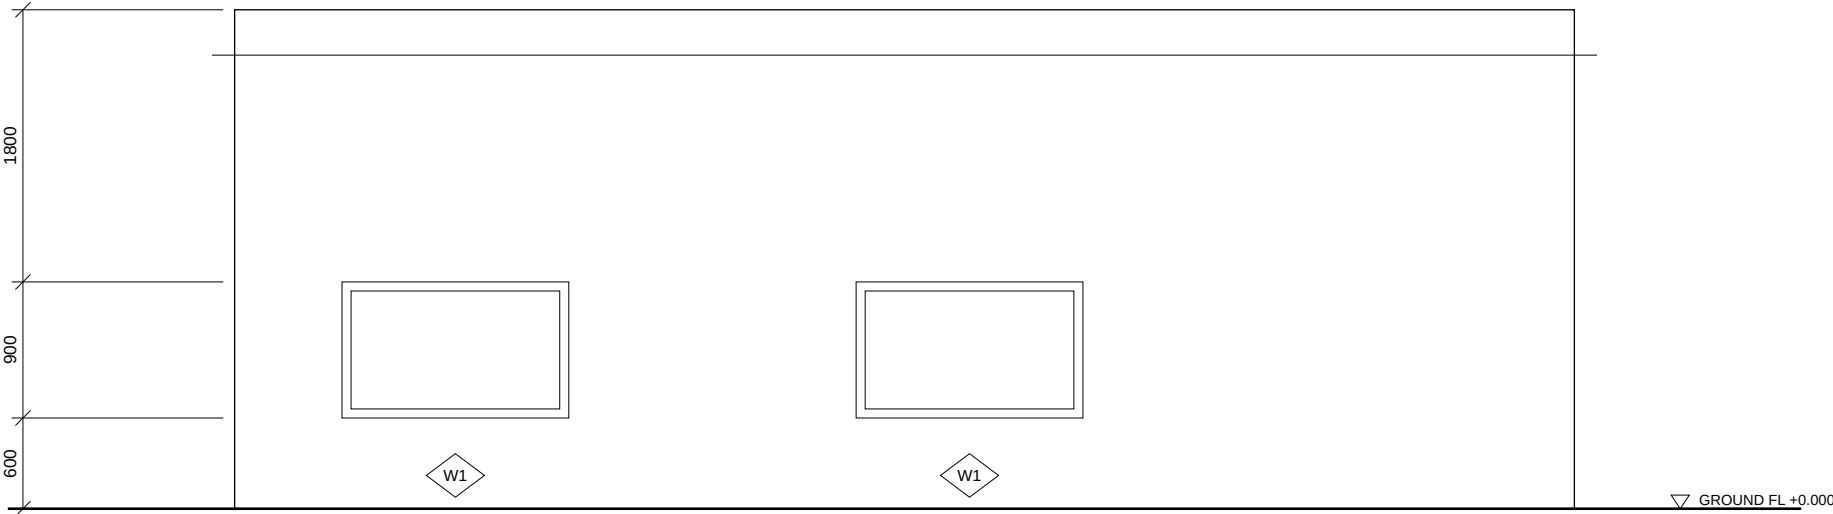

EAST ELEVATION

SCALE 1:50

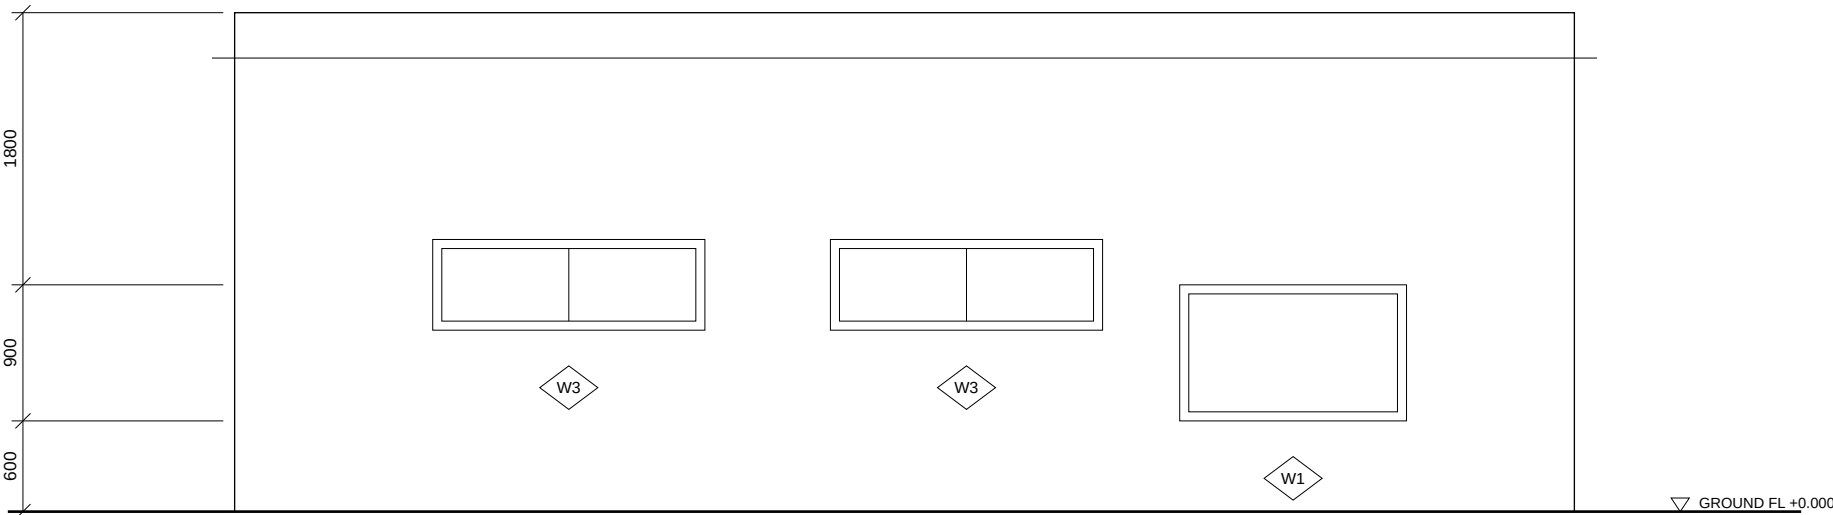

WEST ELEVATION

SCALE 1:50

STUDIO NORTH ARCHITECTS

RESIDENTIAL BUILDING
LOT 27, BENCHMARK AVENUE

ALL DIMENSIONS IN MILLIMETRES UNLESS NOTED
OTHERWISE, DO NOT SCALE.

DRAWING TITLE

EAST & WEST ELEVATIONS

SCALE

1:50

SHEET

A-202

DATE

2026-09-01

REV

B

DOOR SCHEDULE

MARK	TYPE	SIZE (W x H)	QTY	REMARKS
D1	HINGED	720 x 2340	0	
D2	HINGED	920 x 2100	2	
D3	HINGED	820 x 2340	1	

WINDOW SCHEDULE

MARK	TYPE	SIZE (W x H)	SILL	QTY	REMARKS
W1	AWNING	1500 x 600	600	5	
W2	AWNING	1500 x 600	1200	1	
W4	AWNING	1500 x 600	1200	2	

NOTE: ALL SIZES ARE NOMINAL STRUCTURAL OPENING SIZES.

STUDIO NORTH ARCHITECTS RESIDENTIAL BUILDING LOT 27, BENCHMARK AVENUE ALL DIMENSIONS IN MILLIMETRES UNLESS NOTED OTHERWISE. DO NOT SCALE.	DRAWING TITLE DOOR & WINDOW SCHEDULES	
	SCALE NTS	DATE 2026-09-01
	SHEET A-601	REV B