




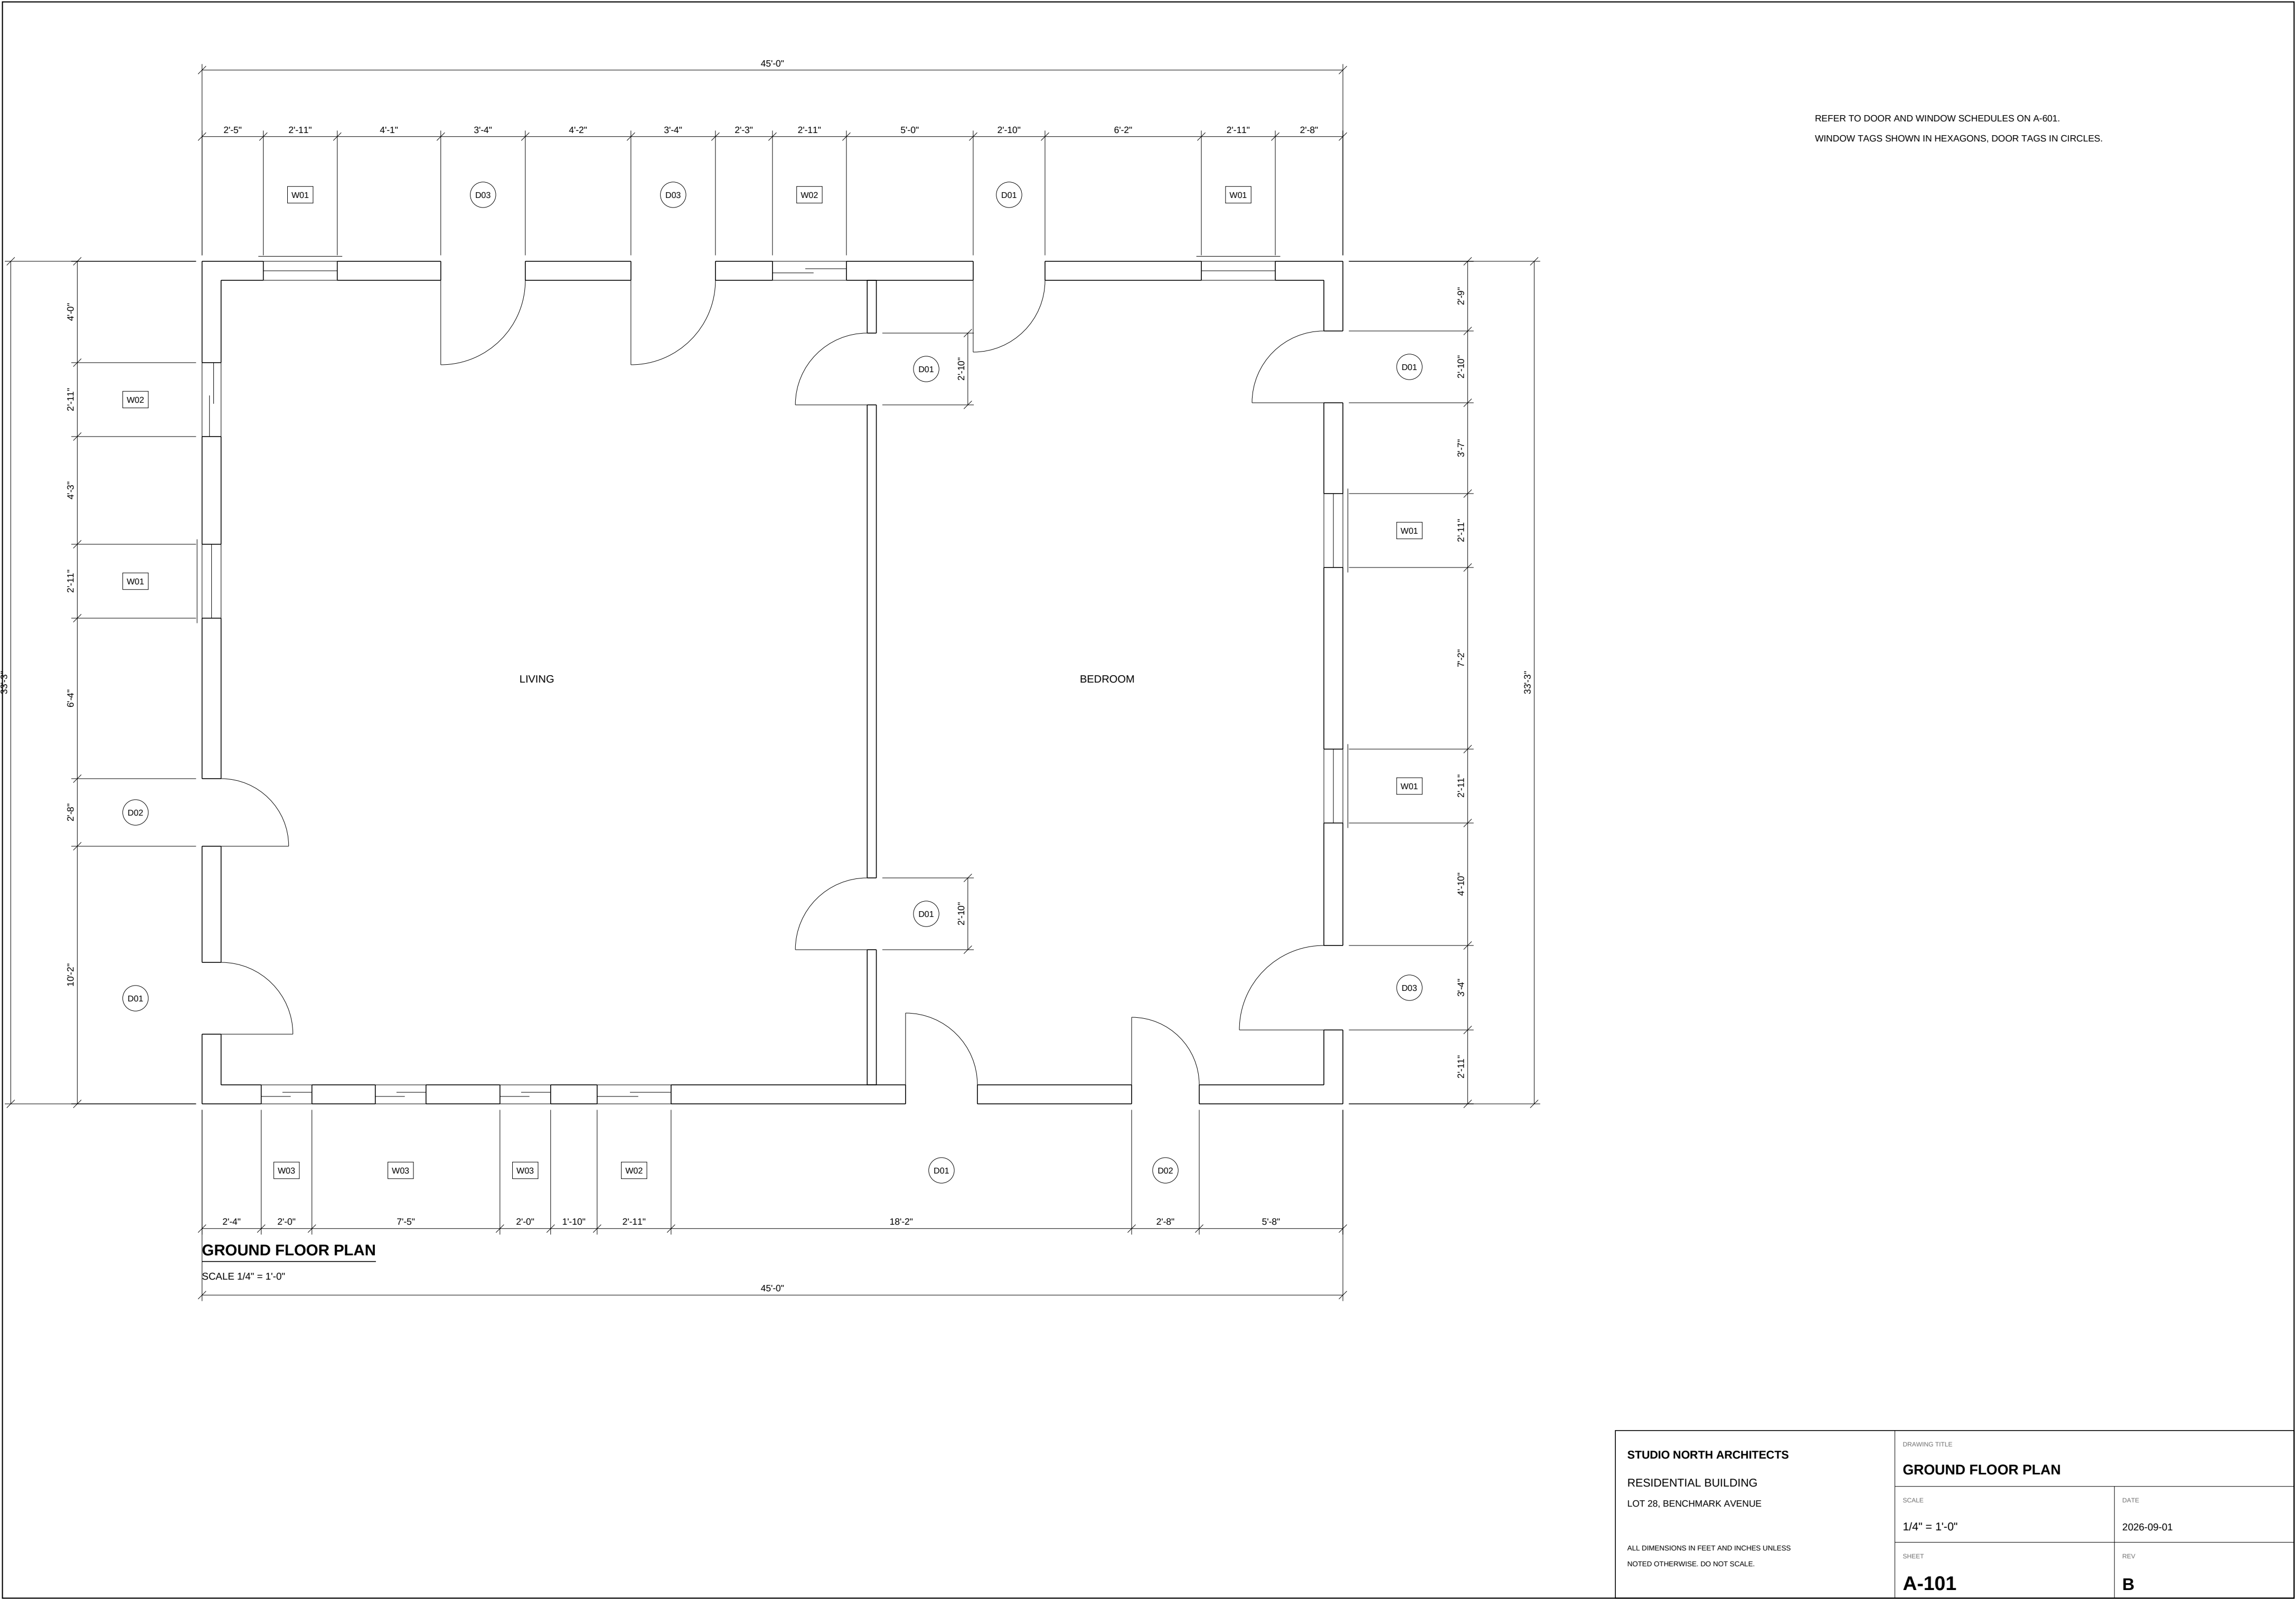

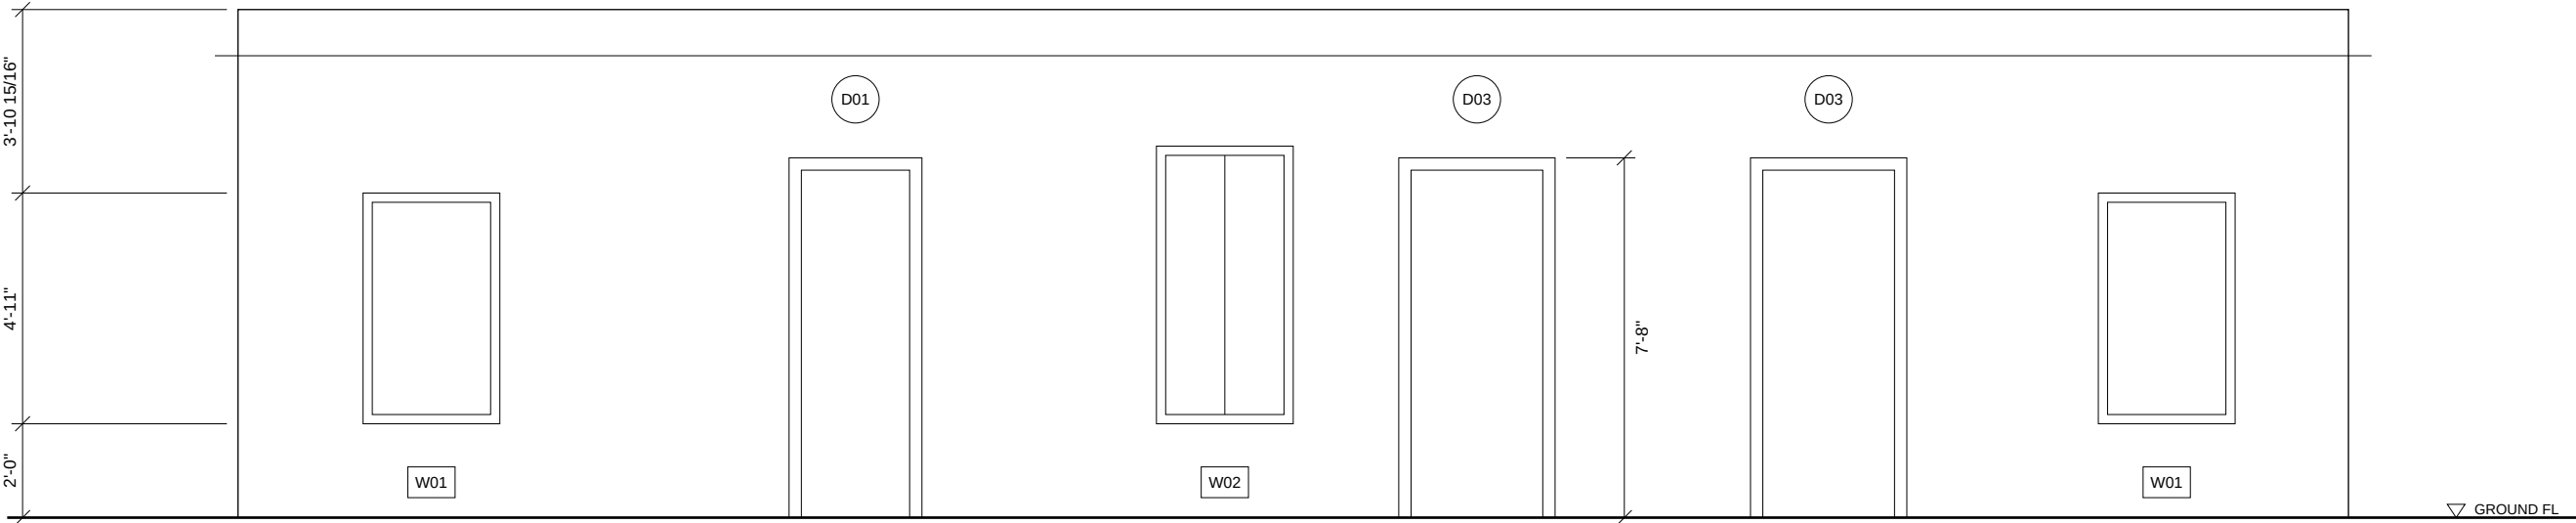

NORTH ELEVATION


SCALE 1/4" = 1'-0"

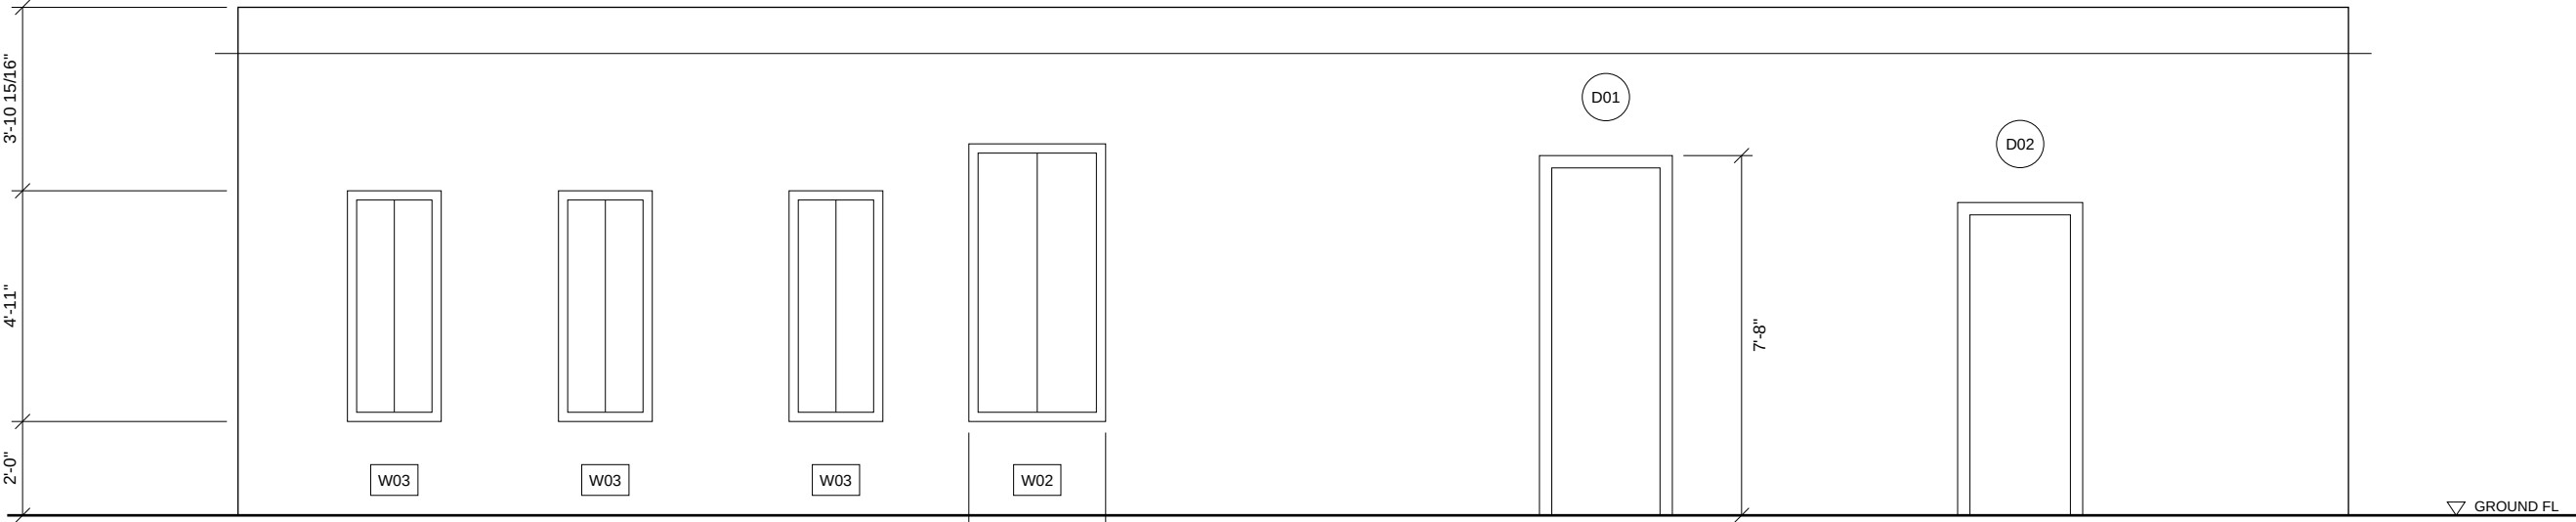

SOUTH ELEVATION


SCALE 1/4" = 1'-0"

STUDIO NORTH ARCHITECTS RESIDENTIAL BUILDING LOT 28, BENCHMARK AVENUE ALL DIMENSIONS IN FEET AND INCHES UNLESS NOTED OTHERWISE. DO NOT SCALE.	DRAWING TITLE NORTH & SOUTH ELEVATIONS	
	SCALE 1/4" = 1'-0"	DATE 2026-09-01
	SHEET A-201	REV B

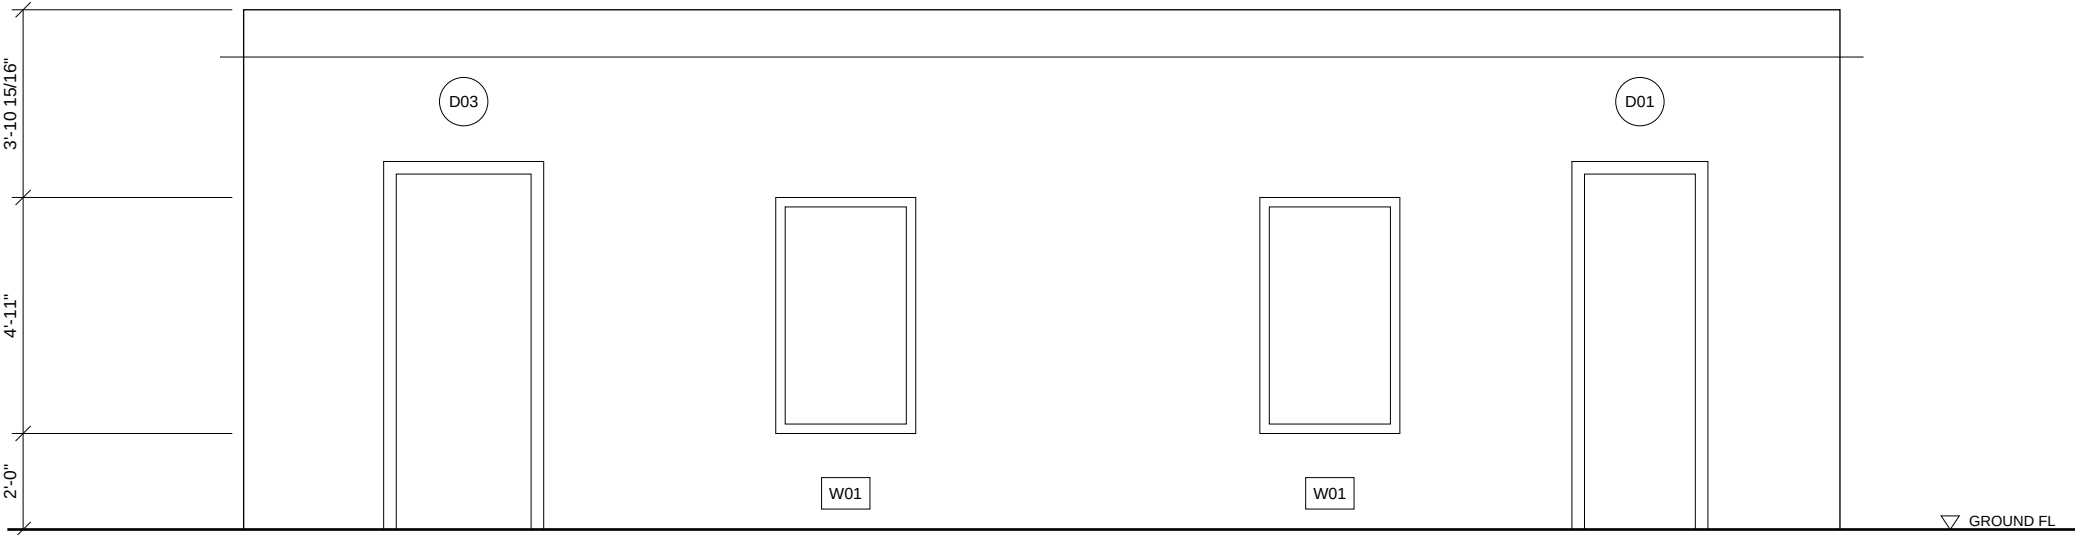

EAST ELEVATION

SCALE 1/4" = 1'-0"

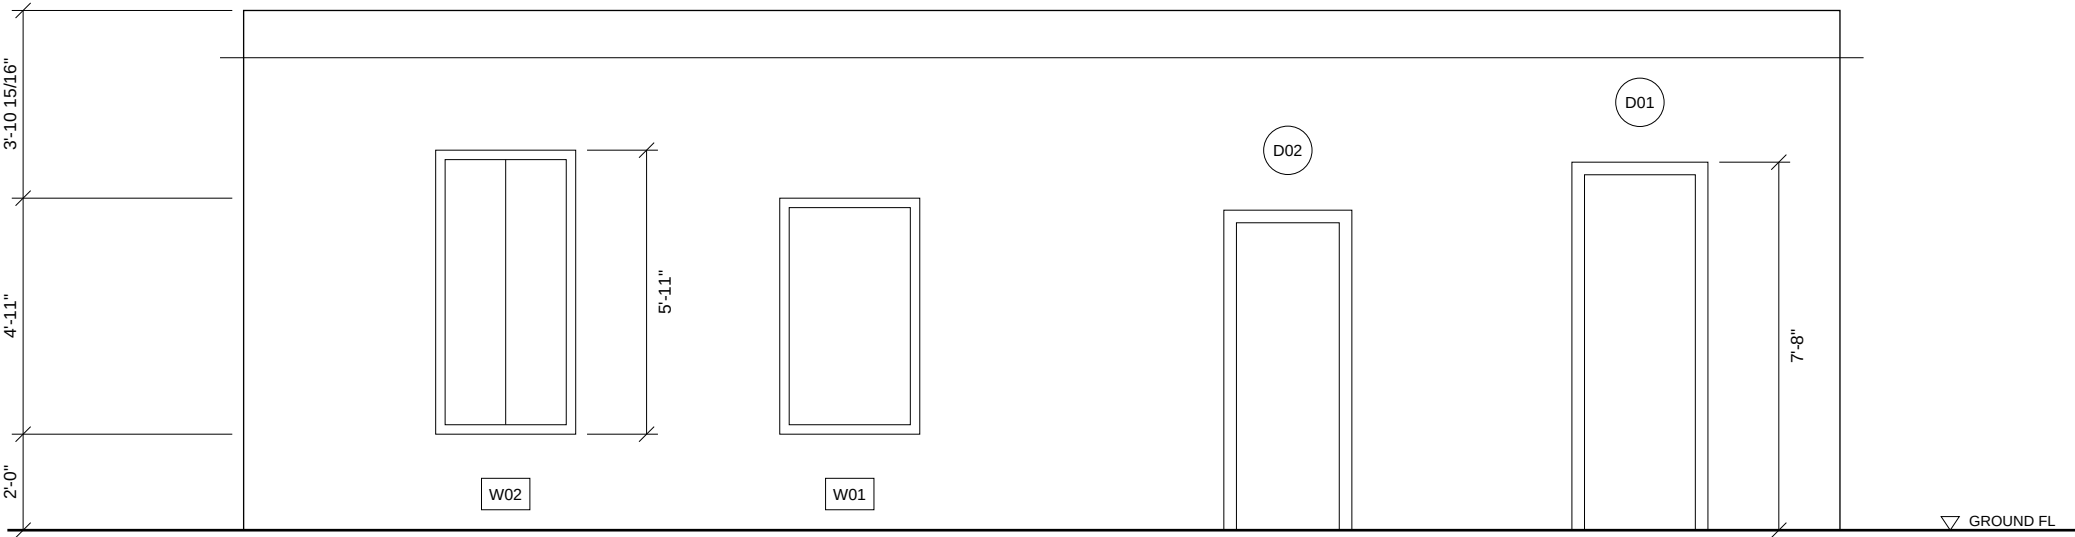

WEST ELEVATION

SCALE 1/4" = 1'-0"

STUDIO NORTH ARCHITECTS

RESIDENTIAL BUILDING
LOT 28, BENCHMARK AVENUE

ALL DIMENSIONS IN FEET AND INCHES UNLESS
NOTED OTHERWISE. DO NOT SCALE.

DRAWING TITLE

EAST & WEST ELEVATIONS

SCALE

1/4" = 1'-0"

SHEET

A-202

DATE

2026-09-01

REV

B

DOOR SCHEDULE

MARK	TYPE	WIDTH	HEIGHT	QTY	REMARKS
D03	HINGED	3'-4"	7'-8"	3	

WINDOW SCHEDULE

MARK	TYPE	WIDTH	HEIGHT	SILL	QTY	REMARKS
W01	AWNING	2'-11"	4'-11"	2'-0"	5	
W02	SLIDING	2'-11"	5'-11"	2'-0"	3	
W03	SLIDING	2'-0"	4'-11"	2'-0"	3	

NOTE: ALL SIZES ARE NOMINAL STRUCTURAL OPENING SIZES.

STUDIO NORTH ARCHITECTS RESIDENTIAL BUILDING LOT 28, BENCHMARK AVENUE ALL DIMENSIONS IN FEET AND INCHES UNLESS NOTED OTHERWISE. DO NOT SCALE.	DRAWING TITLE DOOR & WINDOW SCHEDULES	
	SCALE NTS	DATE 2026-09-01
	SHEET A-601	REV B