

RESIDENTIAL BUILDING


LOT 29, BENCHMARK AVENUE

CONSTRUCTION ISSUE

DRAWING LIST


SHEET	TITLE
A-101	GROUND FLOOR PLAN
A-201	NORTH & SOUTH ELEVATIONS
A-202	EAST & WEST ELEVATIONS
A-601	DOOR & WINDOW SCHEDULES

STUDIO NORTH ARCHITECTS RESIDENTIAL BUILDING LOT 29, BENCHMARK AVENUE ALL DIMENSIONS IN MILLIMETRES UNLESS NOTED OTHERWISE, DO NOT SCALE.	DRAWING TITLE COVER SHEET	
	SCALE NTS	DATE 2026-09-01
	SHEET A-000	REV B

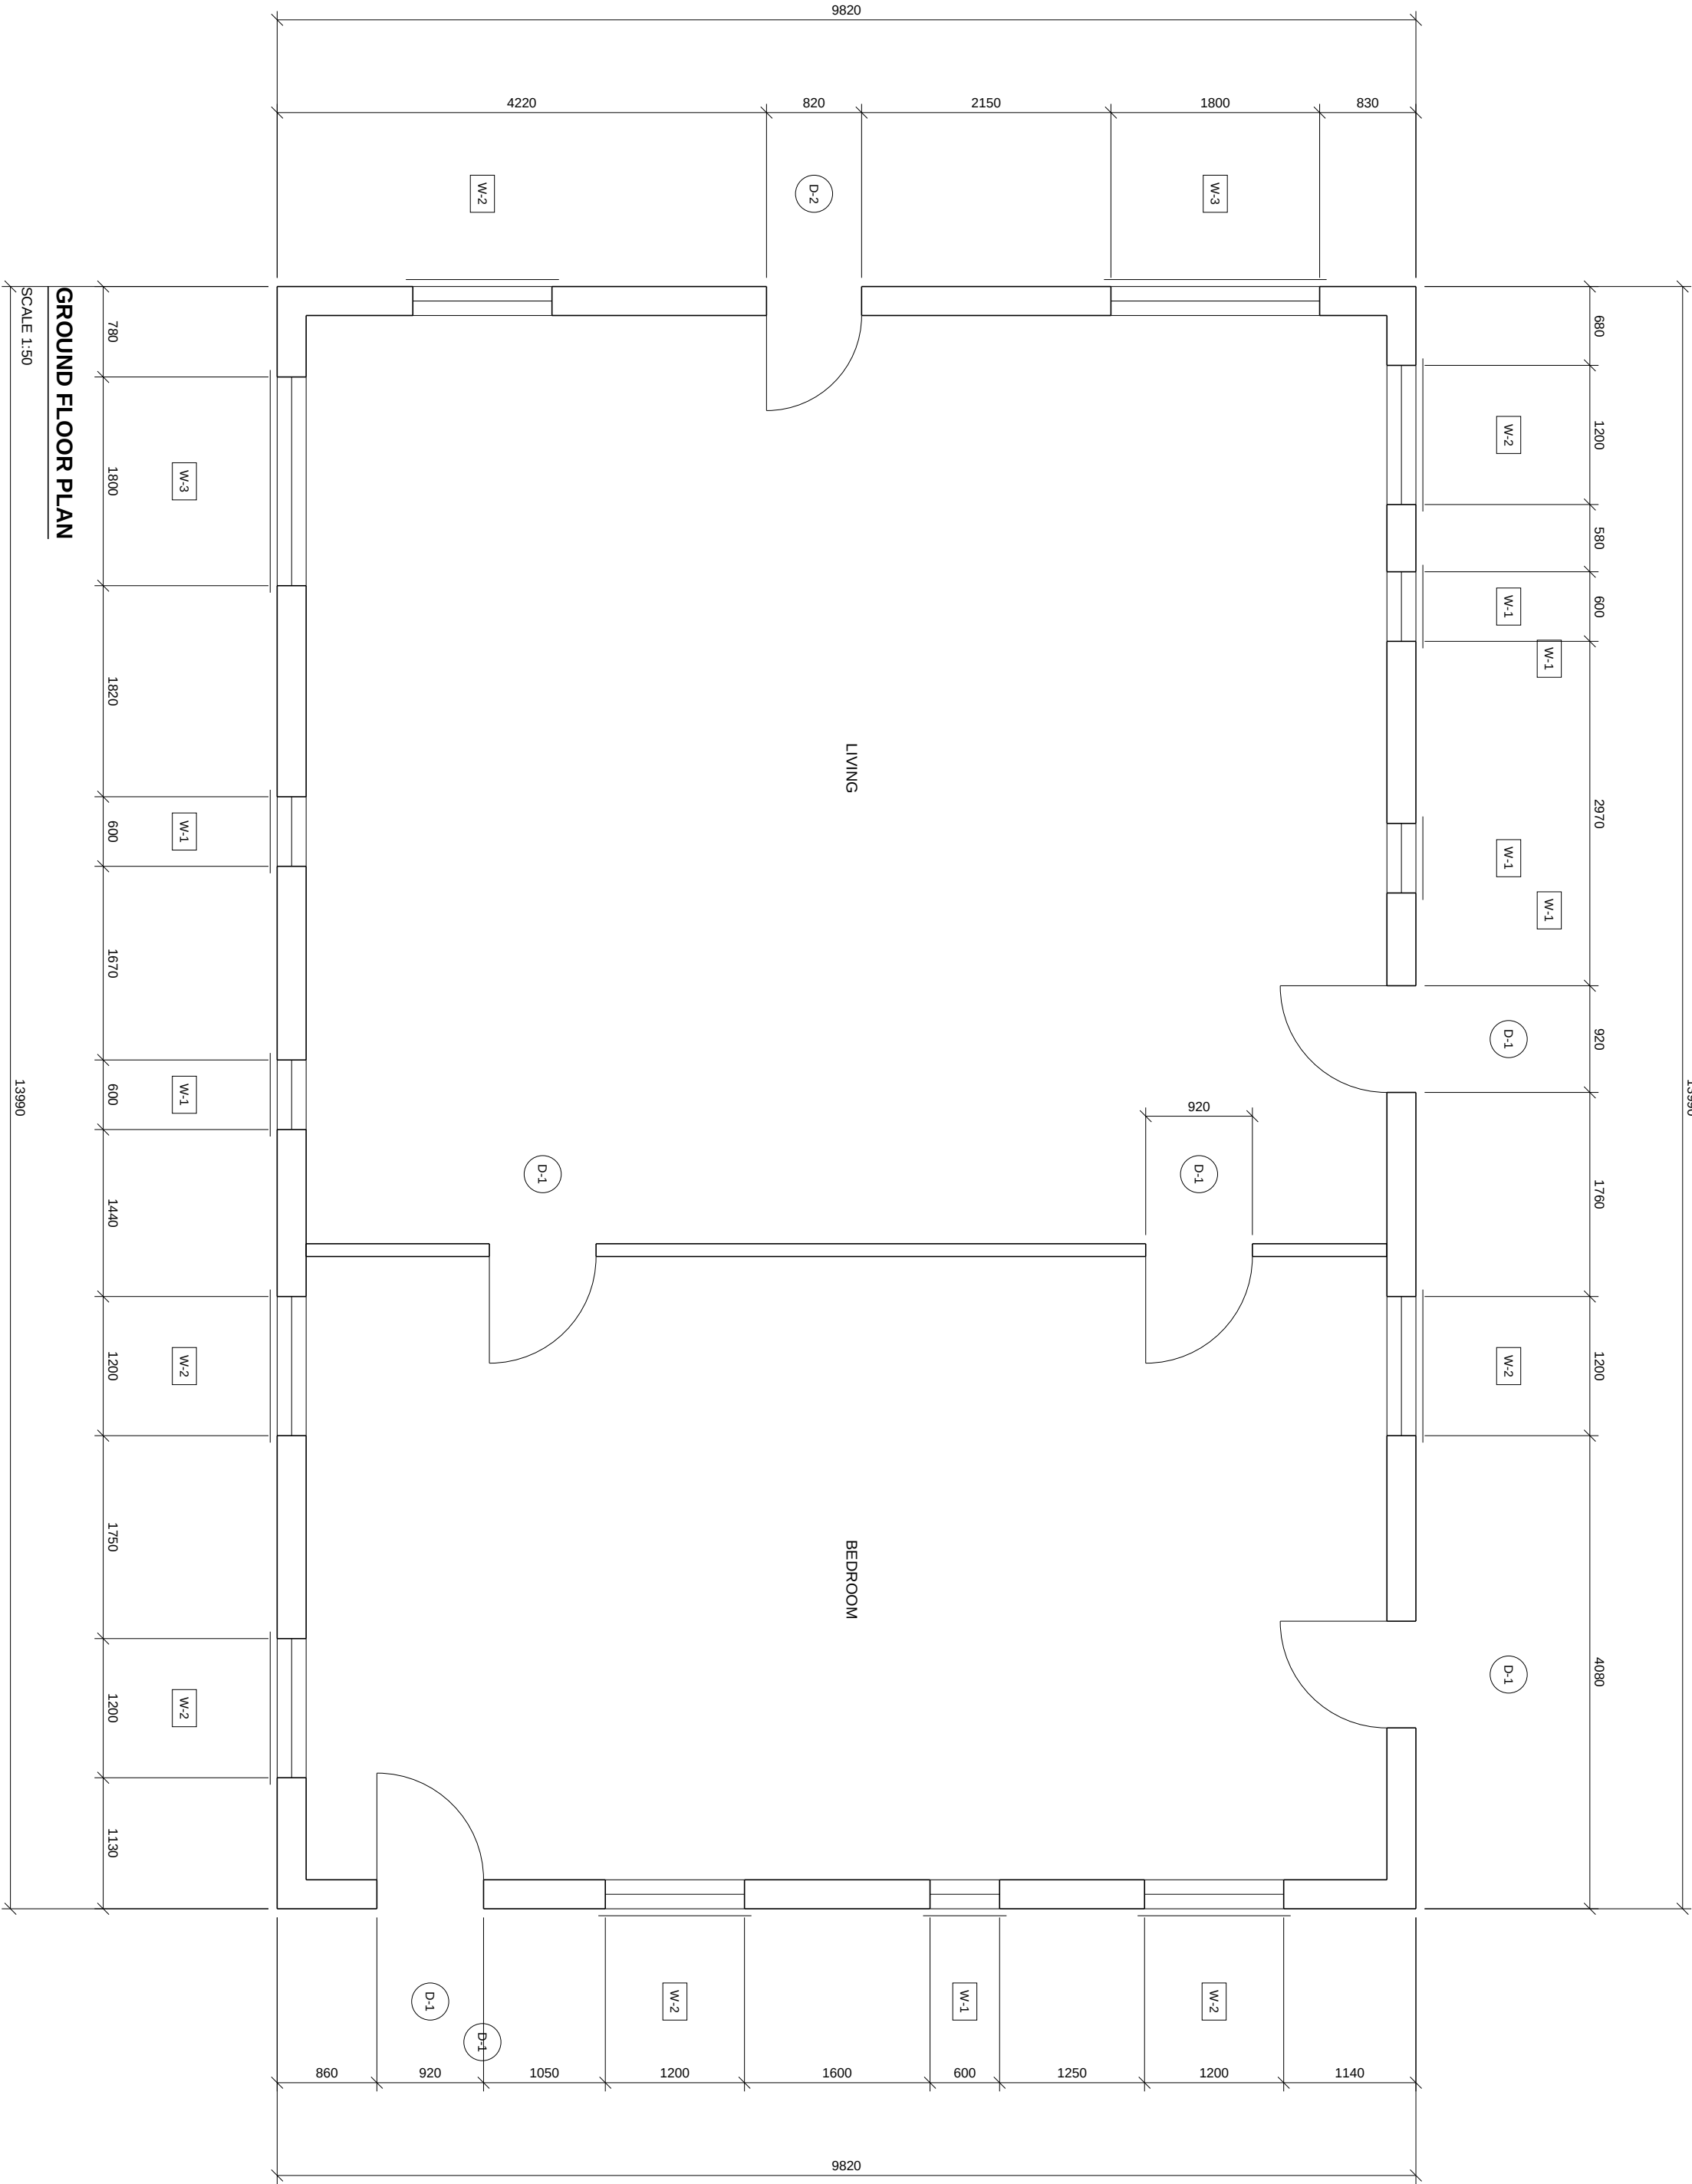


REFER TO DOOR AND WINDOW SCHEDULES ON A-601.
WINDOW TAGS SHOWN IN HEXAGONS, DOOR TAGS IN CIRCLES.

STUDIO NORTH ARCHITECTS RESIDENTIAL BUILDING LOT 29, BENCHMARK AVENUE <
--

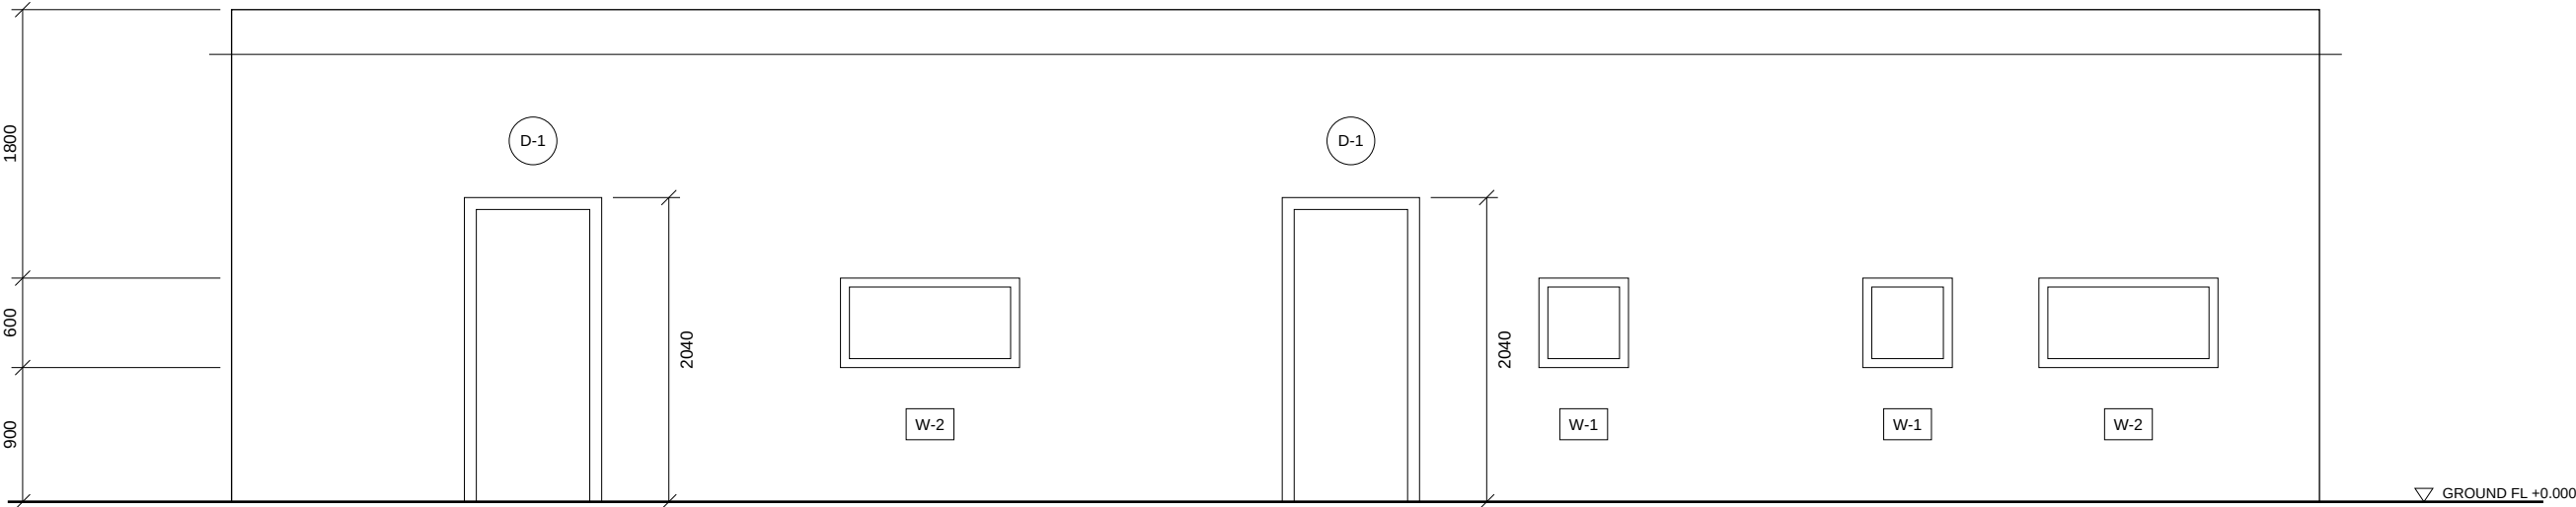

NORTH ELEVATION

SCALE 1:50

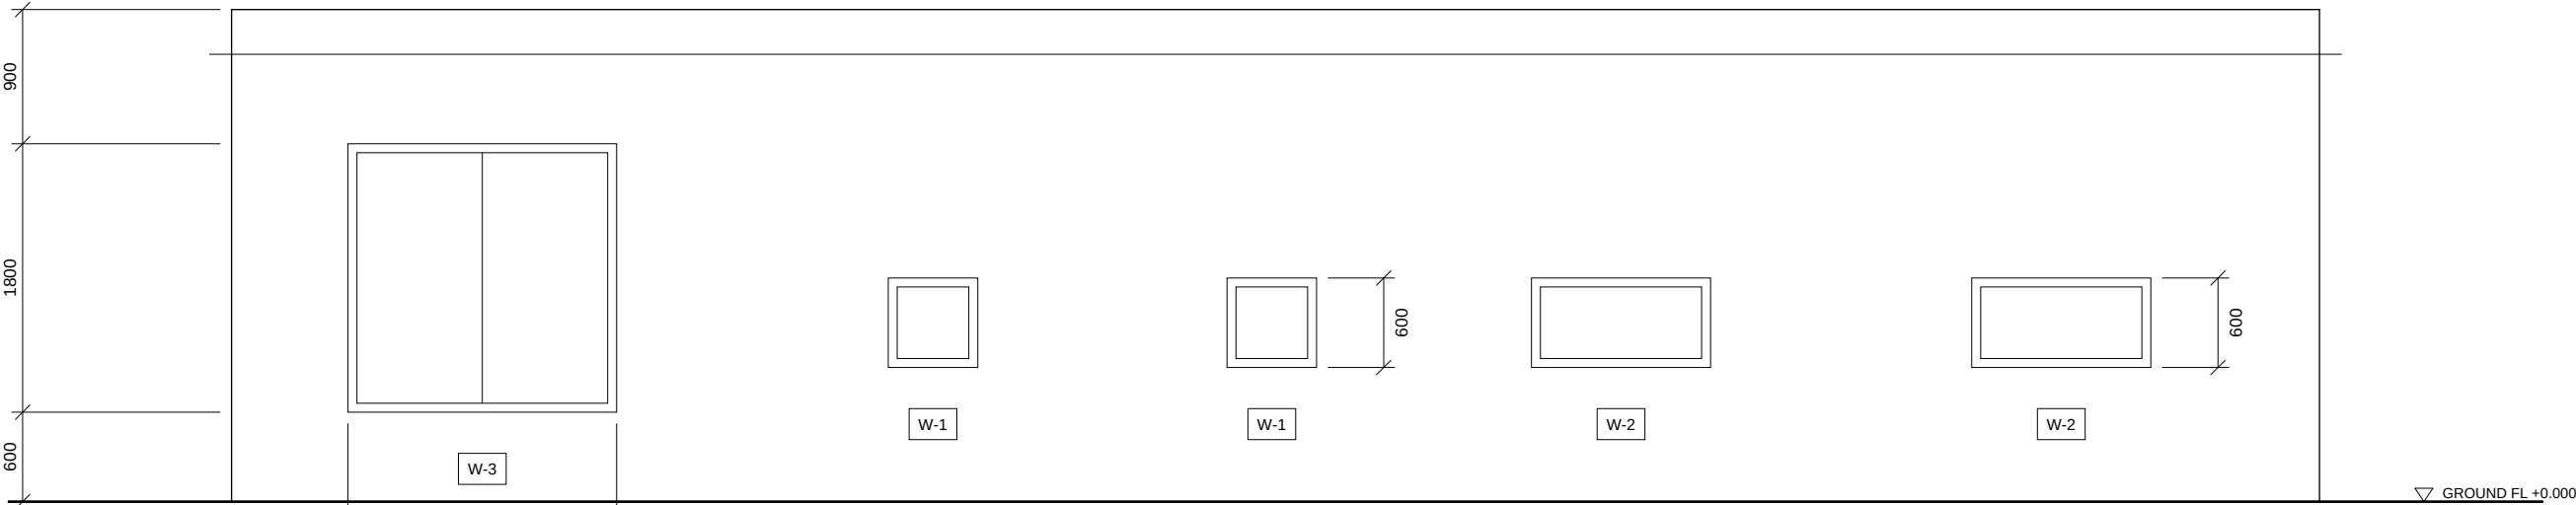

SOUTH ELEVATION

SCALE 1:50

STUDIO NORTH ARCHITECTS

RESIDENTIAL BUILDING
LOT 29, BENCHMARK AVENUE

ALL DIMENSIONS IN MILLIMETRES UNLESS NOTED
OTHERWISE, DO NOT SCALE.

DRAWING TITLE
NORTH & SOUTH ELEVATIONS

SCALE

1:50

SHEET


A-201

DATE

2026-09-01


REV

B

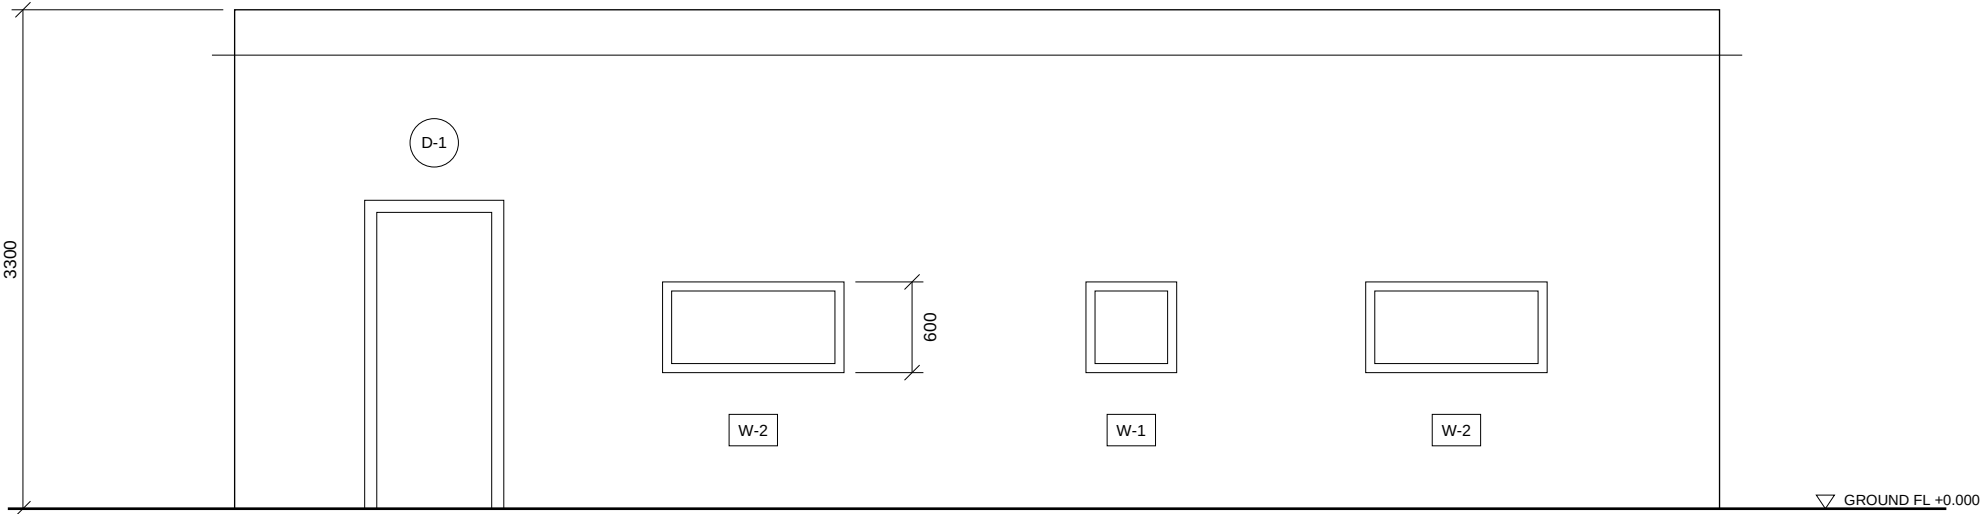

EAST ELEVATION

SCALE 1:50

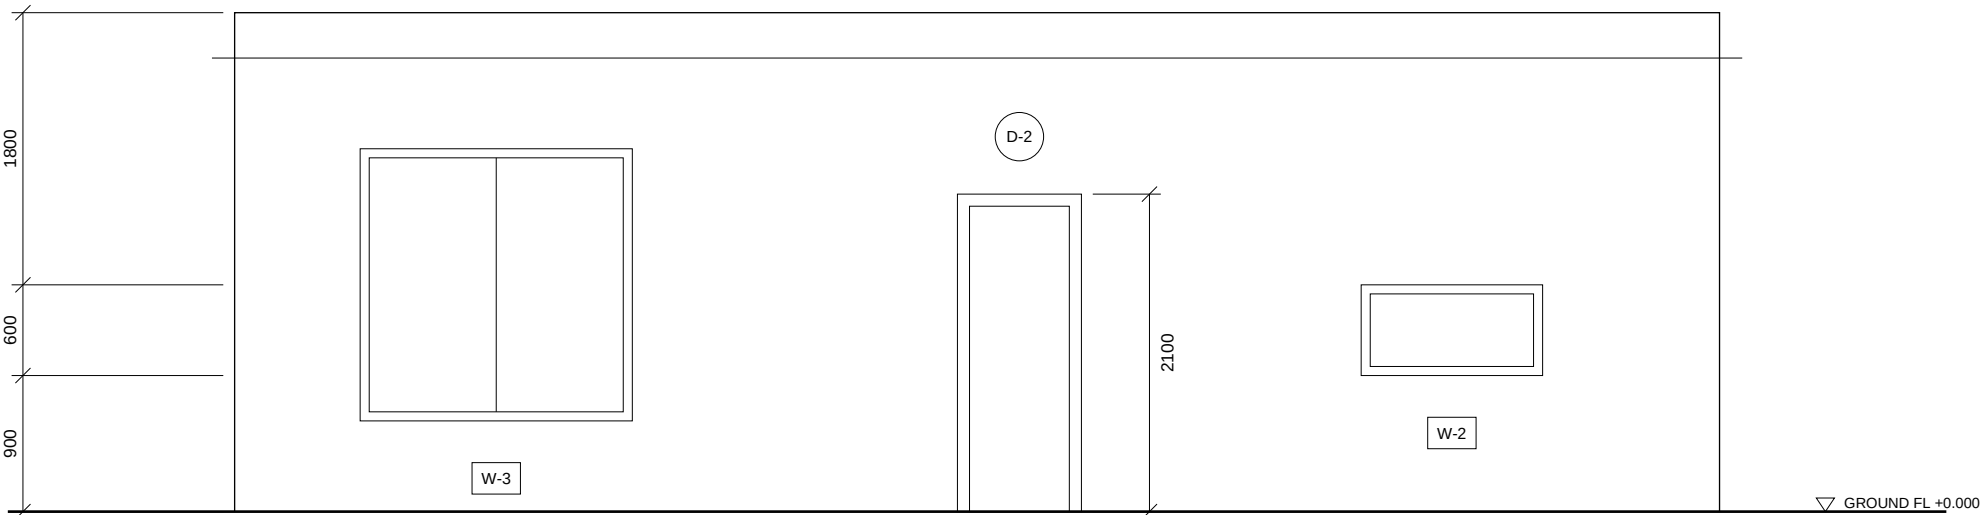

WEST ELEVATION

SCALE 1:50

STUDIO NORTH ARCHITECTS

RESIDENTIAL BUILDING
LOT 29, BENCHMARK AVENUE

ALL DIMENSIONS IN MILLIMETRES UNLESS NOTED
OTHERWISE, DO NOT SCALE.

DRAWING TITLE

EAST & WEST ELEVATIONS

SCALE

1:50

SHEET

A-202

DATE

2026-09-01

REV

B

DOOR SCHEDULE

MARK	TYPE	WIDTH	HEIGHT	QTY	REMARKS
D-1	HINGED	920	2040	5	
D-2	HINGED	820	2100	1	

WINDOW SCHEDULE

MARK	TYPE	WIDTH	HEIGHT	SILL	QTY	REMARKS
W-1	AWNING	600	600	900	5	
W-2	AWNING	1200	600	900	7	
W-3	AWNING	1800	1800	600	2	

NOTE: ALL SIZES ARE NOMINAL STRUCTURAL OPENING SIZES.

STUDIO NORTH ARCHITECTS RESIDENTIAL BUILDING LOT 29, BENCHMARK AVENUE ALL DIMENSIONS IN MILLIMETRES UNLESS NOTED OTHERWISE. DO NOT SCALE.	DRAWING TITLE DOOR & WINDOW SCHEDULES	
	SCALE NTS	DATE 2026-09-01
	SHEET A-601	REV B