

RESIDENTIAL BUILDING


LOT 32, BENCHMARK AVENUE

CONSTRUCTION ISSUE

DRAWING LIST


SHEET	TITLE
A-101	GROUND FLOOR PLAN
A-201	NORTH & SOUTH ELEVATIONS
A-202	EAST & WEST ELEVATIONS
A-601	DOOR & WINDOW SCHEDULES

STUDIO NORTH ARCHITECTS RESIDENTIAL BUILDING LOT 32, BENCHMARK AVENUE ALL DIMENSIONS IN FEET AND INCHES UNLESS NOTED OTHERWISE. DO NOT SCALE.	DRAWING TITLE COVER SHEET	
	SCALE NTS	DATE 2026-09-01
	SHEET A-000	REV B

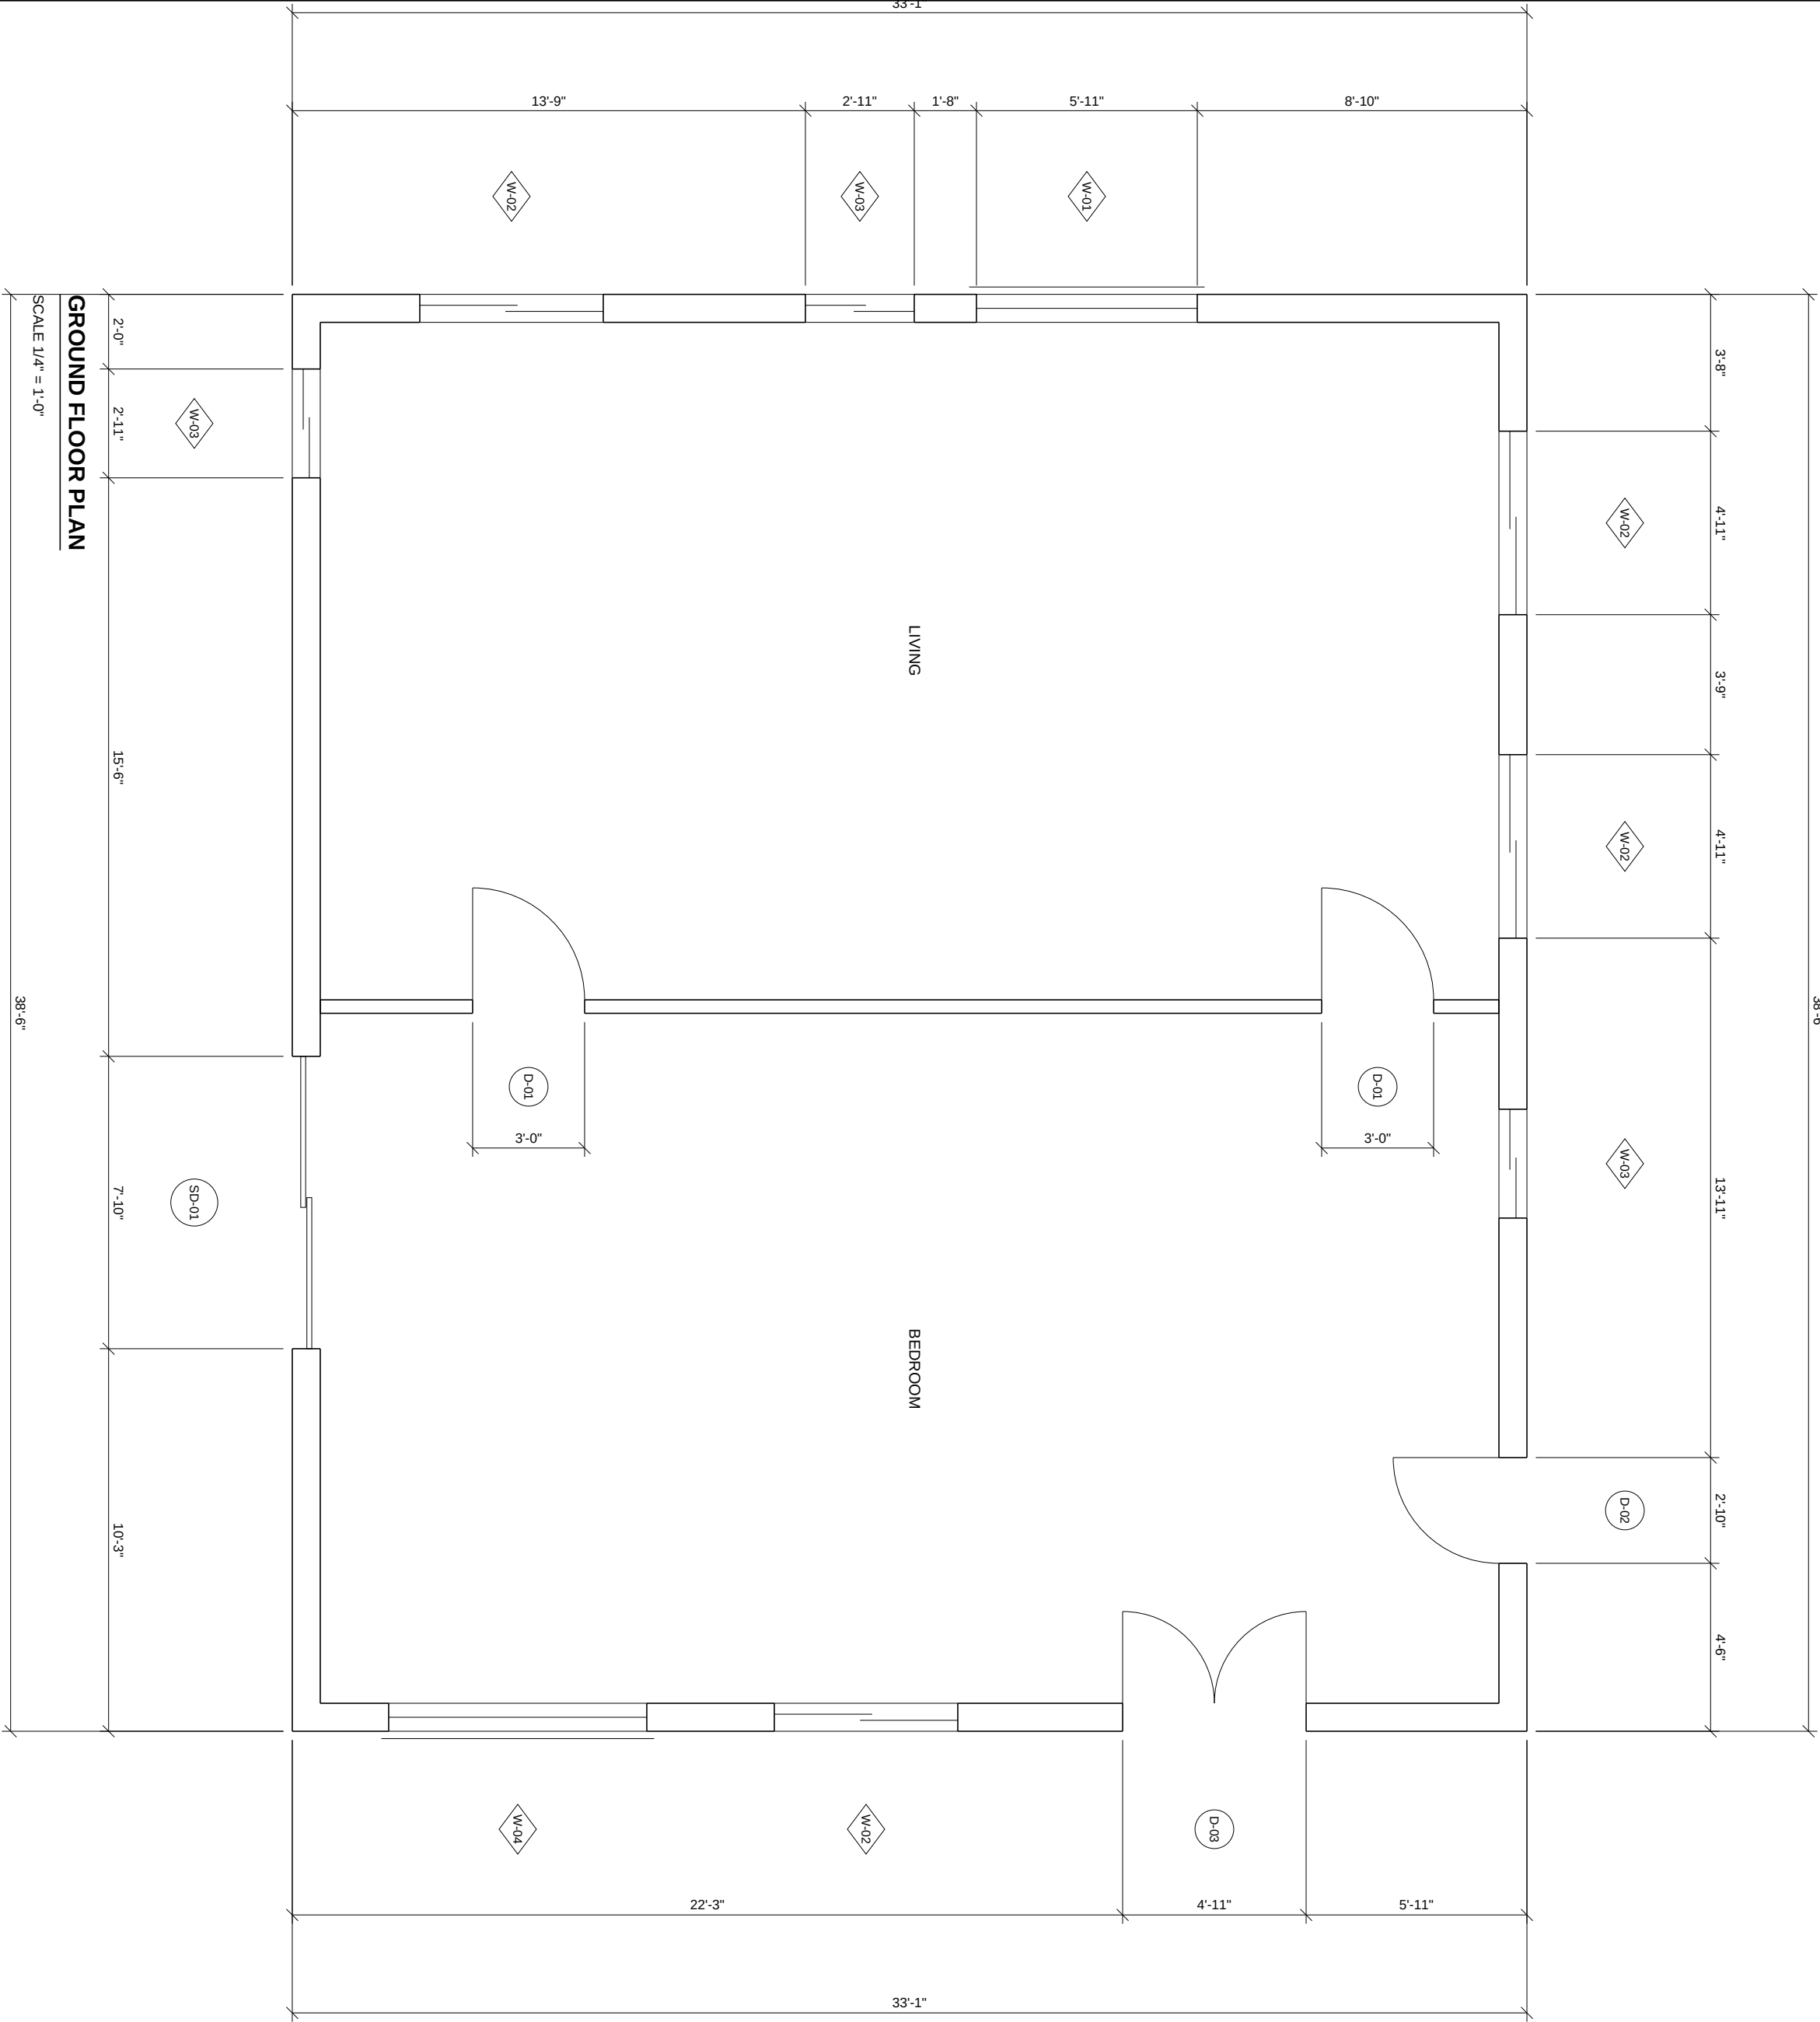


REFER TO DOOR AND WINDOW SCHEDULES ON A-601.
WINDOW TAGS SHOWN IN HEXAGONS, DOOR TAGS IN CIRCLES.

STUDIO NORTH ARCHITECTS		DRAWING TITLE	
RESIDENTIAL BUILDING		GROUND FLOOR PLAN	
LOT 32, BENCHMARK AVENUE		SCALE	DATE
ALL DIMENSIONS IN FEET AND INCHES UNLESS NOTED OTHERWISE. DO NOT SCALE.		1/4" = 1'-0"	2026-09-01
		SHEET	REV
A-101			B

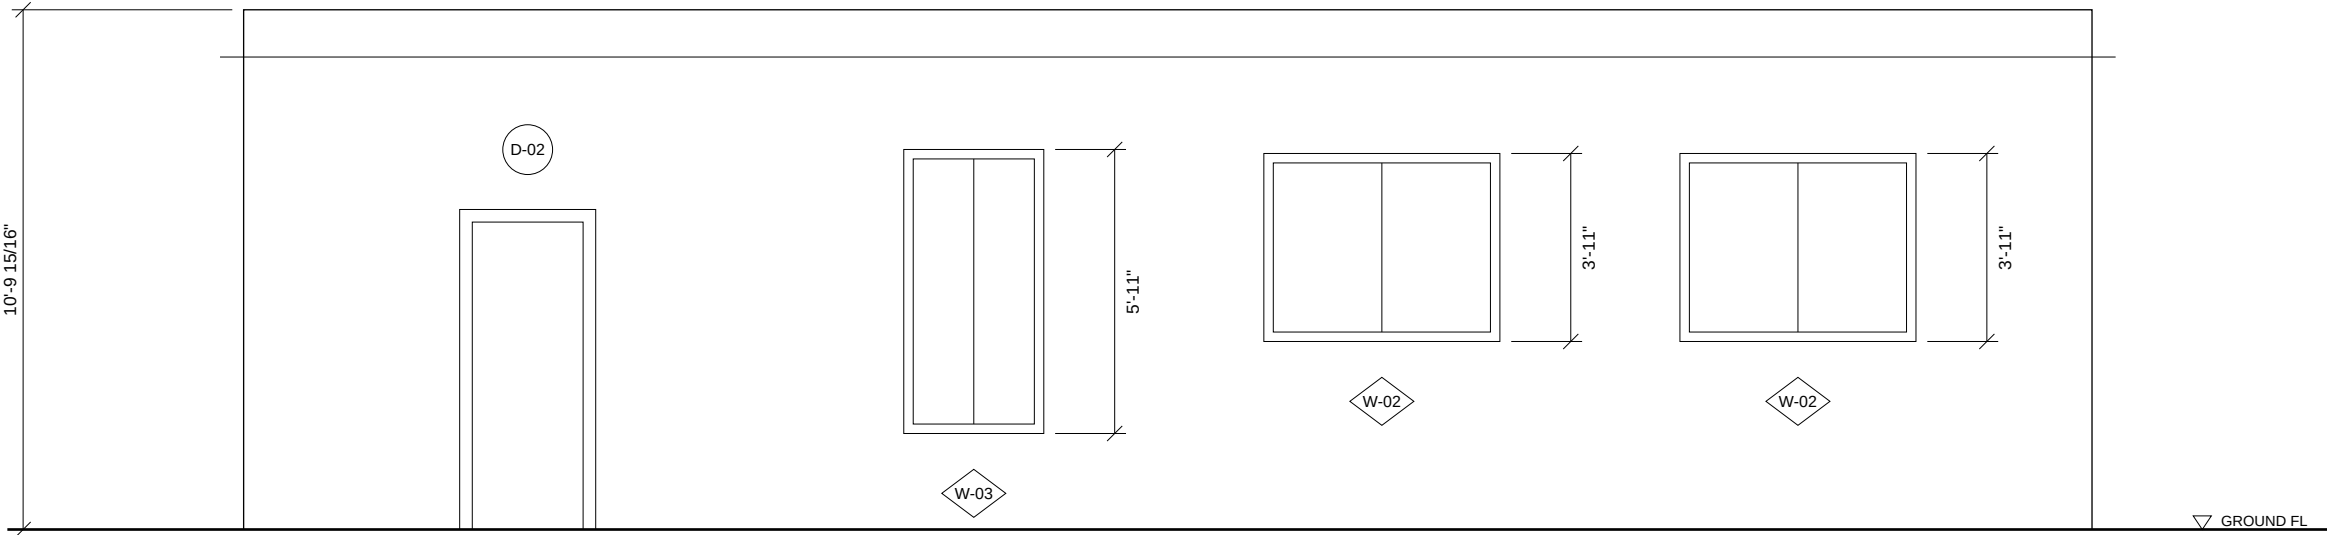

NORTH ELEVATION


SCALE 1/4" = 1'-0"

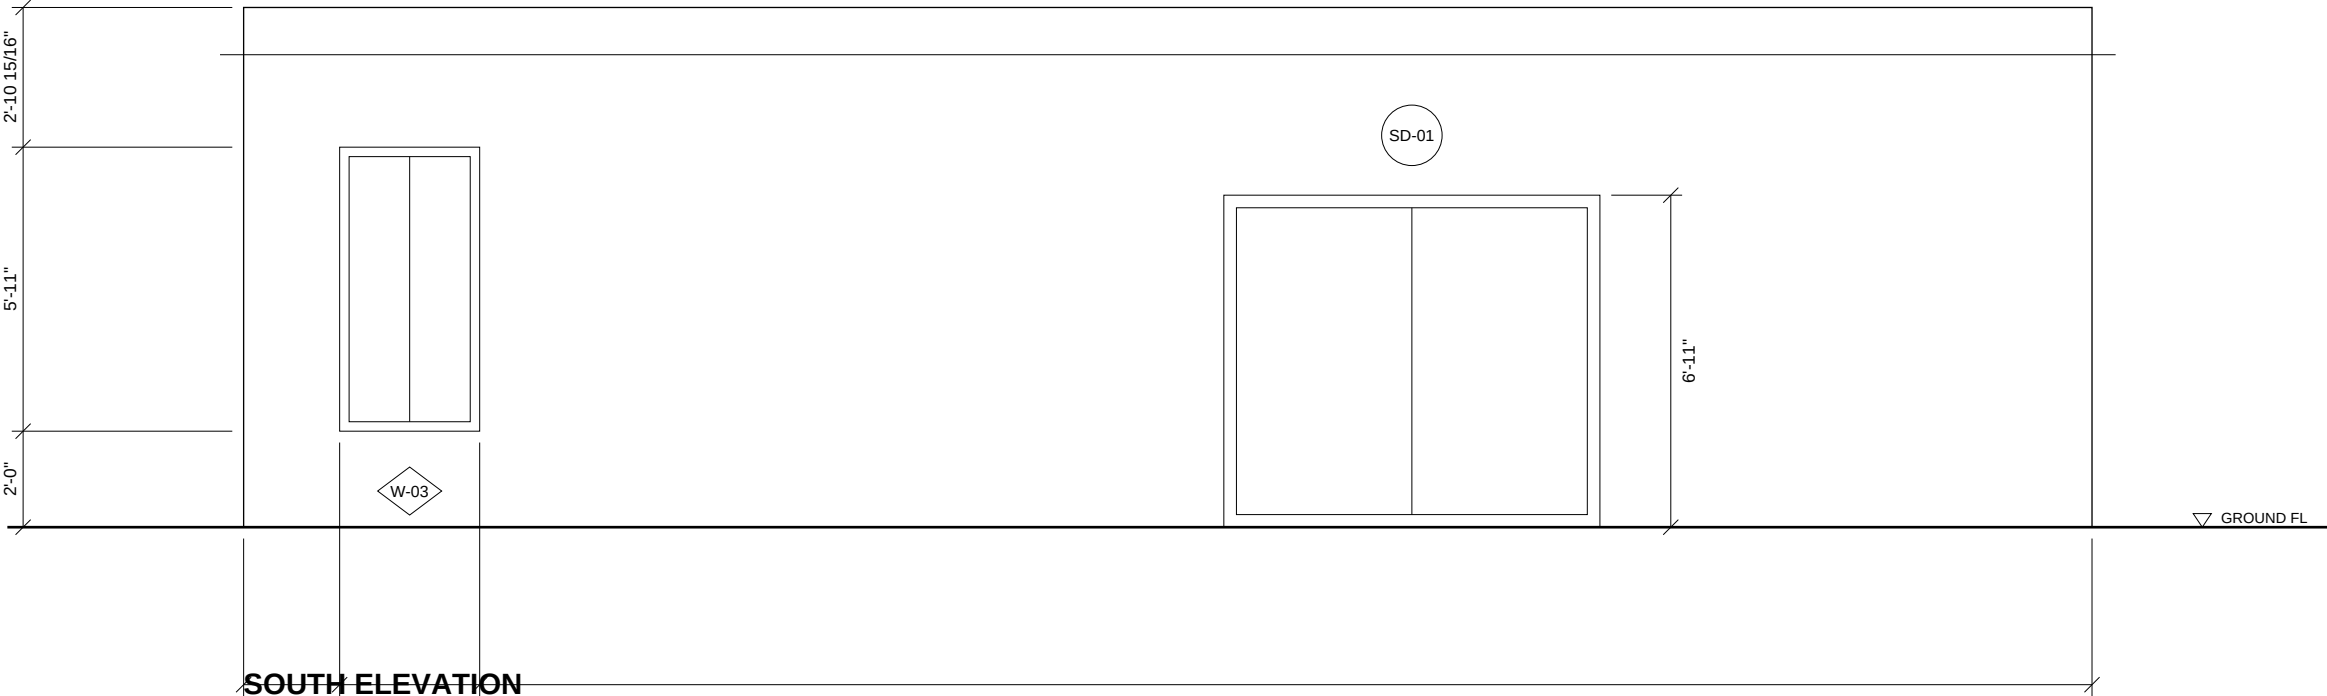

SOUTH ELEVATION


SCALE 1/4" = 1'-0"

STUDIO NORTH ARCHITECTS RESIDENTIAL BUILDING LOT 32, BENCHMARK AVENUE ALL DIMENSIONS IN FEET AND INCHES UNLESS NOTED OTHERWISE. DO NOT SCALE.	DRAWING TITLE NORTH & SOUTH ELEVATIONS	
	SCALE 1/4" = 1'-0"	DATE 2026-09-01
	SHEET A-201	REV B

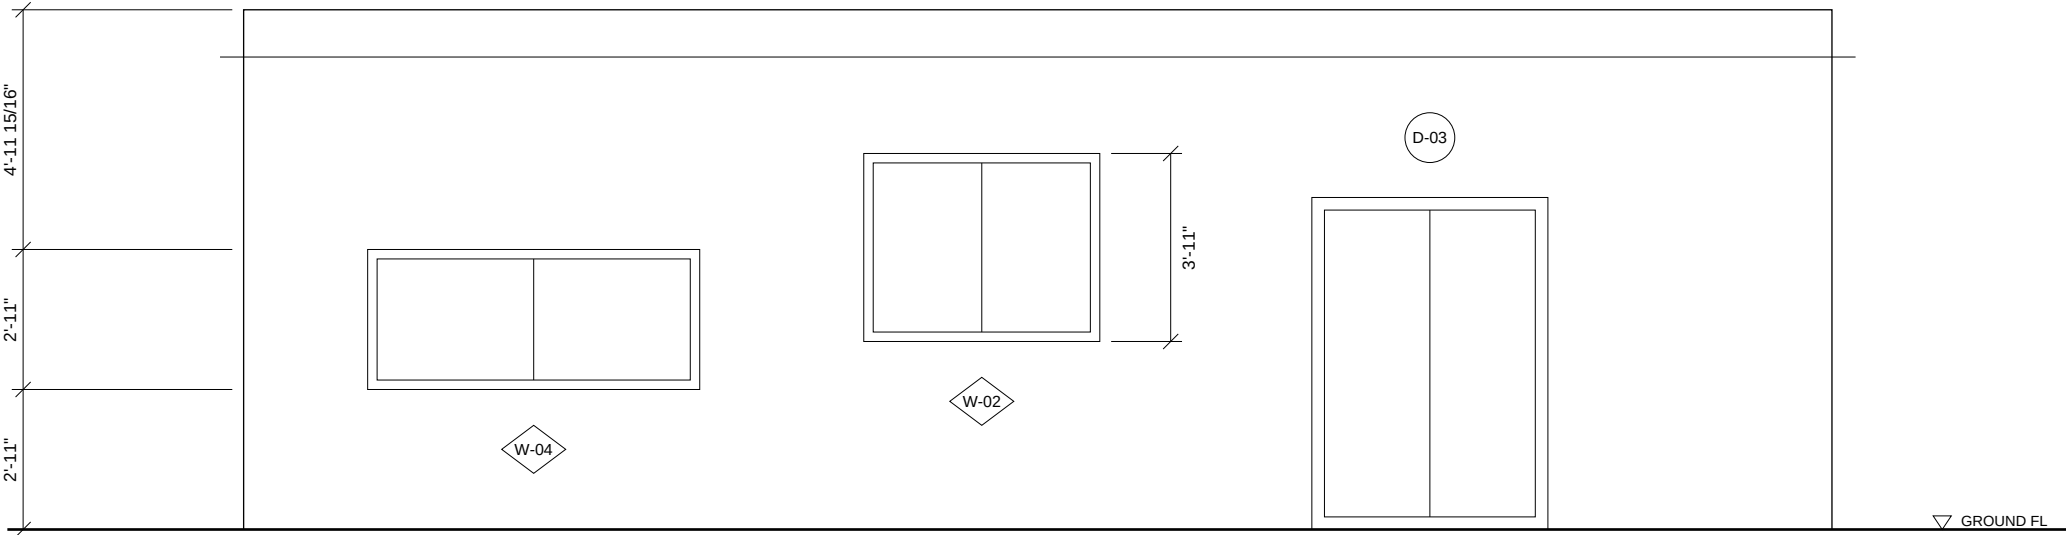

EAST ELEVATION

SCALE 1/4" = 1'-0"

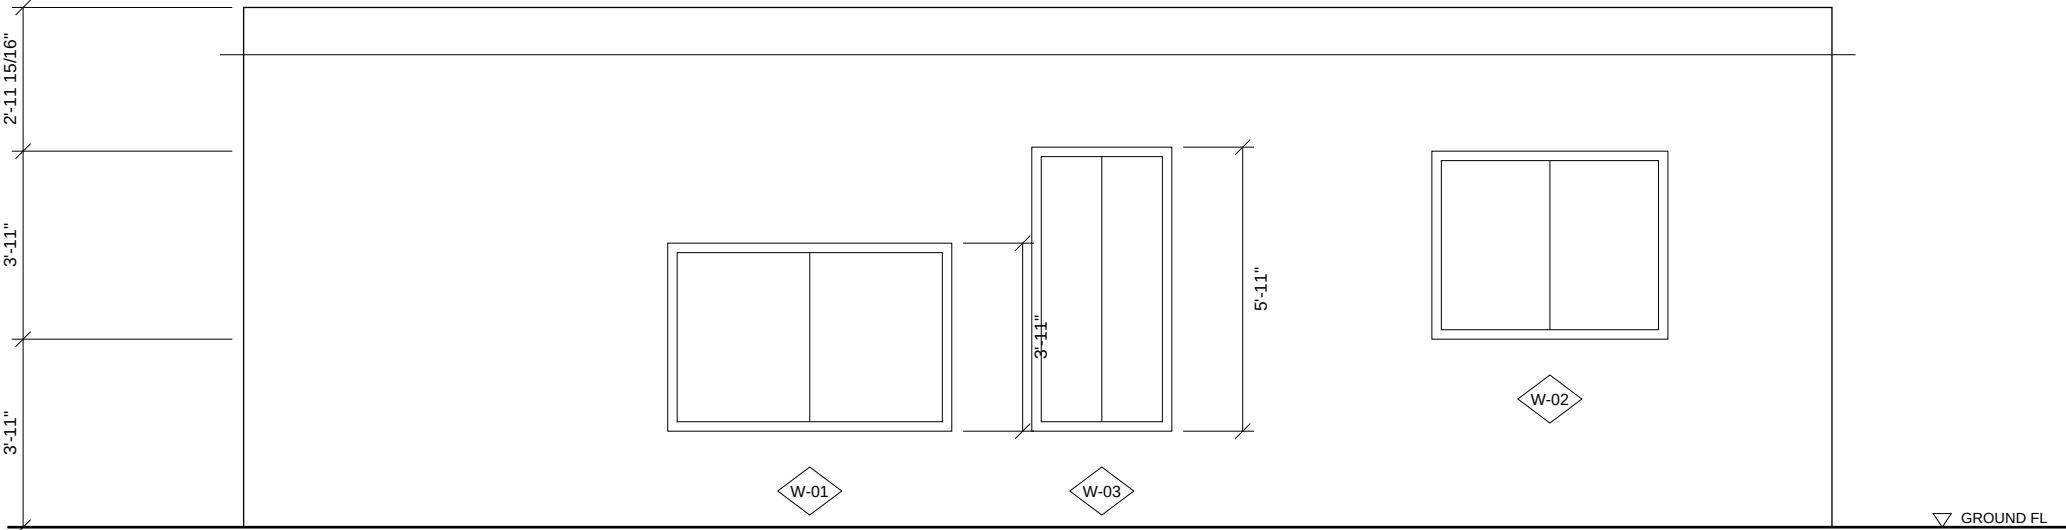

WEST ELEVATION

SCALE 1/4" = 1'-0"

STUDIO NORTH ARCHITECTS

RESIDENTIAL BUILDING
LOT 32, BENCHMARK AVENUE

ALL DIMENSIONS IN FEET AND INCHES UNLESS
NOTED OTHERWISE. DO NOT SCALE.

DRAWING TITLE

EAST & WEST ELEVATIONS

SCALE

1/4" = 1'-0"

SHEET

A-202

DATE

2026-09-01

REV

B

DOOR SCHEDULE

MARK	TYPE	WIDTH	HEIGHT	QTY	REMARKS
D-01	HINGED	3'-0"	6'-8"	2	
D-02	HINGED	2'-10"	6'-8"	1	
SD-01	SLIDING DOOR	7'-10"	6'-11"	1	
D-03	FRENCH DOORS	4'-11"	6'-11"	1	

WINDOW SCHEDULE

MARK	TYPE	WIDTH	HEIGHT	SILL	QTY	REMARKS
W-01	AWNING	5'-11"	3'-11"	2'-0"	1	
W-02	SLIDING	4'-11"	3'-11"	3'-11"	4	
W-03	SLIDING	2'-11"	5'-11"	2'-0"	3	
W-04	AWNING	6'-11"	2'-11"	2'-11"	1	

NOTE: ALL SIZES ARE NOMINAL STRUCTURAL OPENING SIZES.

STUDIO NORTH ARCHITECTS RESIDENTIAL BUILDING LOT 32, BENCHMARK AVENUE ALL DIMENSIONS IN FEET AND INCHES UNLESS NOTED OTHERWISE. DO NOT SCALE.	DRAWING TITLE DOOR & WINDOW SCHEDULES	
	SCALE NTS	DATE 2026-09-01
	SHEET A-601	REV B