

RESIDENTIAL BUILDING


LOT 33, BENCHMARK AVENUE

CONSTRUCTION ISSUE

DRAWING LIST


SHEET	TITLE
A-101	GROUND FLOOR PLAN
A-201	NORTH & SOUTH ELEVATIONS
A-202	EAST & WEST ELEVATIONS
A-601	DOOR & WINDOW SCHEDULES

STUDIO NORTH ARCHITECTS RESIDENTIAL BUILDING LOT 33, BENCHMARK AVENUE ALL DIMENSIONS IN MILLIMETRES UNLESS NOTED OTHERWISE, DO NOT SCALE.	DRAWING TITLE COVER SHEET	
	SCALE NTS	DATE 2026-09-01
	SHEET A-000	REV B

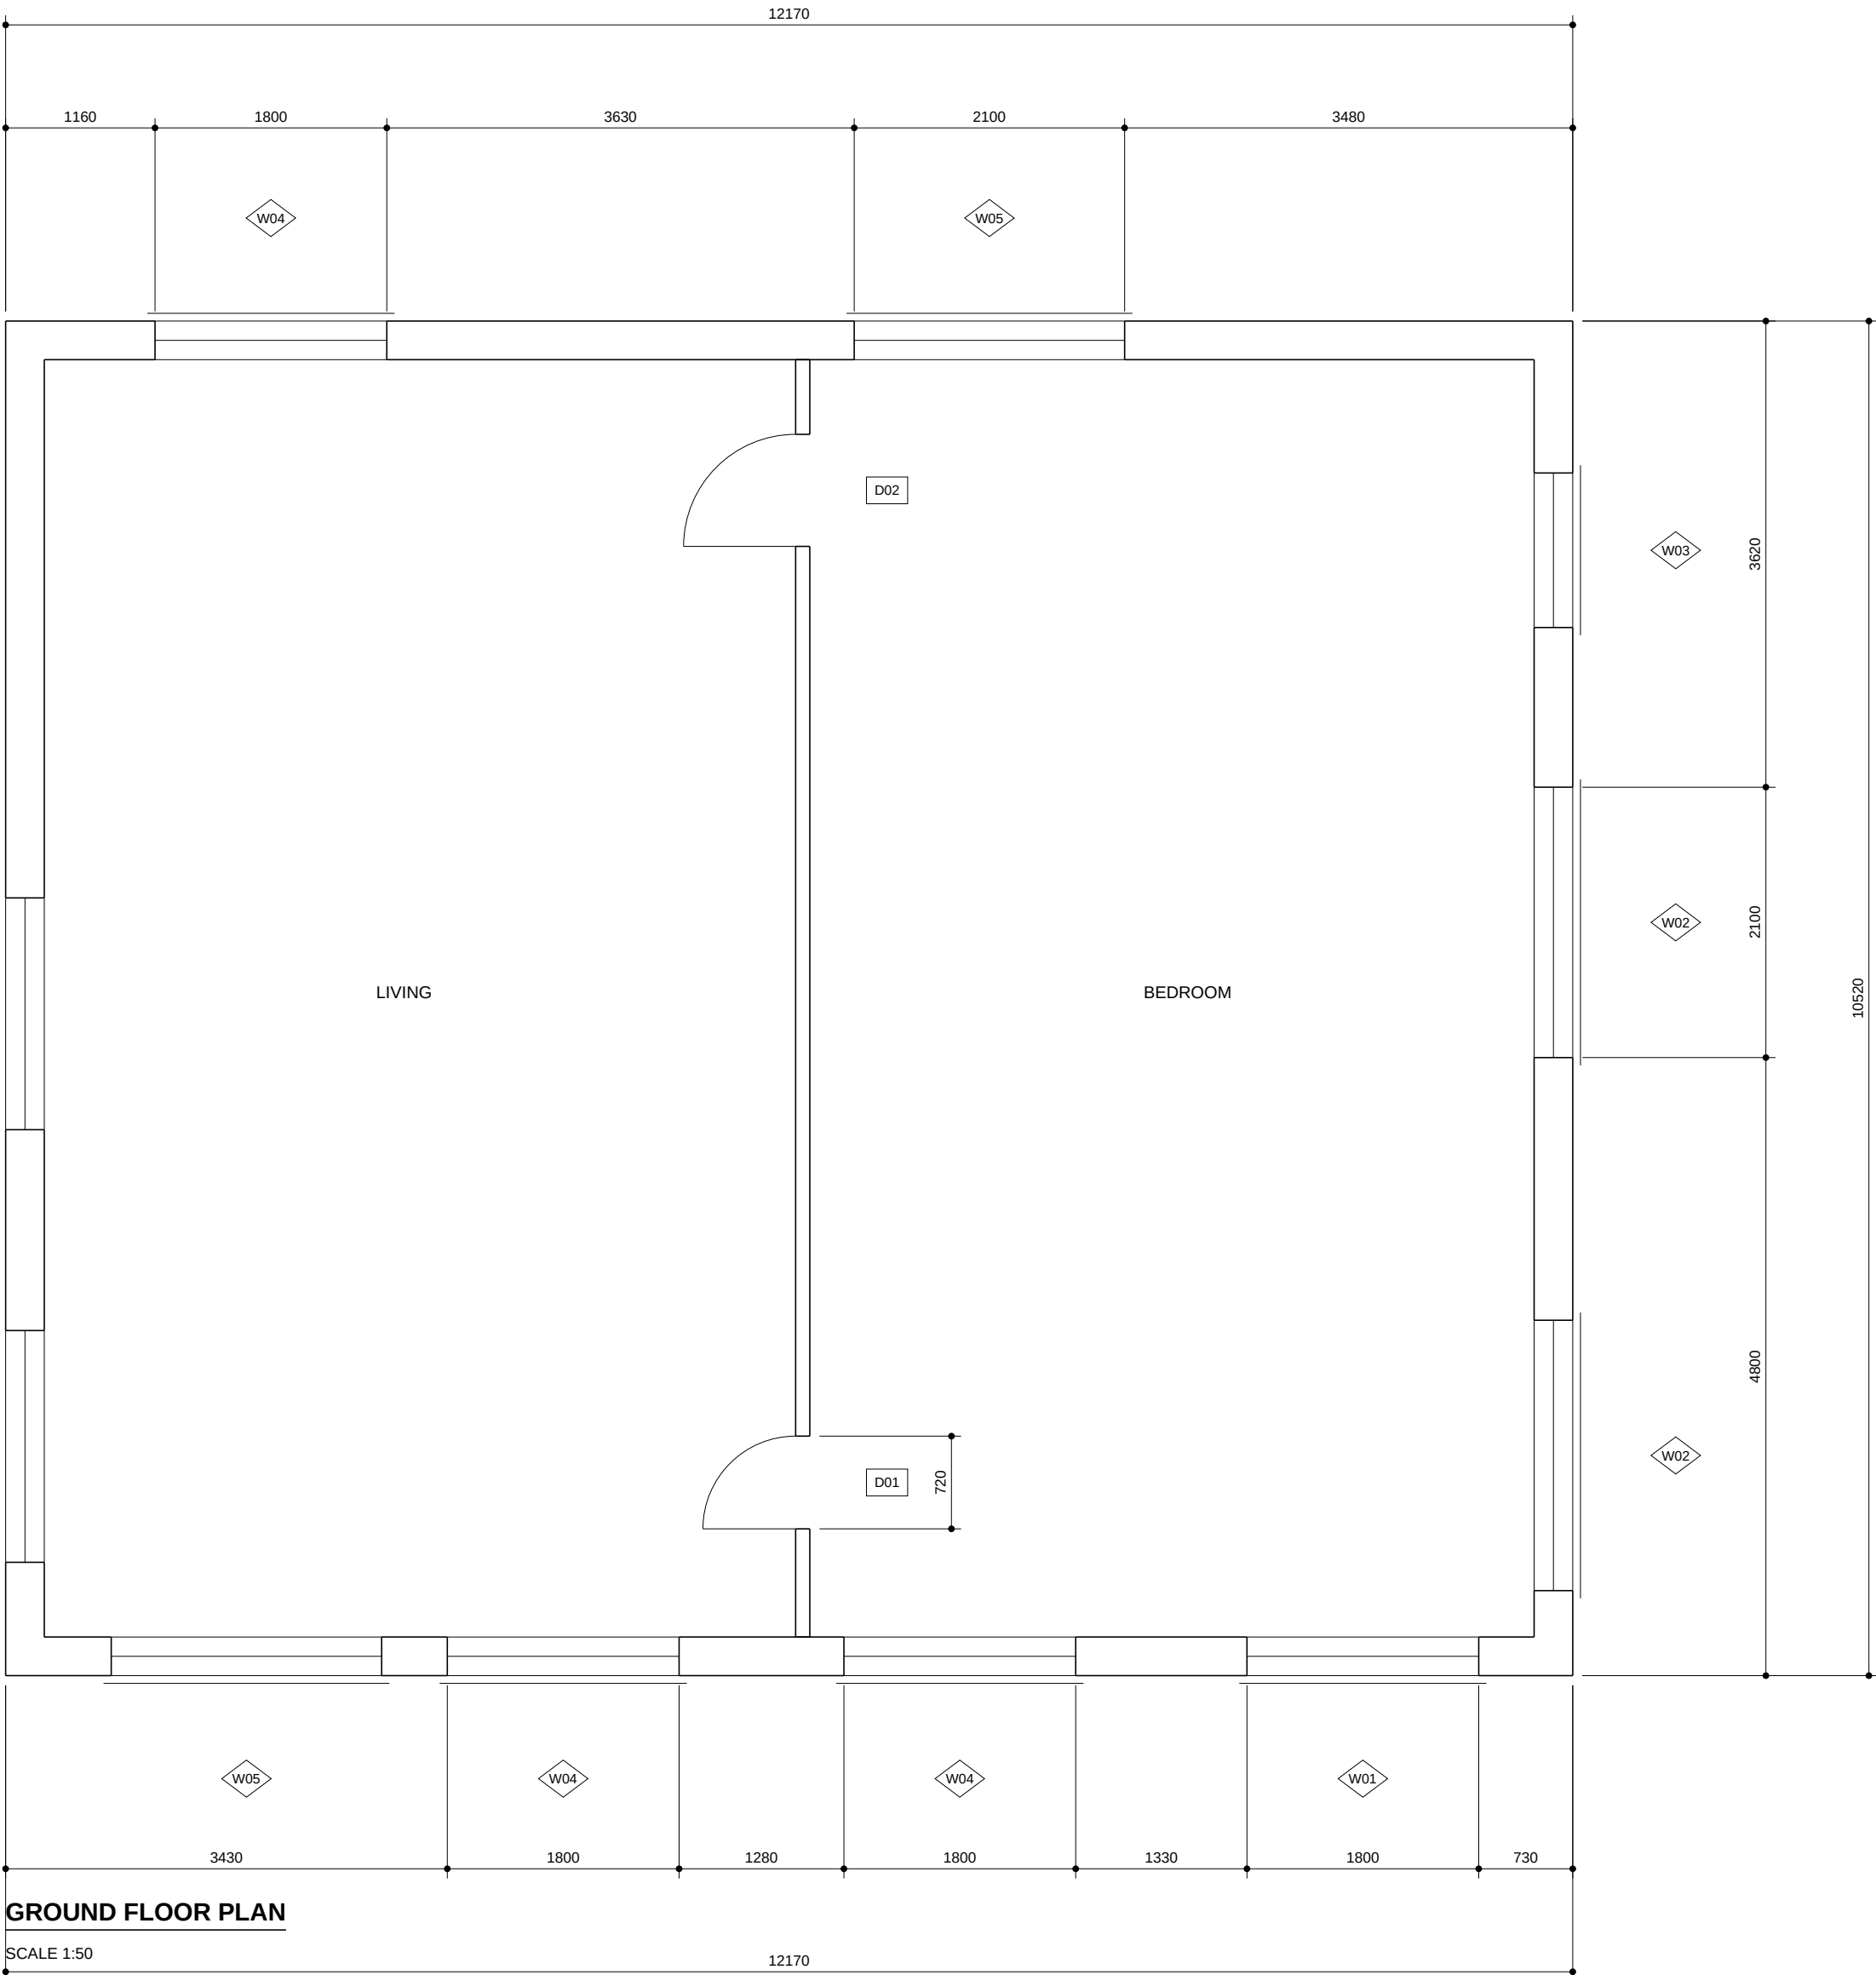


REFER TO DOOR AND WINDOW SCHEDULES ON A-601.
WINDOW TAGS SHOWN IN HEXAGONS, DOOR TAGS IN CIRCLES.

STUDIO NORTH ARCHITECTS RESIDENTIAL BUILDING LOT 33, BENCHMARK AVENUE ALL DIMENSIONS IN MILLIMETRES UNLESS NOTED OTHERWISE, DO NOT SCALE.	DRAWING TITLE GROUND FLOOR PLAN	
	SCALE 1:50	DATE 2026-09-01
	SHEET A-101	REV B

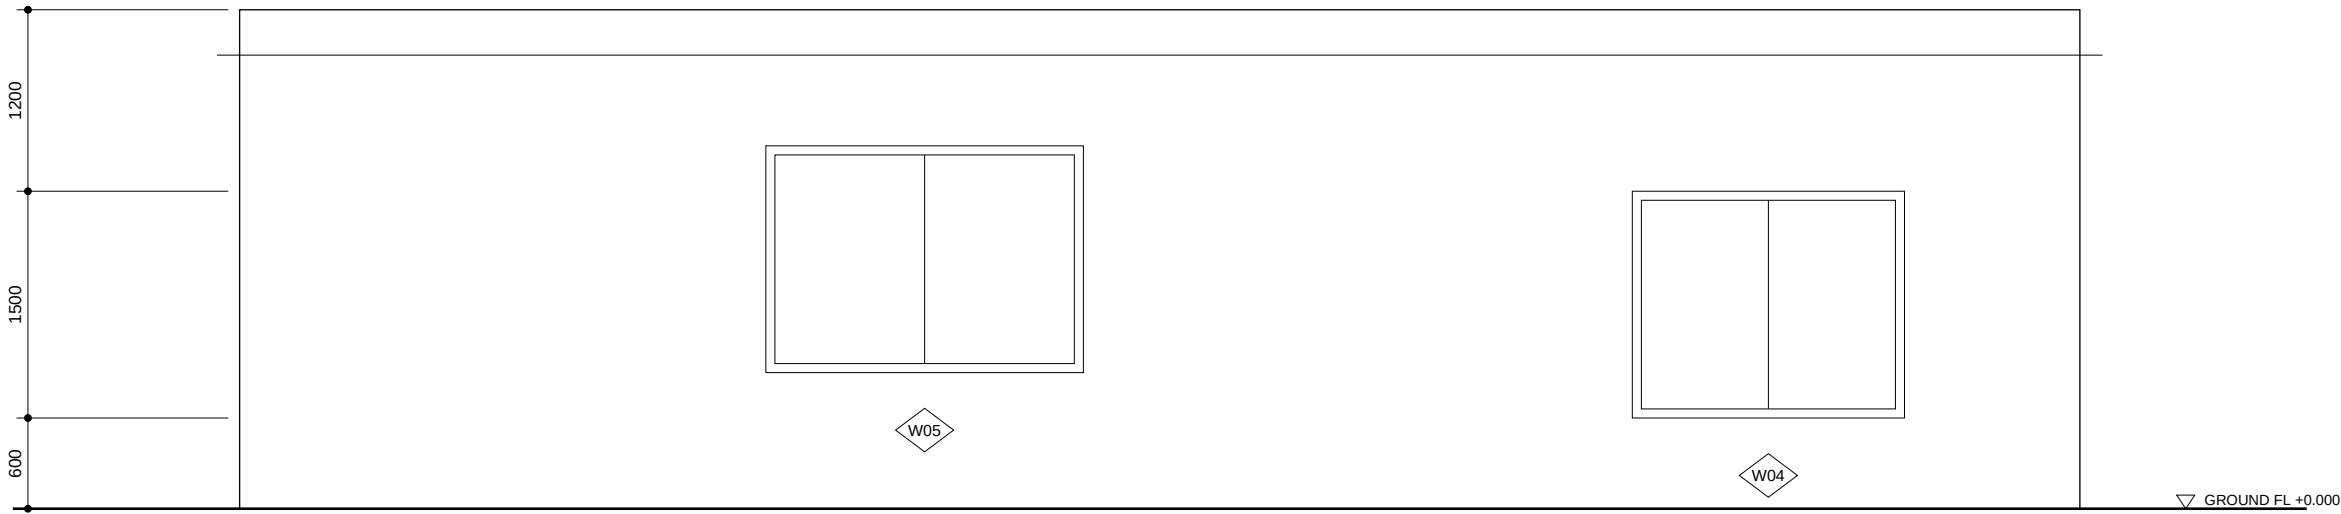

NORTH ELEVATION


SCALE 1:50

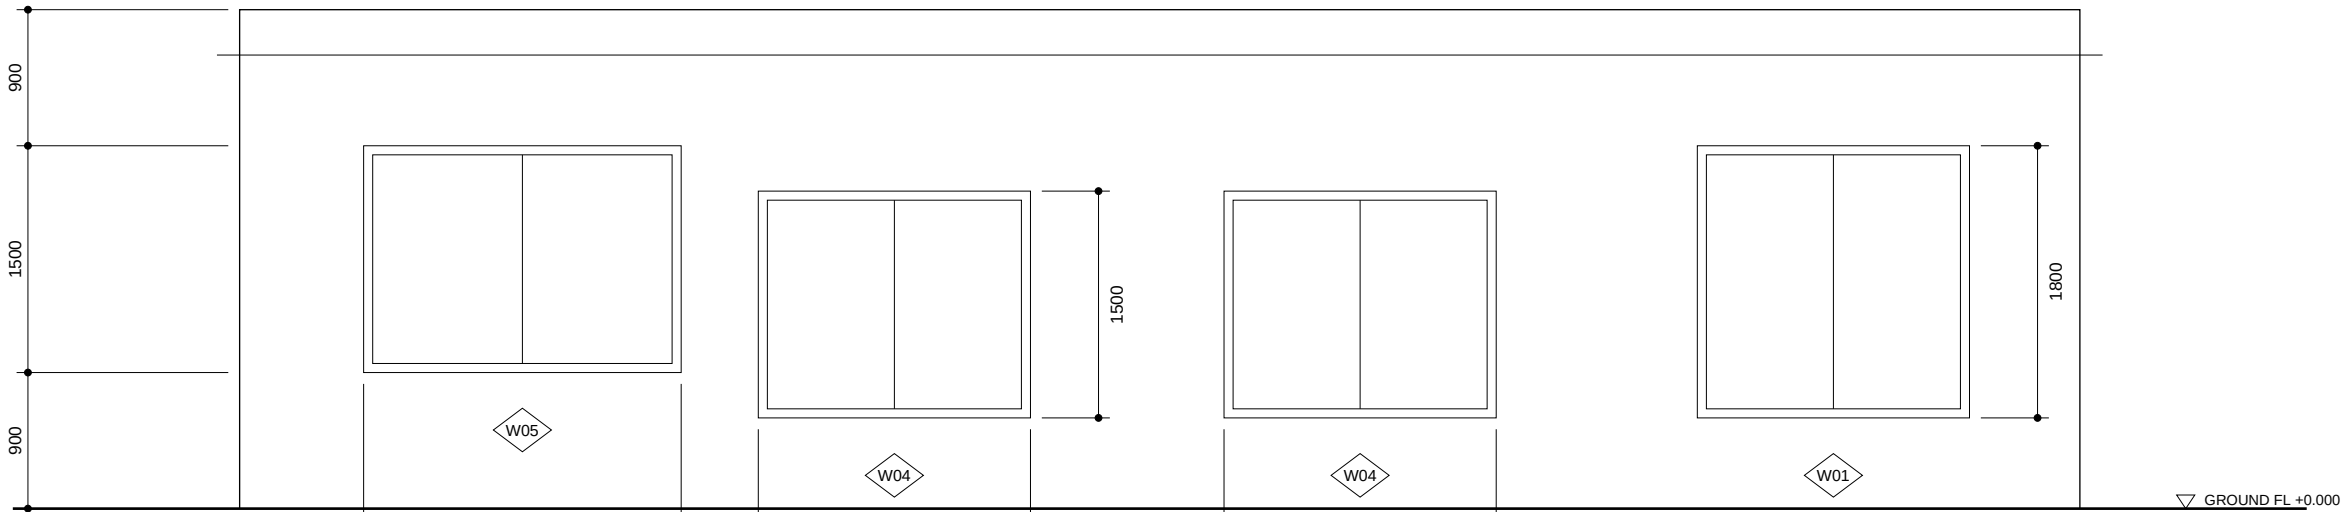

SOUTH ELEVATION


SCALE 1:50

STUDIO NORTH ARCHITECTS RESIDENTIAL BUILDING LOT 33, BENCHMARK AVENUE ALL DIMENSIONS IN MILLIMETRES UNLESS NOTED OTHERWISE, DO NOT SCALE.	DRAWING TITLE NORTH & SOUTH ELEVATIONS	
	SCALE 1:50	DATE 2026-09-01
	SHEET A-201	REV B

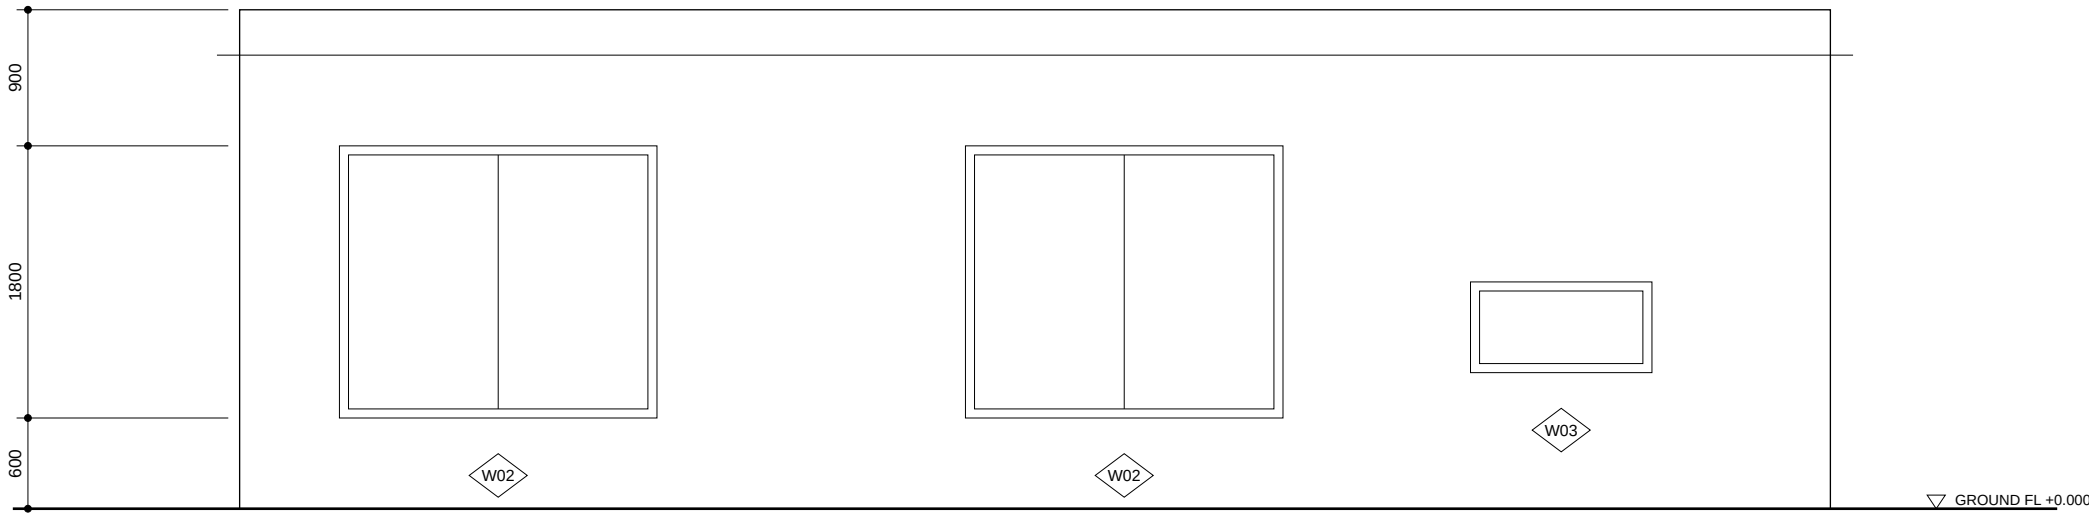

EAST ELEVATION

SCALE 1:50

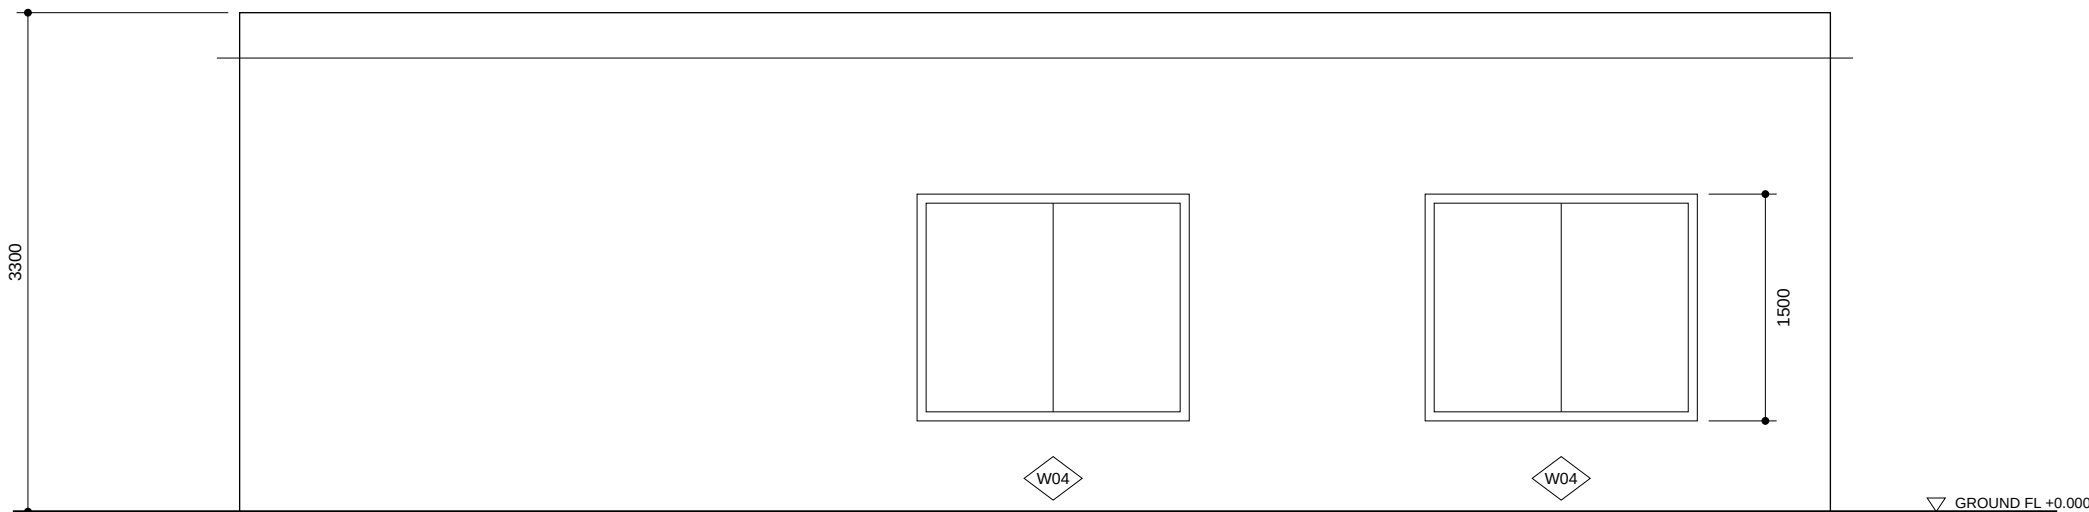

WEST ELEVATION

SCALE 1:50

STUDIO NORTH ARCHITECTS
RESIDENTIAL BUILDING
LOT 33, BENCHMARK AVENUE

ALL DIMENSIONS IN MILLIMETRES UNLESS NOTED
OTHERWISE, DO NOT SCALE.

EAST & WEST ELEVATIONS

SCALE

1:50

SHEET

A-202

DATE

2026-09-01

REV

B

DOOR SCHEDULE

MARK	TYPE	WIDTH	HEIGHT	QTY	REMARKS
D01	HINGED	720	2040	1	
D02	HINGED	870	2100	1	

WINDOW SCHEDULE

MARK	TYPE	WIDTH	HEIGHT	SILL	QTY	REMARKS
W02	AWNING	2100	1800	600	2	
W03	AWNING	1200	600	900	1	
W04	AWNING	1800	1500	600	5	
W05	AWNING	2100	1500	900	2	

NOTE: ALL SIZES ARE NOMINAL STRUCTURAL OPENING SIZES.

STUDIO NORTH ARCHITECTS RESIDENTIAL BUILDING LOT 33, BENCHMARK AVENUE ALL DIMENSIONS IN MILLIMETRES UNLESS NOTED OTHERWISE. DO NOT SCALE.	DRAWING TITLE DOOR & WINDOW SCHEDULES	
	SCALE NTS	DATE 2026-09-01
	SHEET A-601	REV B