

RESIDENTIAL BUILDING


LOT 34, BENCHMARK AVENUE

CONSTRUCTION ISSUE

DRAWING LIST


SHEET	TITLE
A-101	GROUND FLOOR PLAN
A-201	NORTH & SOUTH ELEVATIONS
A-202	EAST & WEST ELEVATIONS
A-601	DOOR & WINDOW SCHEDULES

STUDIO NORTH ARCHITECTS RESIDENTIAL BUILDING LOT 34, BENCHMARK AVENUE ALL DIMENSIONS IN MILLIMETRES UNLESS NOTED OTHERWISE, DO NOT SCALE.	DRAWING TITLE COVER SHEET	
	SCALE NTS	DATE 2026-09-01
	SHEET A-000	REV B

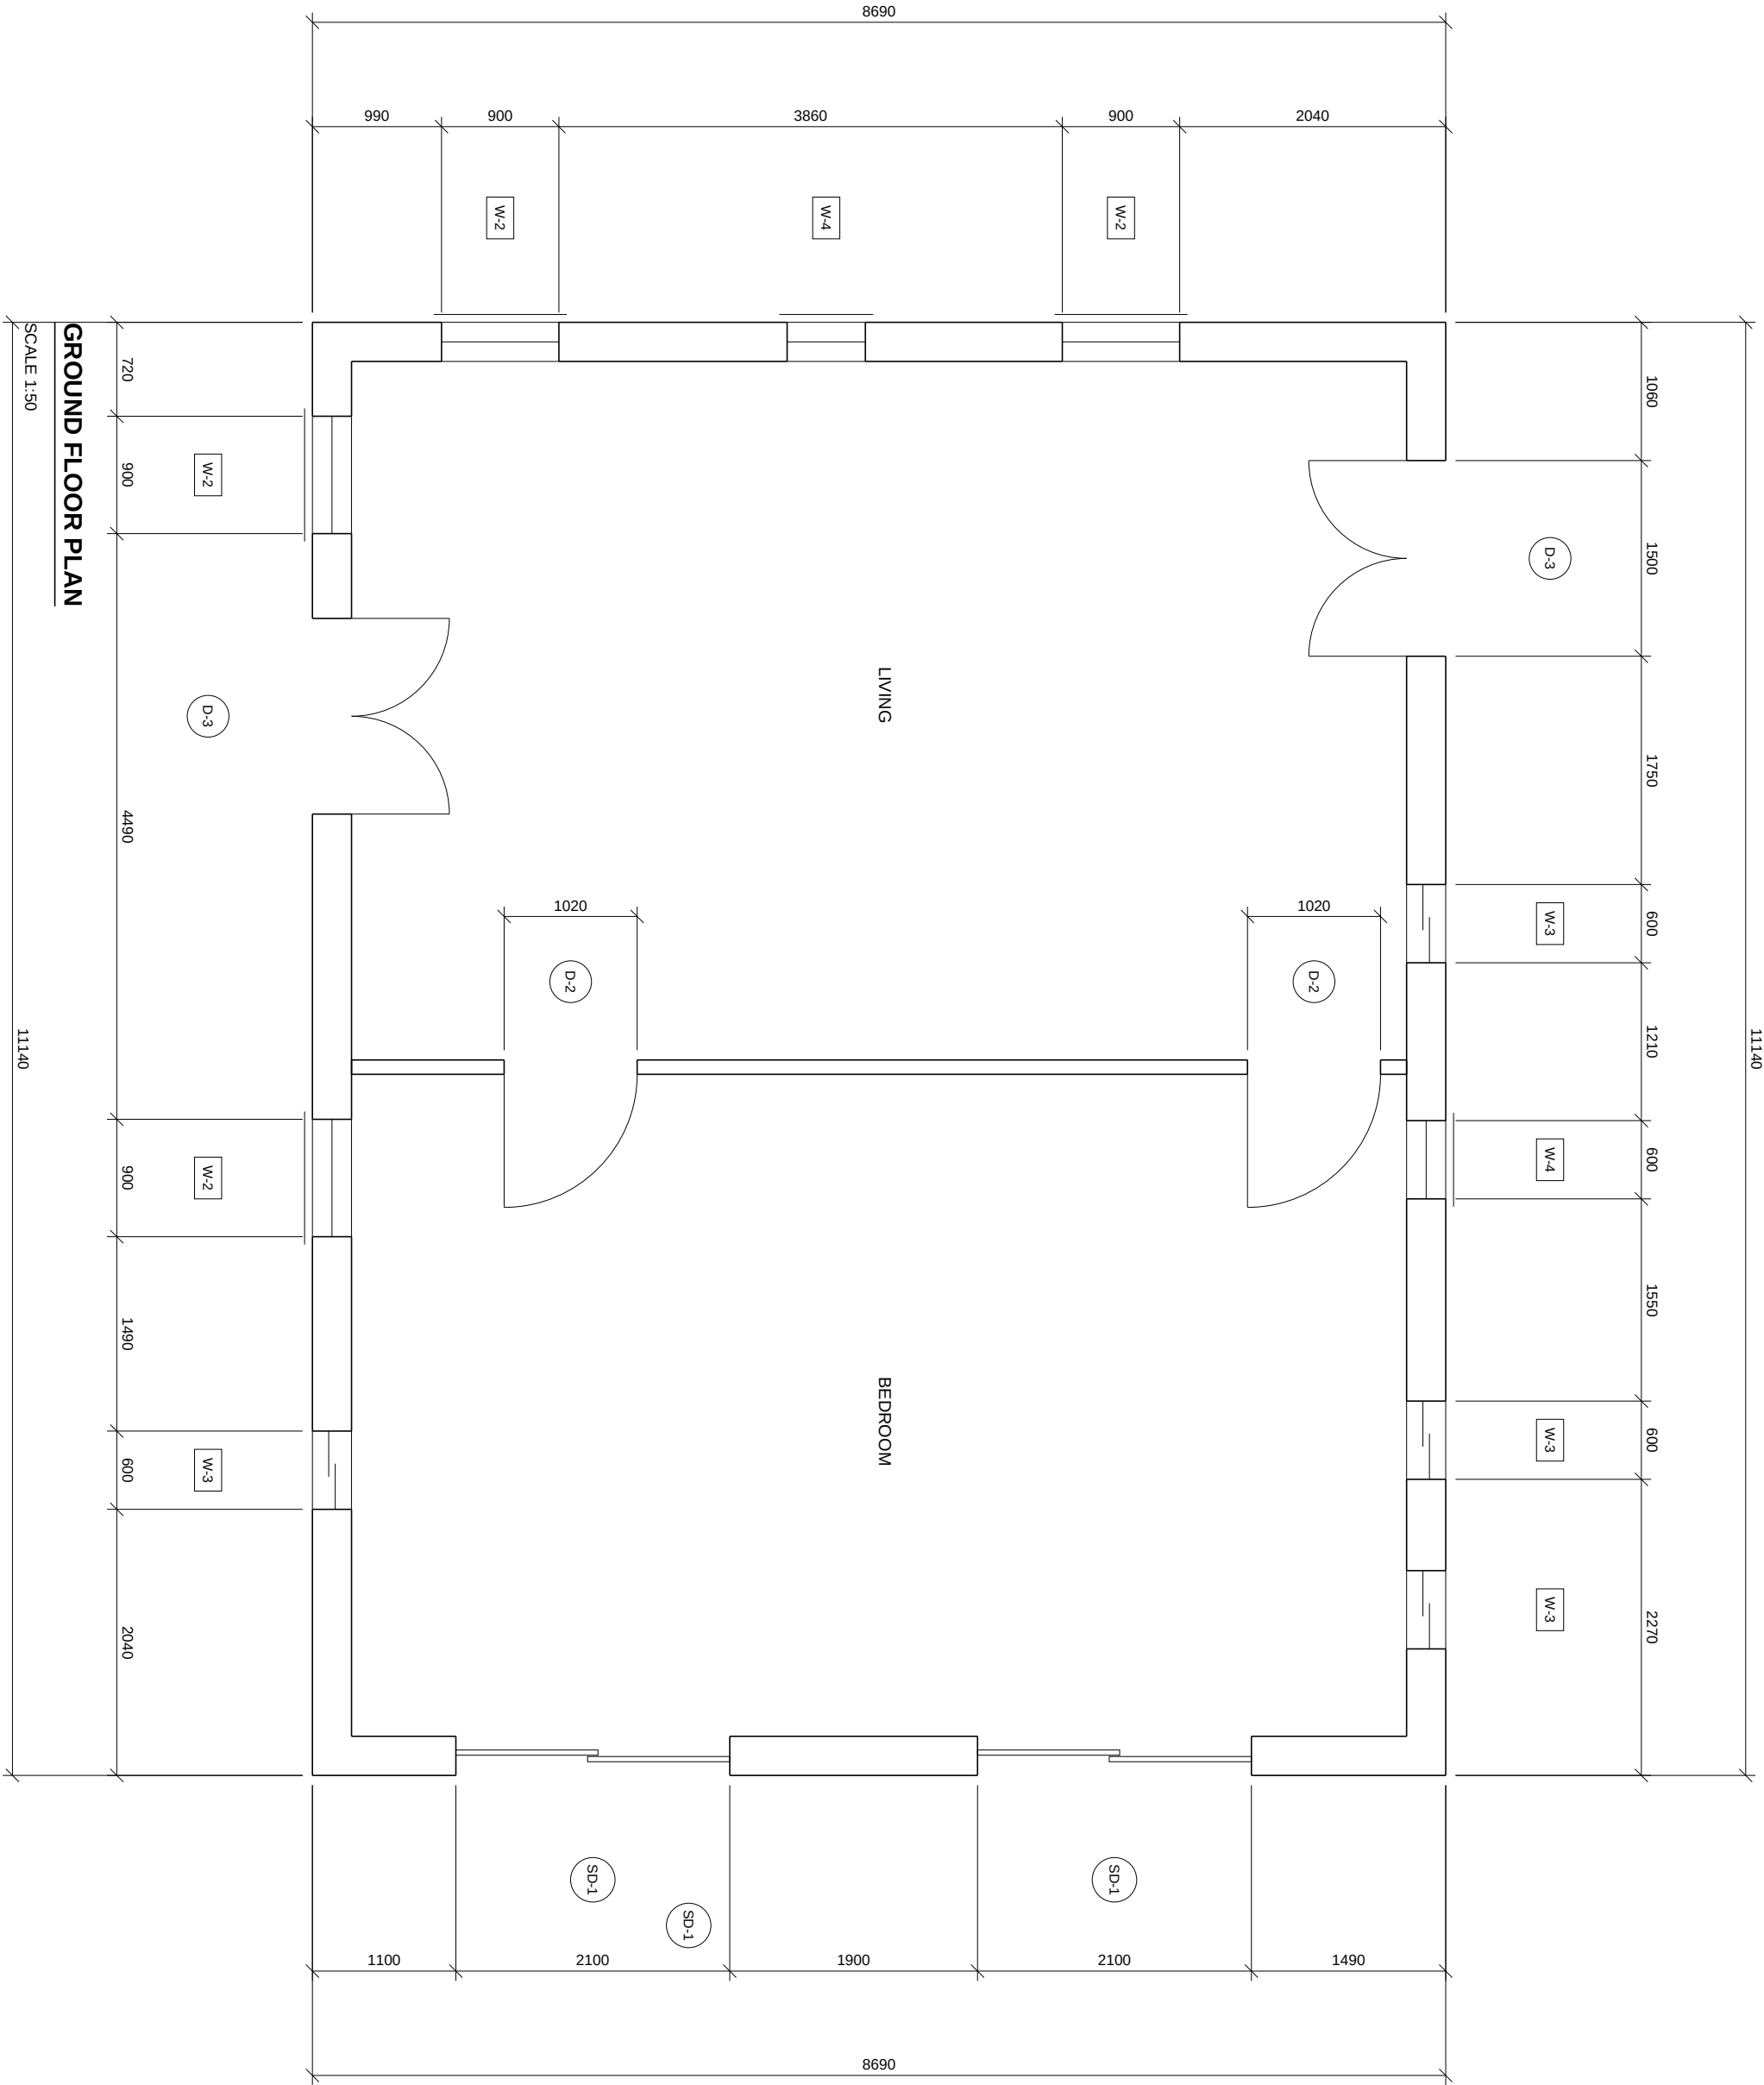


REFER TO DOOR AND WINDOW SCHEDULES ON A-601.
WINDOW TAGS SHOWN IN HEXAGONS, DOOR TAGS IN CIRCLES.

STUDIO NORTH ARCHITECTS		DRAWING TITLE	
RESIDENTIAL BUILDING		GROUND FLOOR PLAN	
LOT 34, BENCHMARK AVENUE		SCALE	DATE
ALL DIMENSIONS IN MILLIMETRES, UNLESS NOTED OTHERWISE, DO NOT SCALE.		1:50	2026-09-01
		SHEET	REV
A-101			B

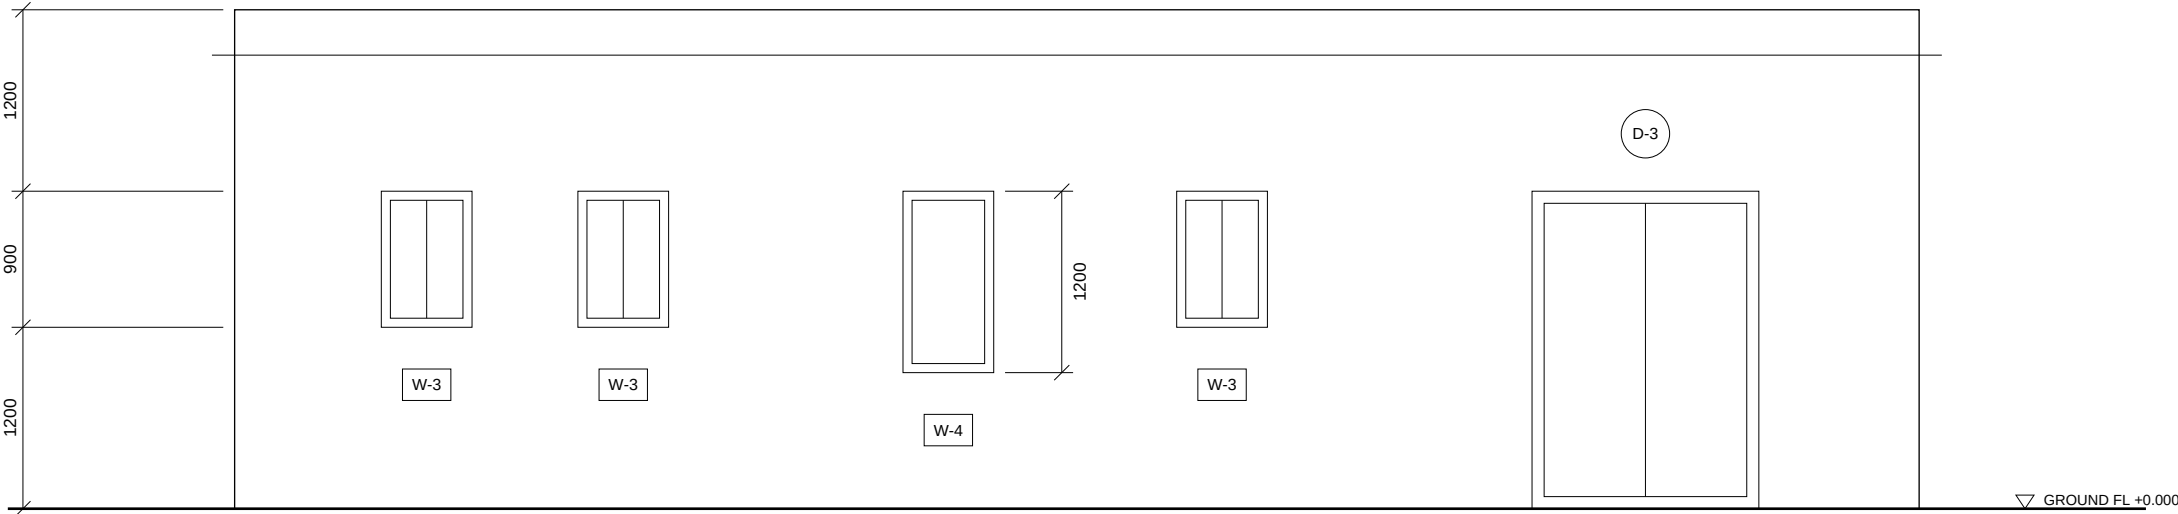

NORTH ELEVATION


SCALE 1:50

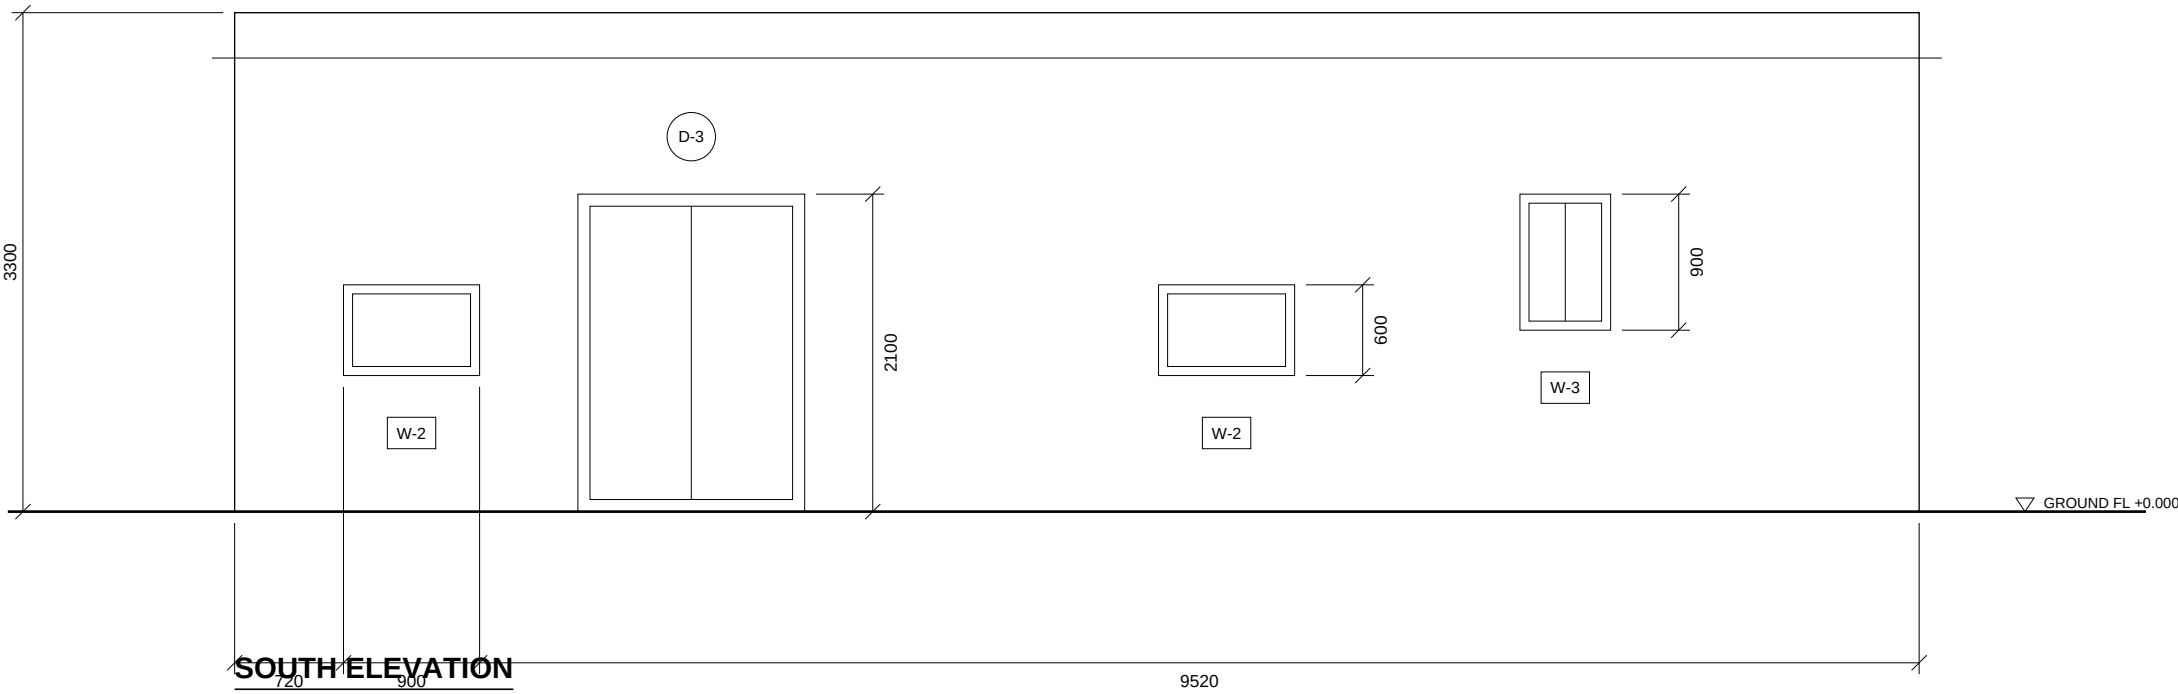

SOUTH ELEVATION


SCALE 1:50

STUDIO NORTH ARCHITECTS RESIDENTIAL BUILDING LOT 34, BENCHMARK AVENUE ALL DIMENSIONS IN MILLIMETRES UNLESS NOTED OTHERWISE, DO NOT SCALE.	DRAWING TITLE NORTH & SOUTH ELEVATIONS	
	SCALE 1:50	DATE 2026-09-01
	SHEET A-201	REV B

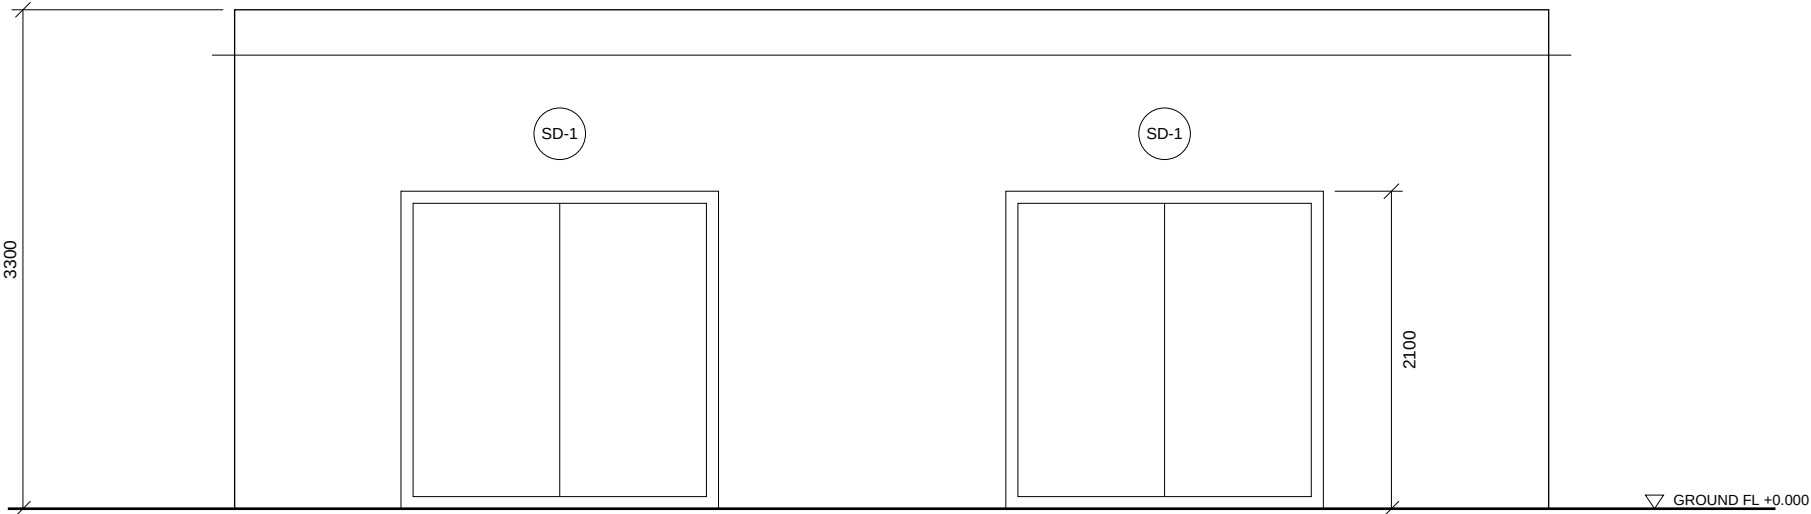

EAST ELEVATION

SCALE 1:50

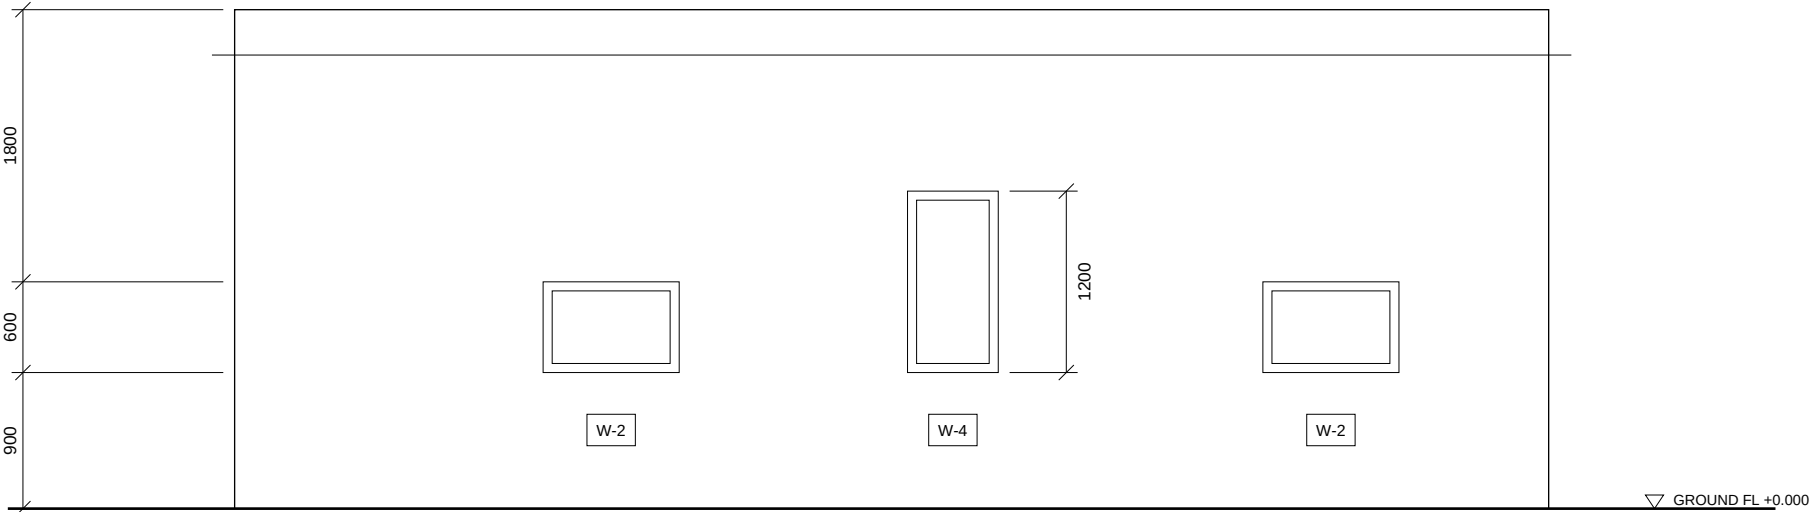

WEST ELEVATION

SCALE 1:50

STUDIO NORTH ARCHITECTS RESIDENTIAL BUILDING LOT 34, BENCHMARK AVENUE ALL DIMENSIONS IN MILLIMETRES UNLESS NOTED OTHERWISE, DO NOT SCALE.	DRAWING TITLE EAST & WEST ELEVATIONS	
	SCALE 1:50	DATE 2026-09-01
	SHEET A-202	REV B

DOOR SCHEDULE

MARK	TYPE	SIZE (W x H)	QTY	REMARKS
D-1	HINGED	920 x 2040	0	
D-2	HINGED	1020 x 2340	2	
SD-1	SLIDING DOOR	2100 x 2100	2	

WINDOW SCHEDULE

MARK	TYPE	SIZE (W x H)	SILL	QTY	REMARKS
W-1	AWNING	1200 x 600	1200	0	
W-2	AWNING	900 x 600	900	4	
W-4	AWNING	600 x 1200	900	2	

NOTE: ALL SIZES ARE NOMINAL STRUCTURAL OPENING SIZES.

STUDIO NORTH ARCHITECTS RESIDENTIAL BUILDING LOT 34, BENCHMARK AVENUE ALL DIMENSIONS IN MILLIMETRES UNLESS NOTED OTHERWISE. DO NOT SCALE.	DRAWING TITLE DOOR & WINDOW SCHEDULES	
	SCALE NTS	DATE 2026-09-01
	SHEET A-601	REV B