



REFER TO DOOR AND WINDOW SCHEDULES ON A-601.
WINDOW TAGS SHOWN IN HEXAGONS, DOOR TAGS IN CIRCLES.

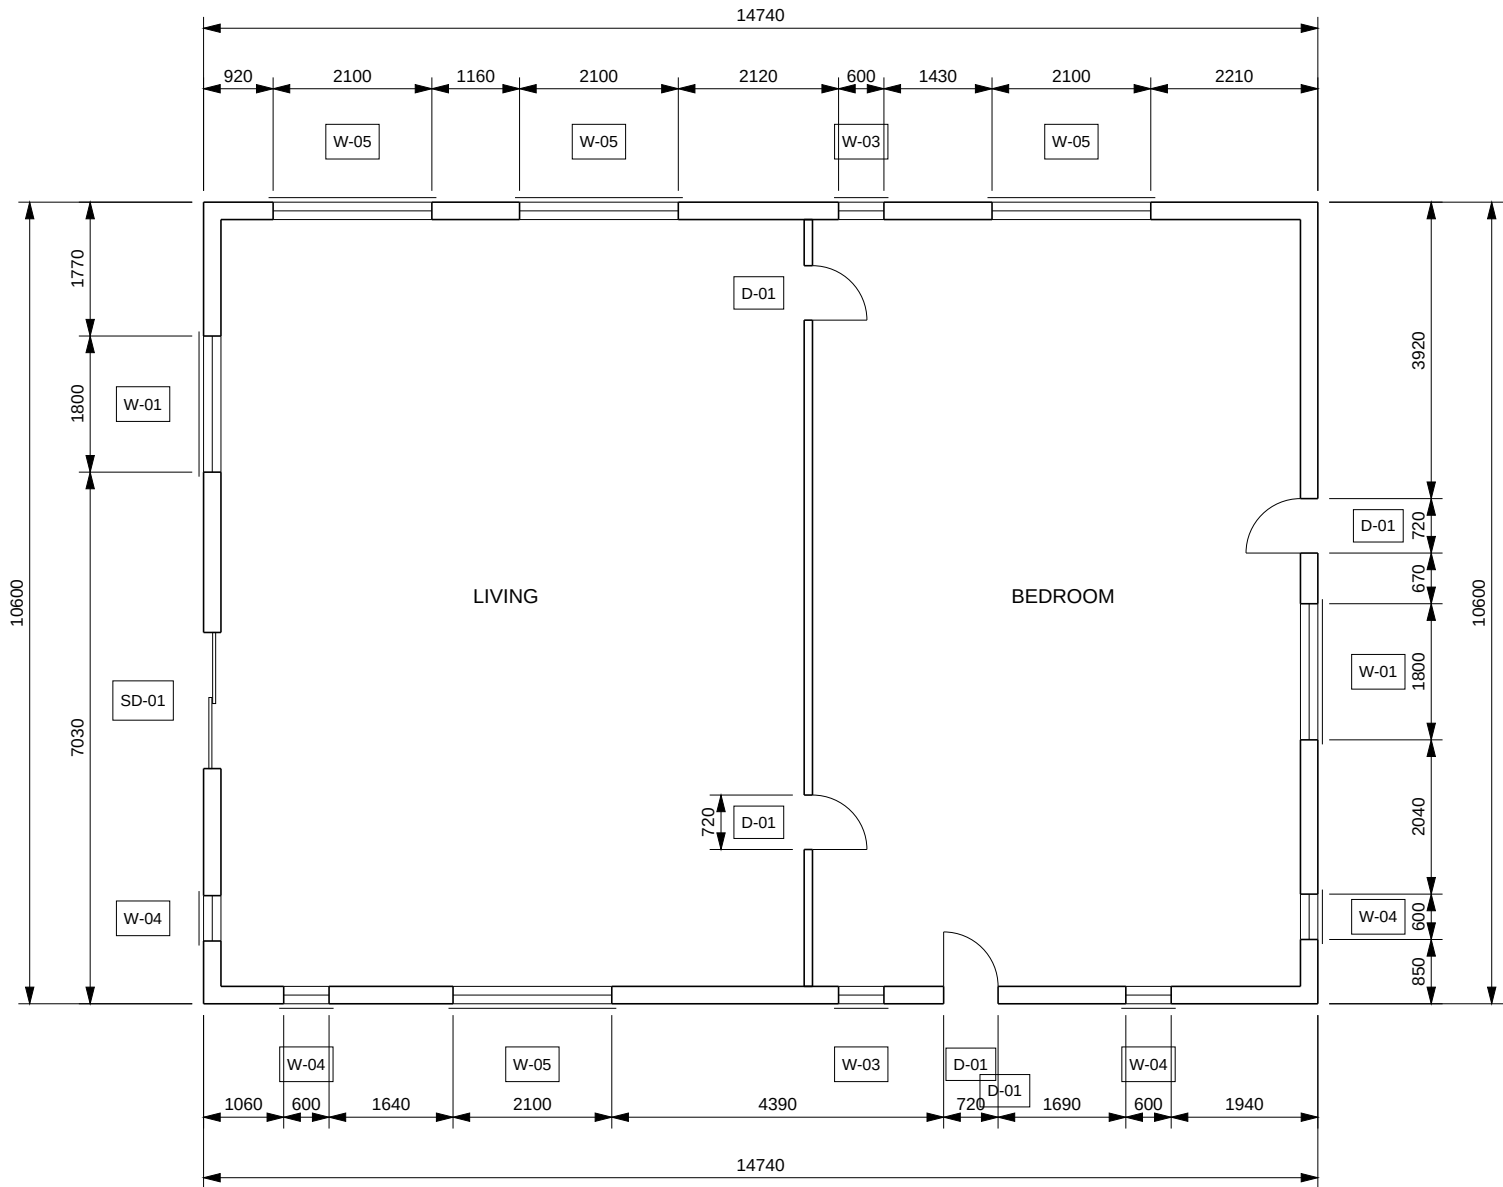

GROUND FLOOR PLAN


SCALE 1:100

STUDIO NORTH ARCHITECTS RESIDENTIAL BUILDING LOT 35, BENCHMARK AVENUE ALL DIMENSIONS IN MILLIMETRES UNLESS NOTED OTHERWISE, DO NOT SCALE.	DRAWING TITLE	
	GROUND FLOOR PLAN	
	SCALE	DATE
	1:100	2026-09-01
	SHEET	REV
	A-101	B

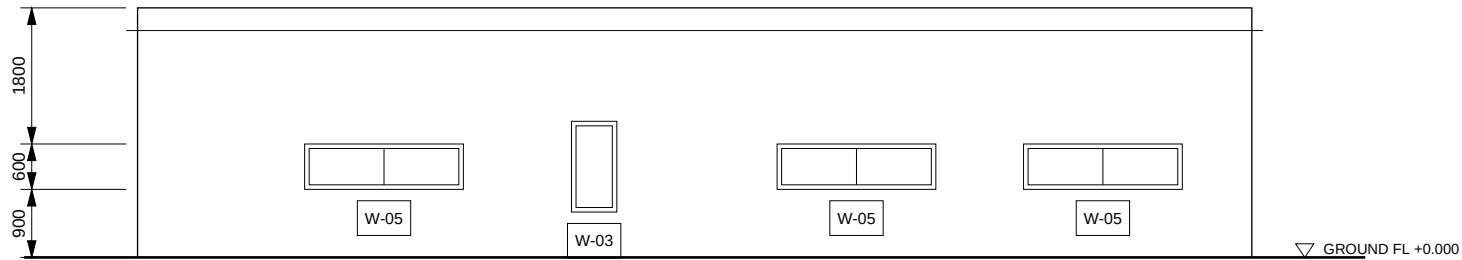

NORTH ELEVATION


SCALE 1:100

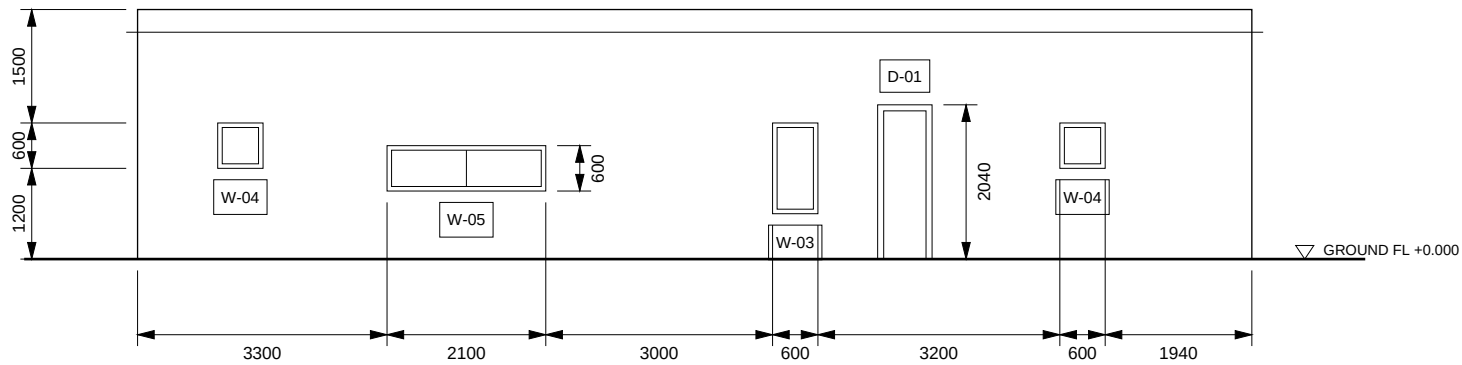

SOUTH ELEVATION


SCALE 1:100

STUDIO NORTH ARCHITECTS RESIDENTIAL BUILDING LOT 35, BENCHMARK AVENUE ALL DIMENSIONS IN MILLIMETRES UNLESS NOTED OTHERWISE, DO NOT SCALE.	DRAWING TITLE	
	NORTH & SOUTH ELEVATIONS	
	SCALE	DATE
	1:100	2026-09-01
	SHEET	REV
	A-201	B

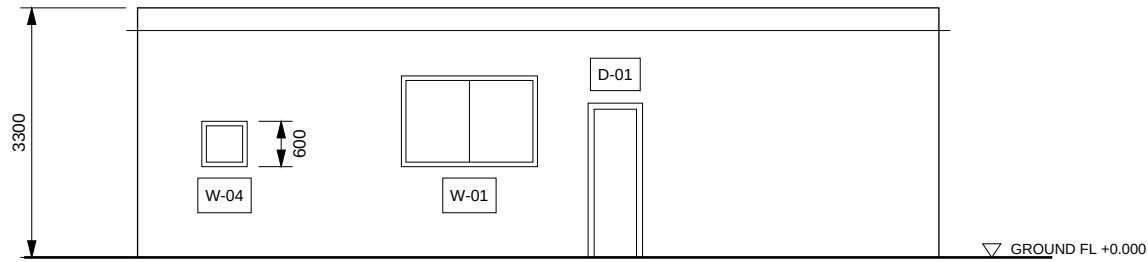

EAST ELEVATION

SCALE 1:100

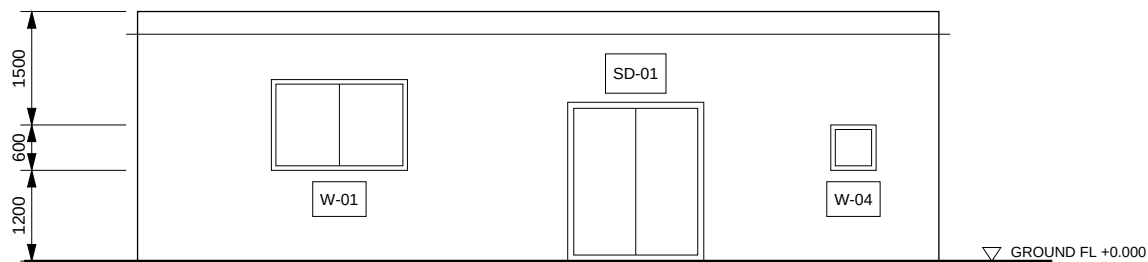

WEST ELEVATION

SCALE 1:100

STUDIO NORTH ARCHITECTS

RESIDENTIAL BUILDING

LOT 35, BENCHMARK AVENUE

ALL DIMENSIONS IN MILLIMETRES UNLESS NOTED
OTHERWISE. DO NOT SCALE.

DRAWING TITLE

EAST & WEST ELEVATIONS

SCALE

1:100

SHEET

A-202

DATE

2026-09-01

REV

B

DOOR SCHEDULE

MARK	TYPE	WIDTH	HEIGHT	QTY	REMARKS
D-02	HINGED	870	2040	0	
SD-01	SLIDING DOOR	1800	2100	1	

WINDOW SCHEDULE

MARK	TYPE	WIDTH	HEIGHT	SILL	QTY	REMARKS
W-01	AWNING	1800	1200	1200	2	
W-02	AWNING	2100	1800	600	0	
W-03	AWNING	600	1200	600	2	
W-04	AWNING	600	600	1200	4	
W-05	AWNING	2100	600	900	4	

NOTE: ALL SIZES ARE NOMINAL STRUCTURAL OPENING SIZES.

STUDIO NORTH ARCHITECTS RESIDENTIAL BUILDING LOT 35, BENCHMARK AVENUE ALL DIMENSIONS IN MILLIMETRES UNLESS NOTED OTHERWISE. DO NOT SCALE.	DRAWING TITLE DOOR & WINDOW SCHEDULES	
	SCALE NTS	DATE 2026-09-01
	SHEET A-601	REV B