

RESIDENTIAL BUILDING


14 HARBOUR STREET, NORTHBRIDGE

CONSTRUCTION ISSUE

DRAWING LIST

SHEET	TITLE
A-001	SITE PLAN
A-002	GENERAL NOTES
A-101	GROUND FLOOR PLAN
A-102	FIRST FLOOR PLAN
A-201	NORTH & SOUTH ELEVATIONS
A-202	EAST & WEST ELEVATIONS
A-301	SECTION A-A
A-501	ENLARGED BATHROOM PLAN
A-601	DOOR & WINDOW SCHEDULES

STUDIO NORTH ARCHITECTS RESIDENTIAL BUILDING 14 HARBOUR STREET, NORTHBRIDGE ALL DIMENSIONS IN MILLIMETRES UNLESS NOTED OTHERWISE. DO NOT SCALE.	DRAWING TITLE COVER SHEET	
	SCALE NTS	DATE 2026-09-01
	SHEET A-000	REV B

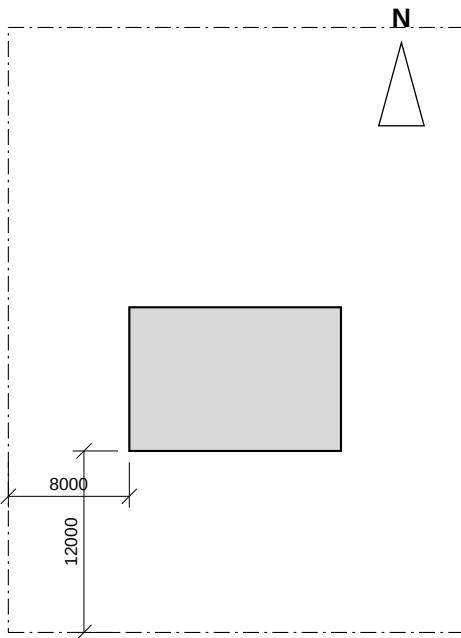

SITE PLAN

SCALE 1:500

STUDIO NORTH ARCHITECTS RESIDENTIAL BUILDING 14 HARBOUR STREET, NORTHBRIDGE ALL DIMENSIONS IN MILLIMETRES UNLESS NOTED OTHERWISE, DO NOT SCALE.	DRAWING TITLE SITE PLAN	
	SCALE 1:500	DATE 2026-09-01
	SHEET A-001	REV B


GENERAL NOTES

- 1. THESE DRAWINGS SHALL BE READ IN CONJUNCTION WITH ALL SPECIFICATIONS.
- 2. CONTRACTOR TO VERIFY ALL DIMENSIONS ON SITE PRIOR TO COMMENCEMENT.
- 3. ALL WINDOWS TO COMPLY WITH THE ENERGY EFFICIENCY REQUIREMENTS.
- 4. GLAZING TO BATHROOMS TO BE OBSCURE GLASS.
- 5. SMOKE ALARMS TO BE INSTALLED IN ACCORDANCE WITH THE BUILDING CODE.
- 6. WET AREAS TO BE WATERPROOFED TO THE RELEVANT STANDARD.
- 7. ALL TIMBER FRAMING TO BE TERMITE RESISTANT.
- 8. REFER TO STRUCTURAL ENGINEER'S DRAWINGS FOR ALL FOOTING DETAILS.

SPECIFICATION SUMMARY

STUDIO NORTH ARCHITECTS RESIDENTIAL BUILDING 14 HARBOUR STREET, NORTHBRIDGE ALL DIMENSIONS IN MILLIMETRES UNLESS NOTED OTHERWISE. DO NOT SCALE.	DRAWING TITLE GENERAL NOTES	
	SCALE NTS	DATE 2026-09-01
	SHEET A-002	REV B

REFER TO DOOR AND WINDOW SCHEDULES ON A-601.
WINDOW TAGS SHOWN IN HEXAGONS, DOOR TAGS IN CIRCLES.

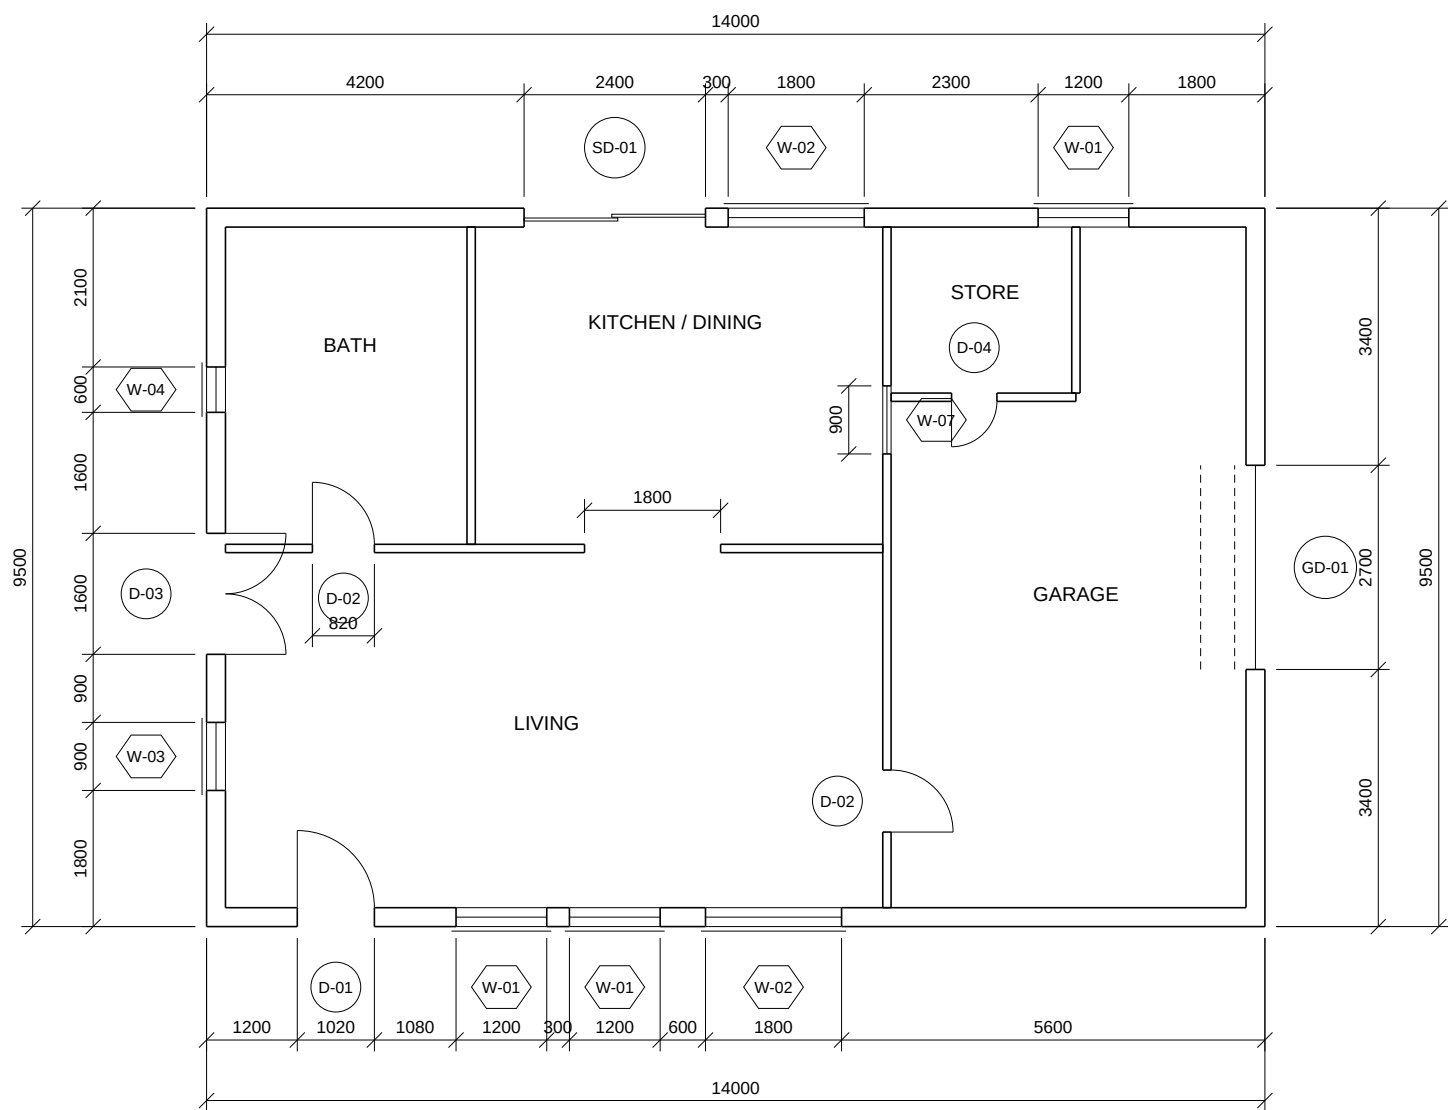


GROUND FLOOR PLAN

SCALE 1:100

STUDIO NORTH ARCHITECTS RESIDENTIAL BUILDING 14 HARBOUR STREET, NORTHBRIDGE ALL DIMENSIONS IN MILLIMETRES UNLESS NOTED OTHERWISE, DO NOT SCALE.	DRAWING TITLE GROUND FLOOR PLAN	
	SCALE 1:100	DATE 2026-09-01
	SHEET A-101	REV B


REFER TO DOOR AND WINDOW SCHEDULES ON A-601.
WINDOW TAGS SHOWN IN HEXAGONS, DOOR TAGS IN CIRCLES.

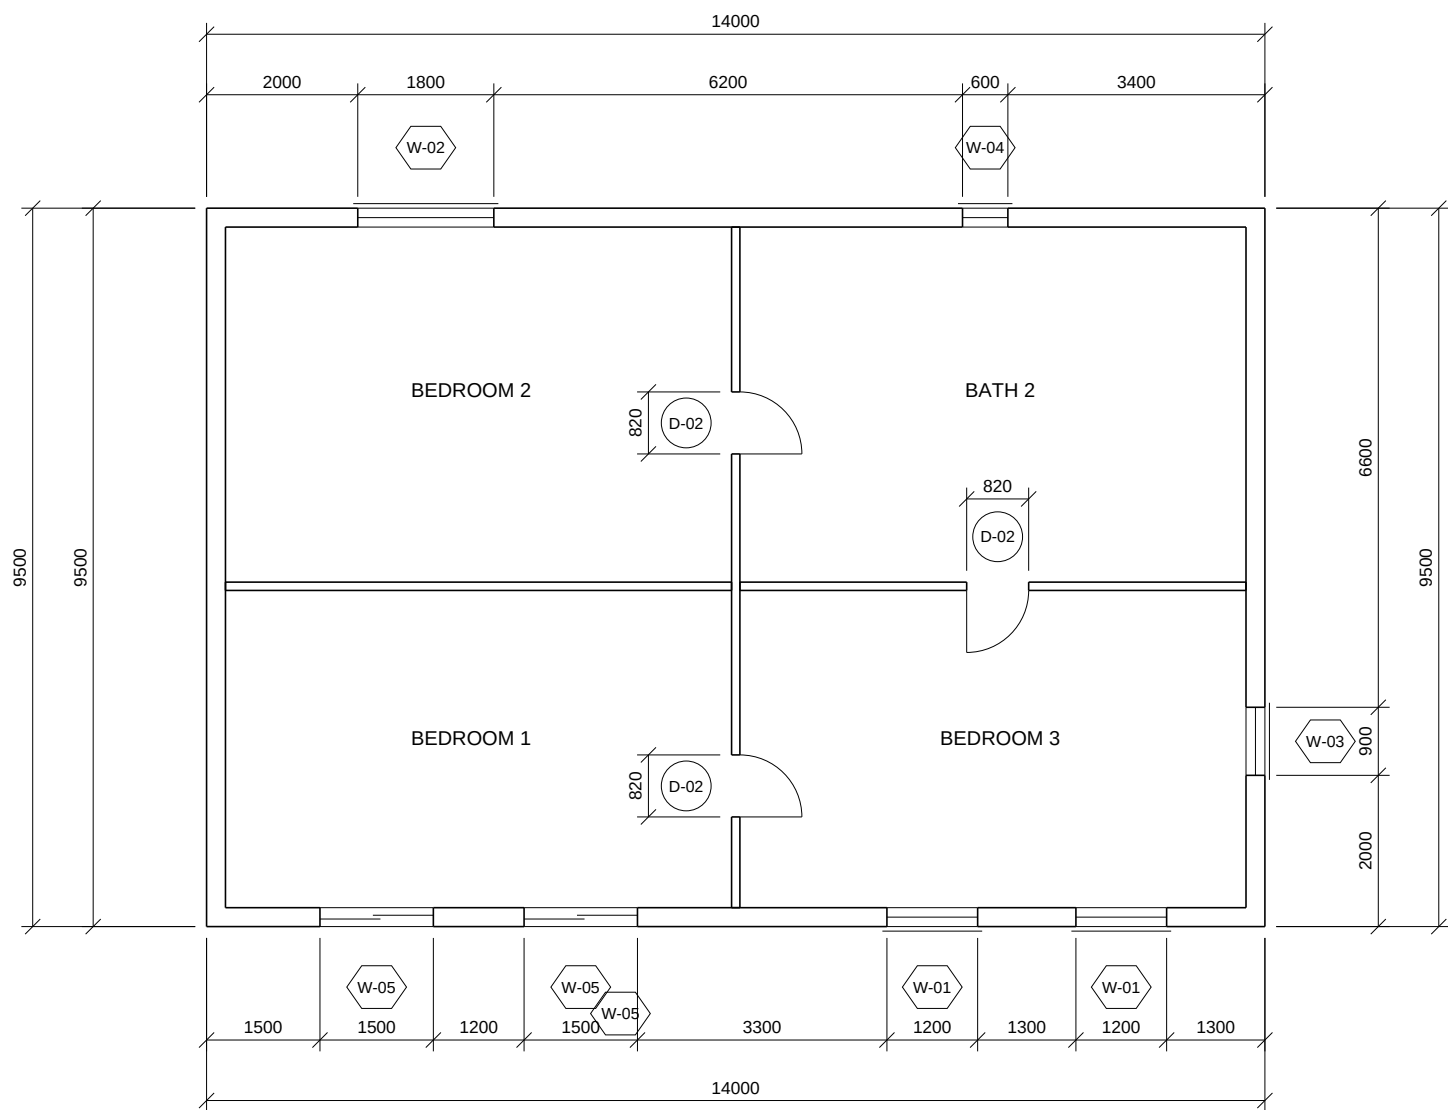

FIRST FLOOR PLAN


SCALE 1:100

STUDIO NORTH ARCHITECTS RESIDENTIAL BUILDING 14 HARBOUR STREET, NORTHBRIDGE ALL DIMENSIONS IN MILLIMETRES UNLESS NOTED OTHERWISE. DO NOT SCALE.	DRAWING TITLE	
	FIRST FLOOR PLAN	
	SCALE	DATE
	1:100	2026-09-01
	SHEET	REV
	A-102	B

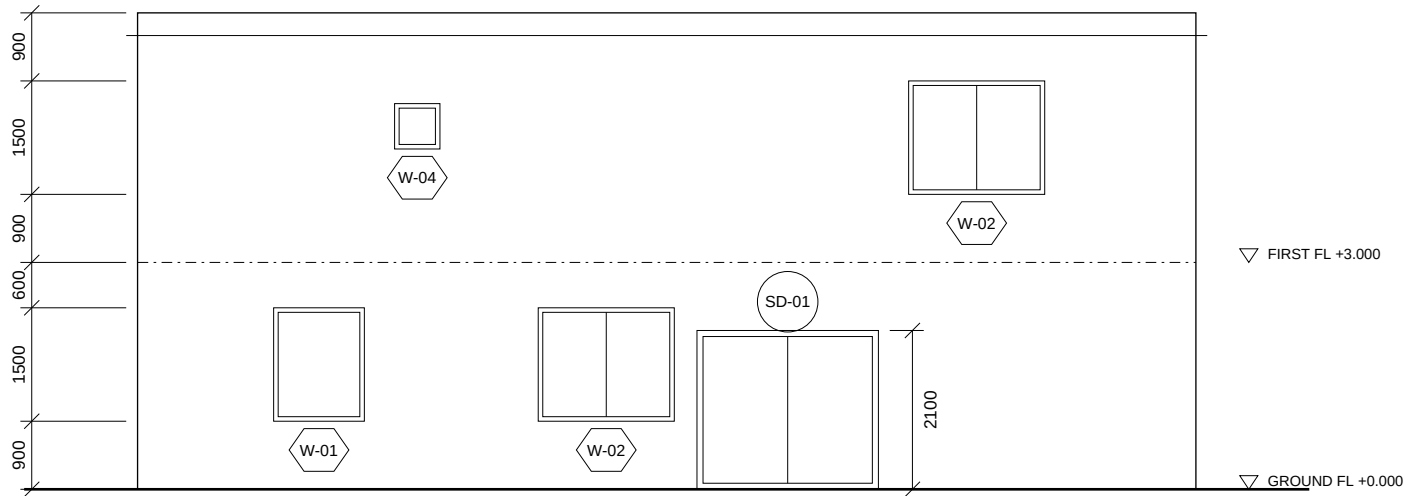

NORTH ELEVATION


SCALE 1:100

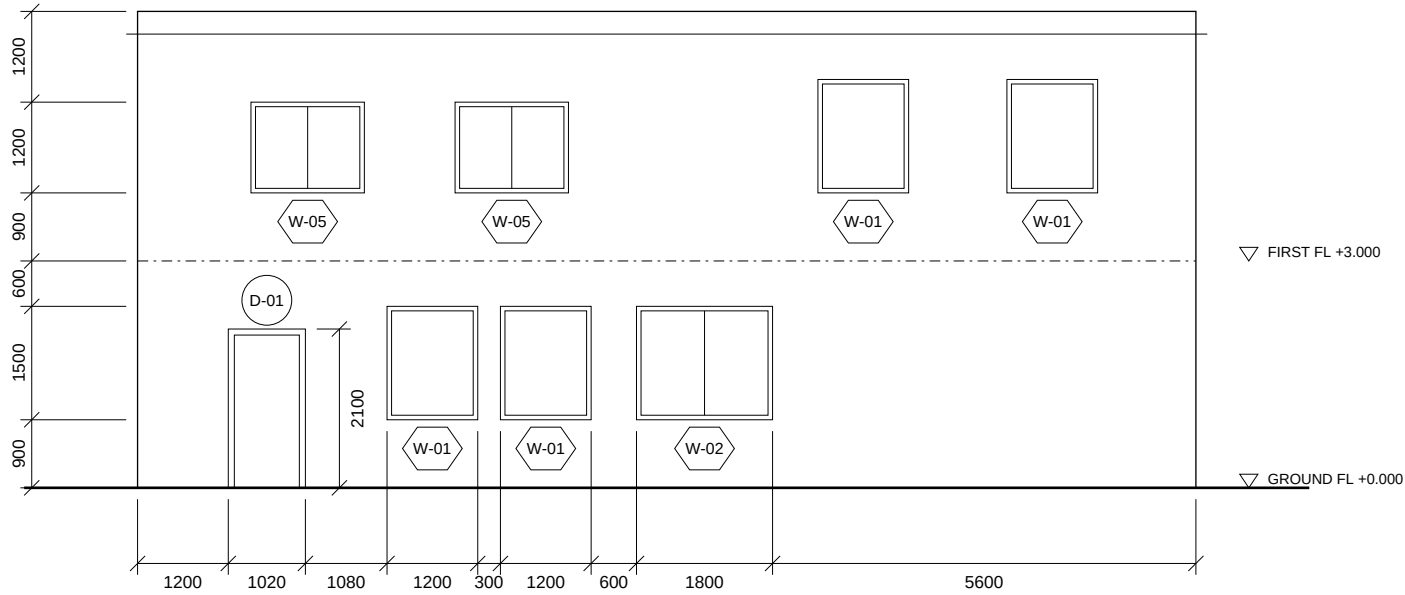

SOUTH ELEVATION


SCALE 1:100

STUDIO NORTH ARCHITECTS RESIDENTIAL BUILDING 14 HARBOUR STREET, NORTHBRIDGE ALL DIMENSIONS IN MILLIMETRES UNLESS NOTED OTHERWISE. DO NOT SCALE.	DRAWING TITLE NORTH & SOUTH ELEVATIONS	
	SCALE 1:100	DATE 2026-09-01
	SHEET A-201	REV B

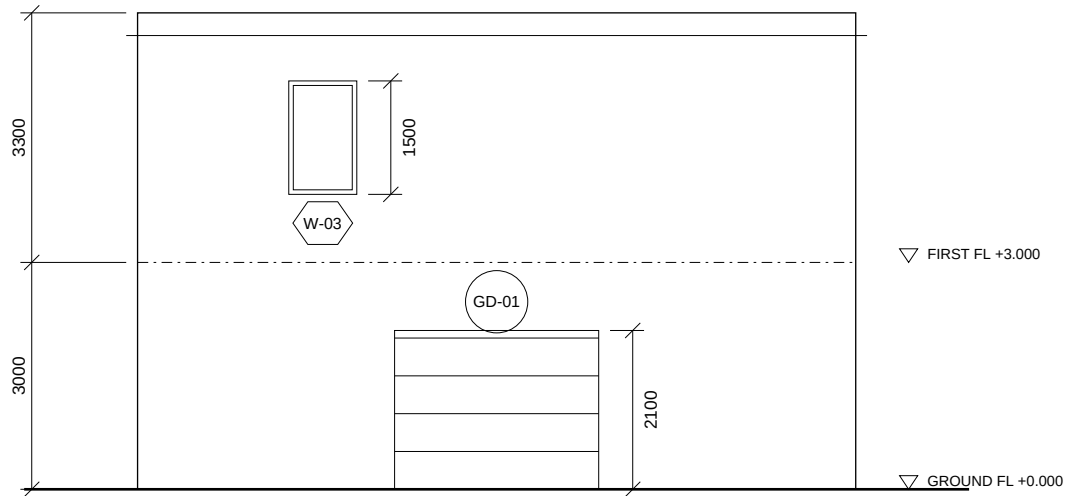

EAST ELEVATION

SCALE 1:100

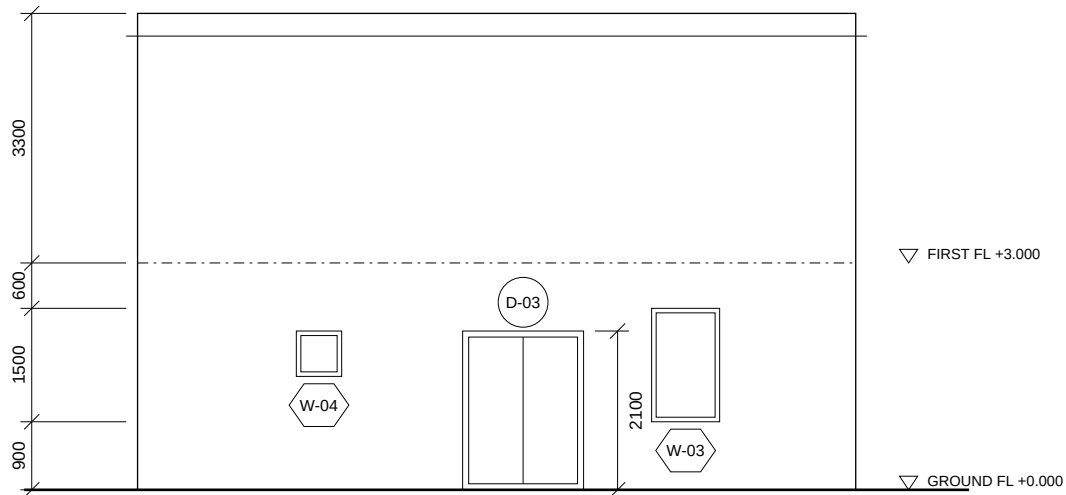

WEST ELEVATION

SCALE 1:100

STUDIO NORTH ARCHITECTS

RESIDENTIAL BUILDING

14 HARBOUR STREET, NORTHBRIDGE

ALL DIMENSIONS IN MILLIMETRES UNLESS NOTED
OTHERWISE. DO NOT SCALE.

DRAWING TITLE

EAST & WEST ELEVATIONS

SCALE

1:100

DATE


2026-09-01

SHEET

A-202

REV


B

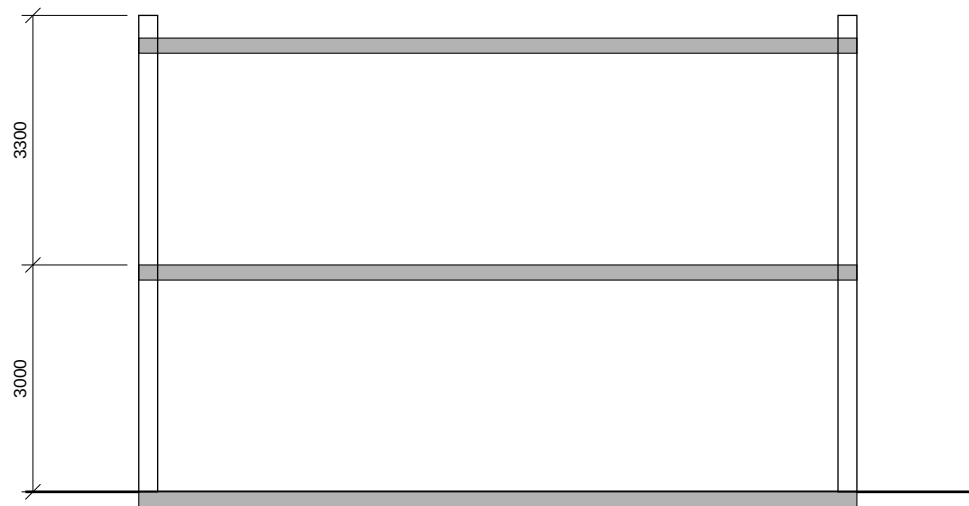

SECTION A-A

SCALE 1:100

STUDIO NORTH ARCHITECTS RESIDENTIAL BUILDING 14 HARBOUR STREET, NORTHBRIDGE ALL DIMENSIONS IN MILLIMETRES UNLESS NOTED OTHERWISE. DO NOT SCALE.	DRAWING TITLE SECTION A-A	
	SCALE 1:100	DATE 2026-09-01
	SHEET A-301	REV B

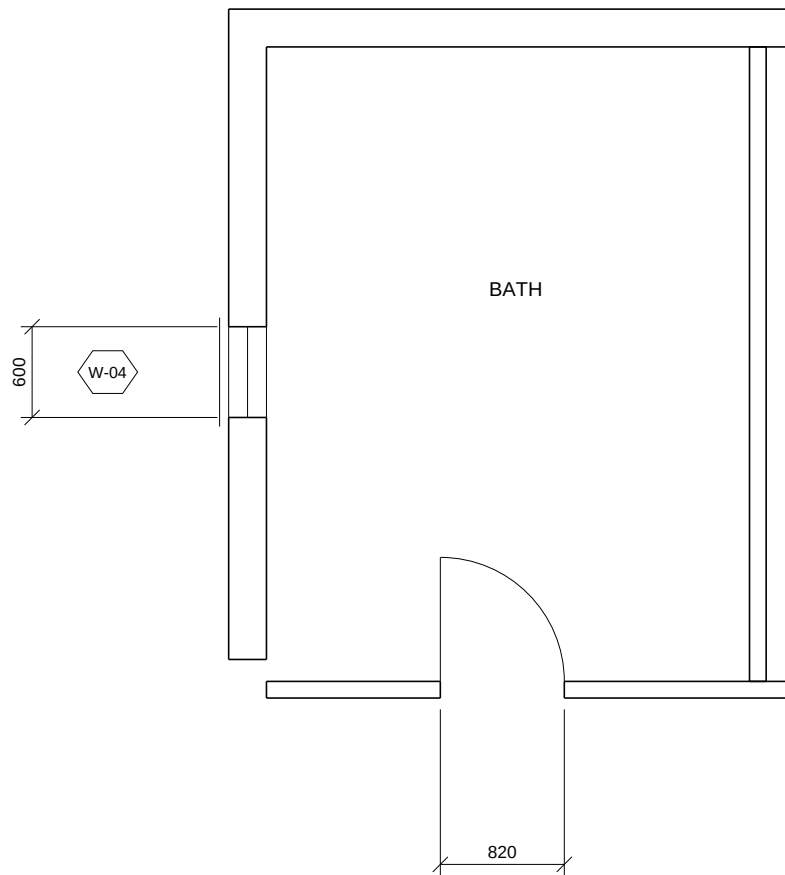

ENLARGED BATHROOM PLAN

SCALE 1:50

STUDIO NORTH ARCHITECTS RESIDENTIAL BUILDING 14 HARBOUR STREET, NORTHBRIDGE ALL DIMENSIONS IN MILLIMETRES UNLESS NOTED OTHERWISE, DO NOT SCALE.	DRAWING TITLE	
	ENLARGED BATHROOM PLAN	
	SCALE	DATE
	1:50	2026-09-01
	SHEET	REV
	A-501	B

DOOR SCHEDULE

MARK	TYPE	WIDTH	HEIGHT	QTY	REMARKS
D-01	ENTRY DOOR, SOLID CORE	1020	2100	1	
D-02	INTERNAL HINGED	820	2040	5	
D-03	GLAZED FRENCH DOORS	1600	2100	1	
SD-01	SLIDING GLASS DOOR	2400	2100	1	
GD-01	SECTIONAL GARAGE DOOR	2700	2100	1	

WINDOW SCHEDULE

MARK	TYPE	WIDTH	HEIGHT	SILL	QTY	REMARKS
W-01	AWNING	1200	1500	900	6	
W-02	FIXED + AWNING	1800	1500	900	3	
W-03	AWNING	900	1200	900	2	
W-05	SLIDING	1500	1200	900	2	
W-06	FIXED	900	900	1200	1	

NOTE: ALL SIZES ARE NOMINAL STRUCTURAL OPENING SIZES.

STUDIO NORTH ARCHITECTS RESIDENTIAL BUILDING 14 HARBOUR STREET, NORTHBRIDGE ALL DIMENSIONS IN MILLIMETRES UNLESS NOTED OTHERWISE. DO NOT SCALE.	DRAWING TITLE DOOR & WINDOW SCHEDULES	
	SCALE NTS	DATE 2026-09-01
	SHEET A-601	REV B